


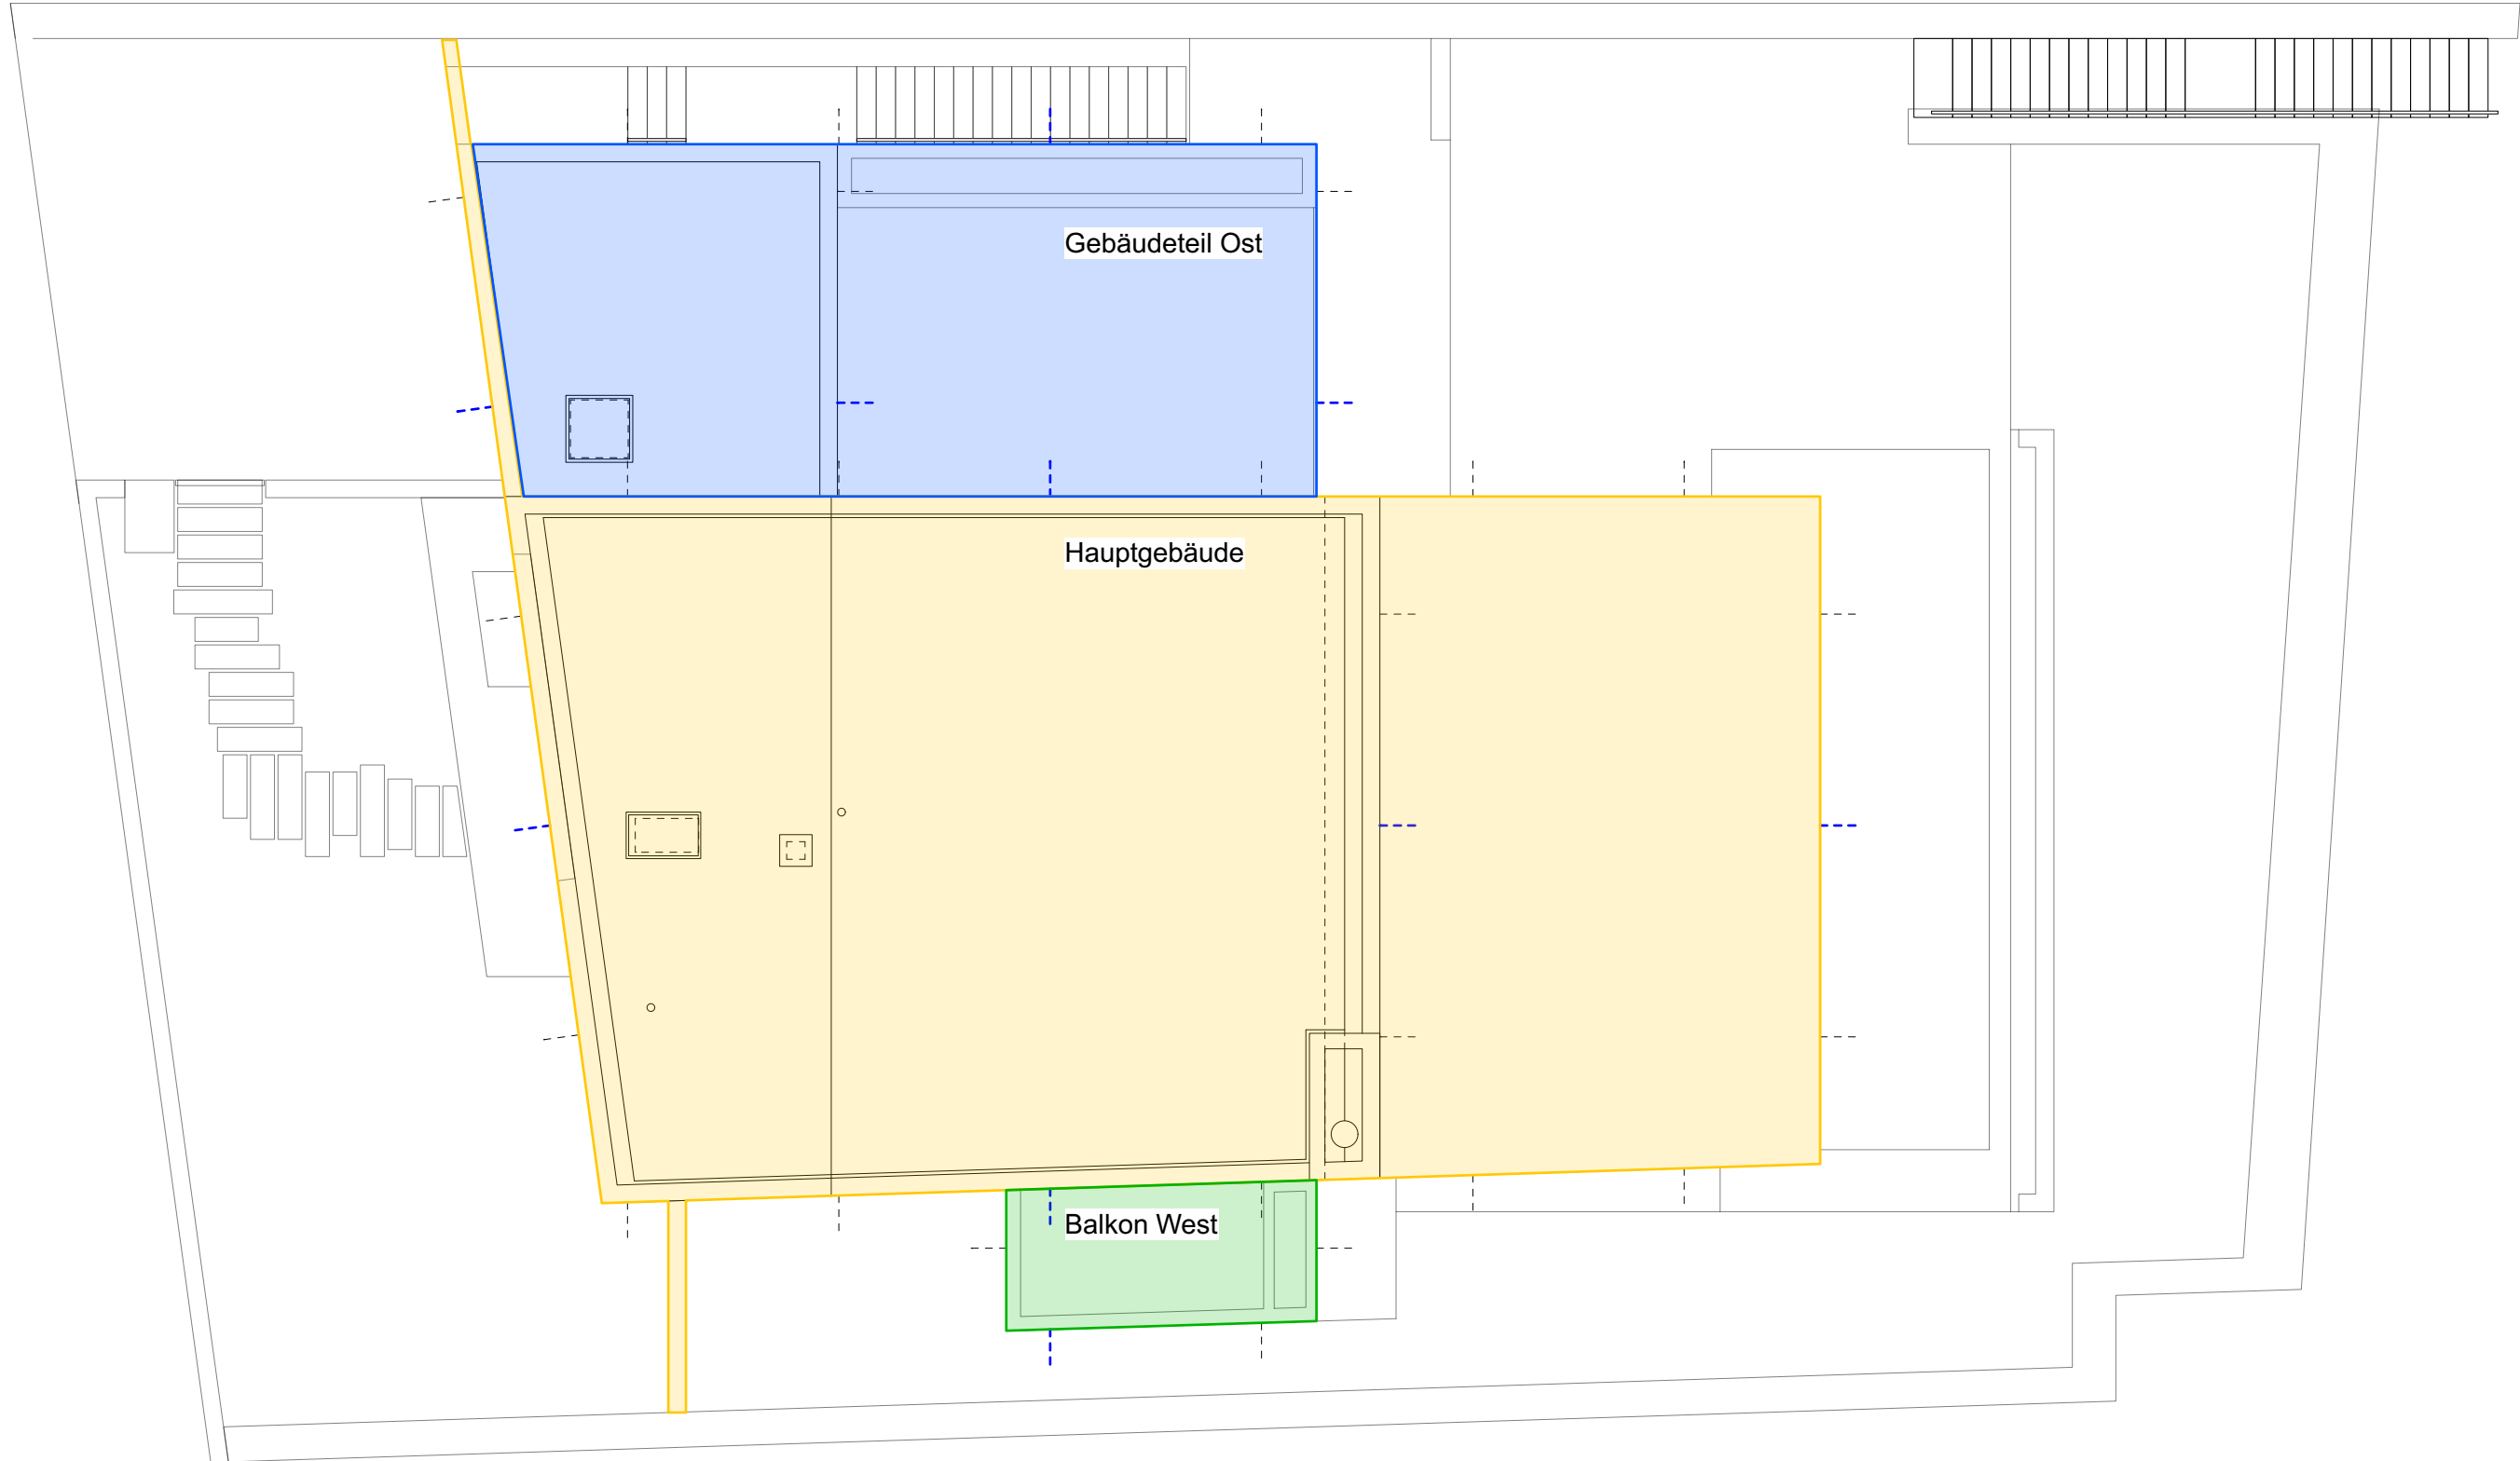


Generell:

- Fassade in Ortbeton, Weissbeton
- Schalungstyp 4.4
- Schaltafeln 3.0 x 0.93m Querformat
- Ankerlöcher in gleichm. Anordnung nach Vorgabe Arch.

Legende:

- Arbeitsfugen Betonierabschnitte
- Schaltafeln (Plattenformat 3.0 x 0.93m)
- - - Fugen von Fassade übernehmen

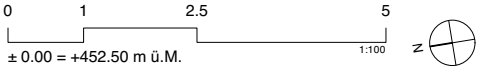


Meilen
Pfannenstielstrasse, 60. Neubau Einfamilienhaus.

Planbezeichnung
Wandansichten
Schalungsbild Übersicht

Architekt Wiel Arets Architects AG. Limmatstrasse 256, 8005 Zürich. T +41 43 818 6200 www.wielaretsarchitects.com


Plannummer	462	AP	430-01	B
	Projekt	Phase	Plan	Index
Massstab	1:100	Format	A3	
Datum	18.03.2025	gezeichnet / geprüft	EME / HSC	

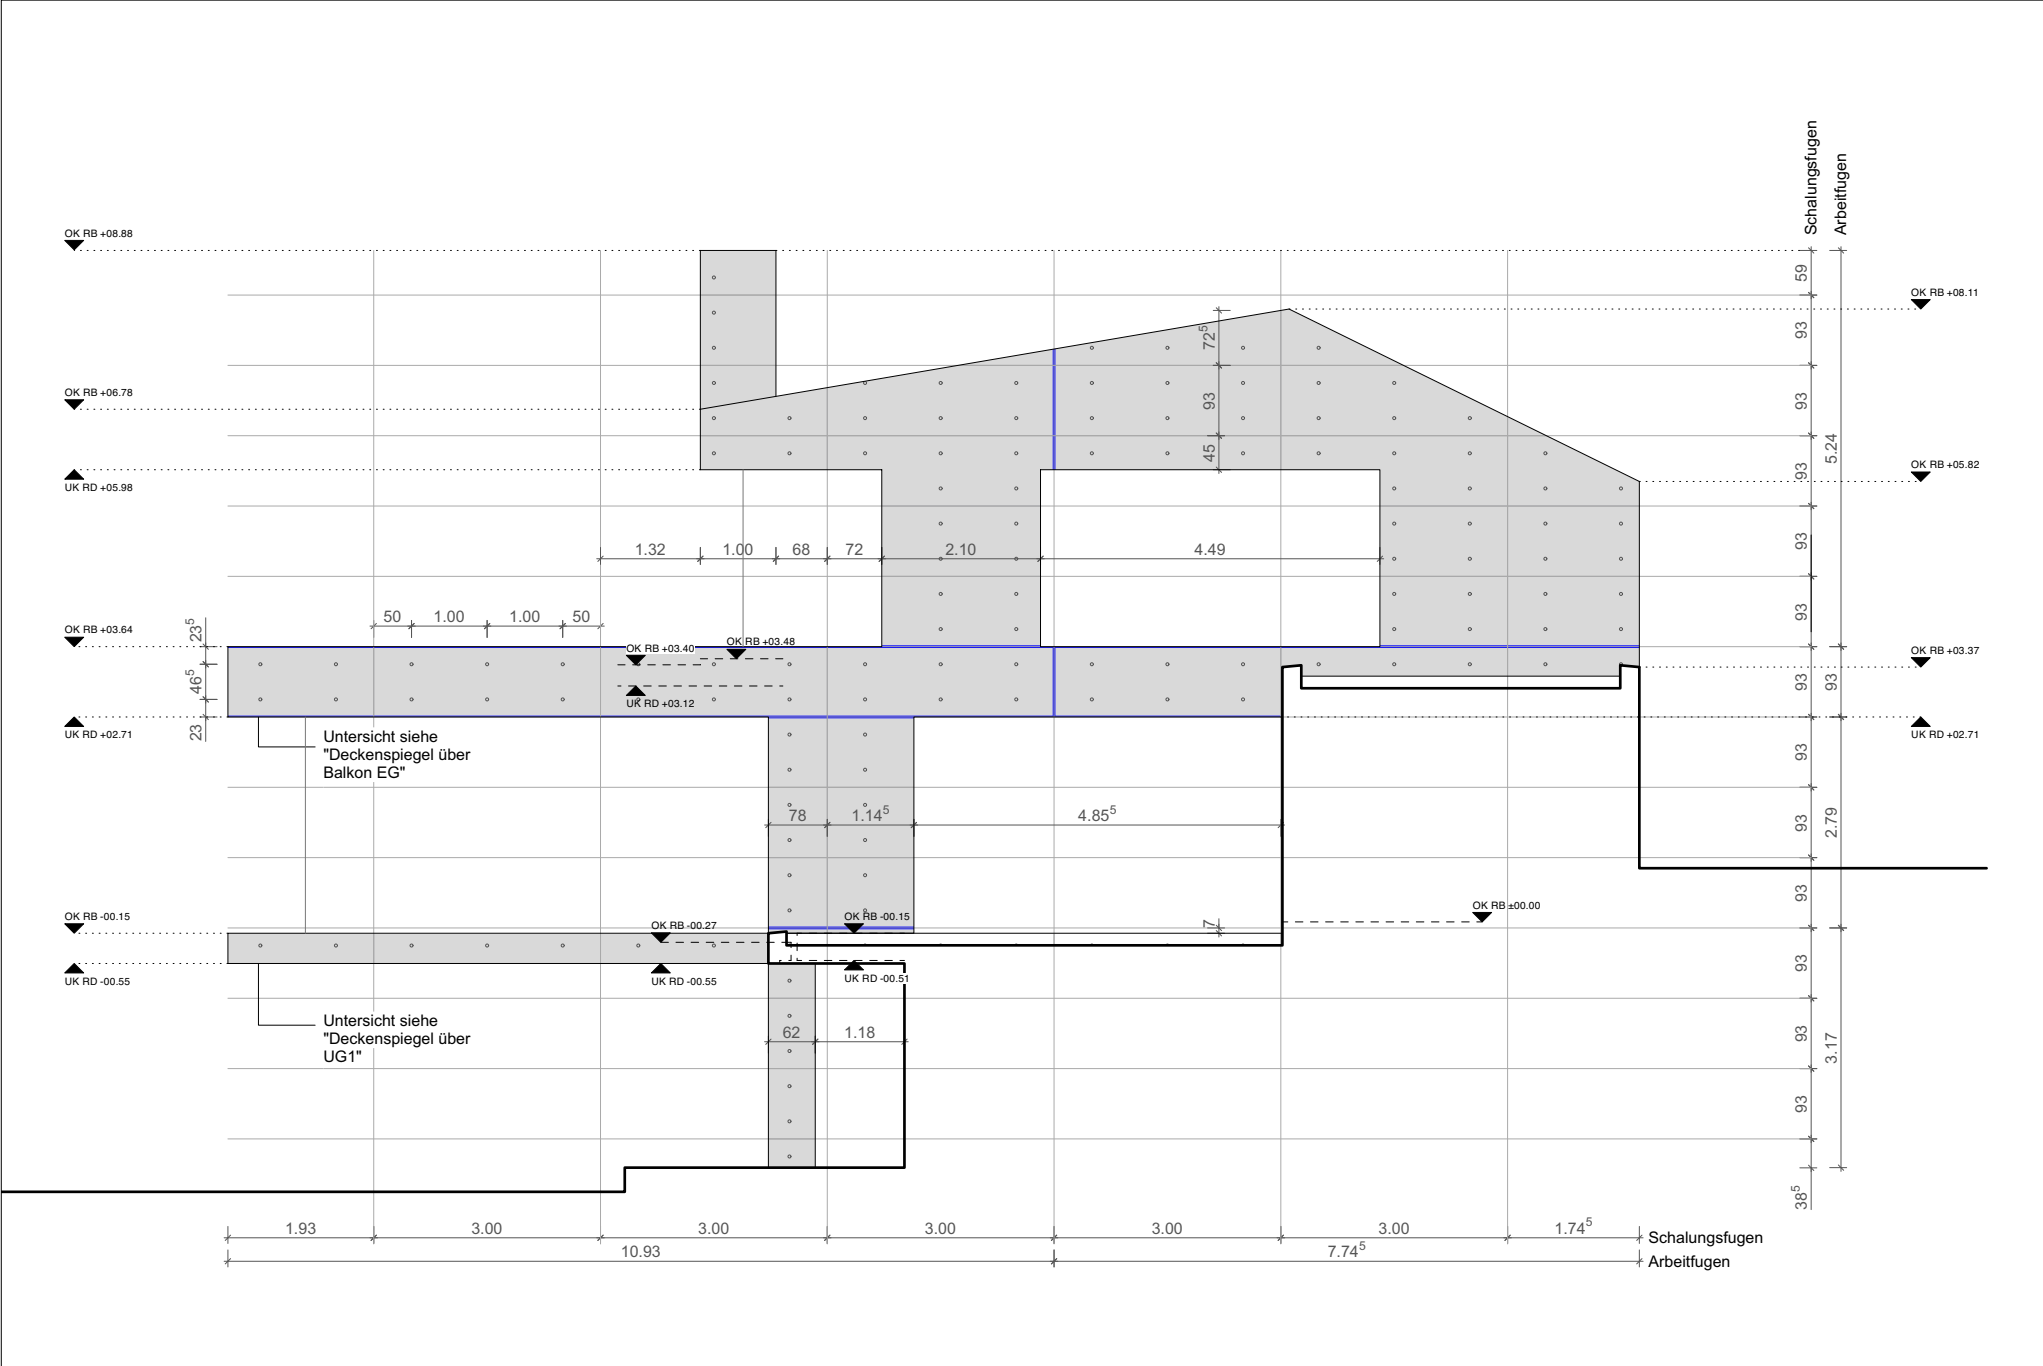

Hauptgebäude Ansicht Ost

- Generell:
- Fassade in Ortbeton, Weissbeton
 - Schalungstyp 4.4
 - Schaltafeln 3.0 x 0.93m Querformat
 - Ankerlöcher in gleichm. Anordnung nach Vorgabe Arch.
 - Alle Schalungsfugen in Leibung übernehmen

- Legende:
- Arbeitsfugen Betonierabschnitte
 - Schaltafeln (Plattenformat 3.0 x 0.93m)
 - Fugen von Fassade übernehmen

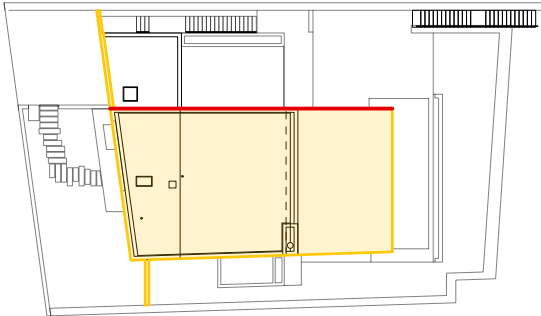

Meilen

Pfannenstielstrasse 60. Neubau Einfamilienhaus

Bauherrschaft / Grundeigentümer

Coleen Critchley und Gion Emanuel Pagnoncini
Schützenmattstrasse 3
8802 Kilchberg

Architekt

Wiel Arets Architects AG
Limmatstrasse 256, 8005 Zürich
www.wielaretsarchitects.com

WAA

Planbezeichnung

Wandansichten


Schalungsbild Ost
Hauptgebäude

Plannummer


462	AP	430-02	B
Projekt	Phase	Plan	Index

Massstab	1:100	Format	A3
----------	-------	--------	----

Datum	18.03.2025	gezeichnet / geprüft	EME / HSC
-------	------------	----------------------	-----------

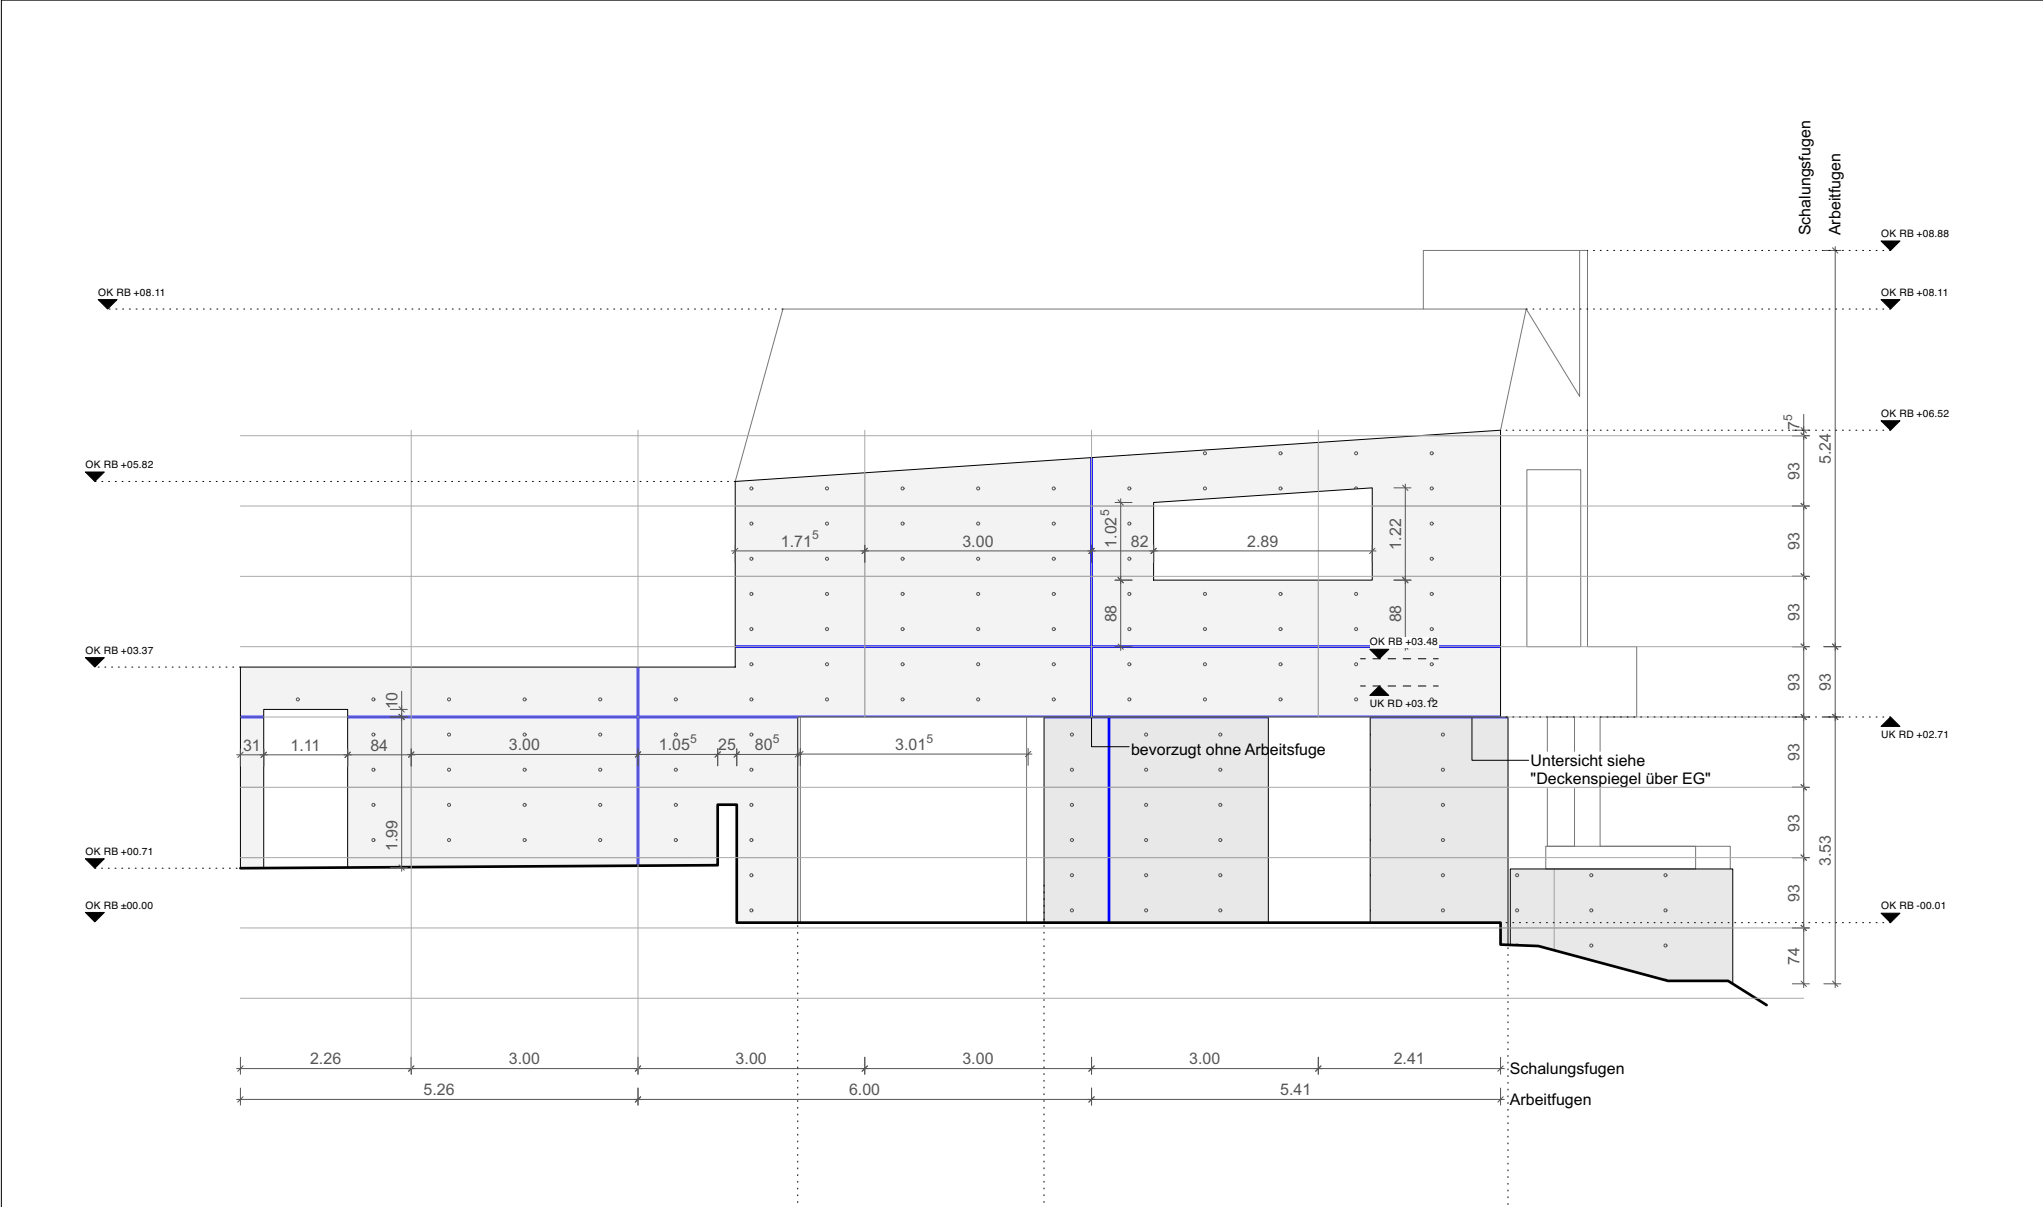


Hauptgebäude Ansicht Nord

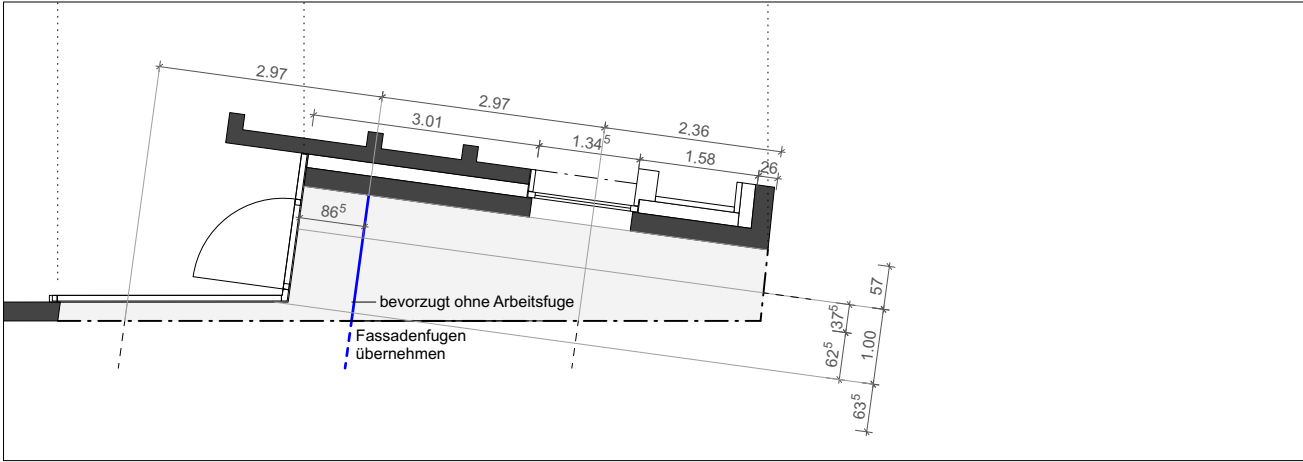

Deckenspiegel über EG

- Generell:
- Fassade in Ortbeton, Weissbeton
 - Schalungstyp 4.4
 - Schaltafeln 3.0 x 0.93m Querformat
 - Ankerlöcher in gleichm. Anordnung nach Vorgabe Arch.
 - Alle Schalungsfugen in Leibung übernehmen

- Legende:
- Arbeitsfugen Betonierabschnitte
 - Schaltafeln (Plattenformat 3.0 x 0.93m)
 - Fugen von Fassade übernehmen

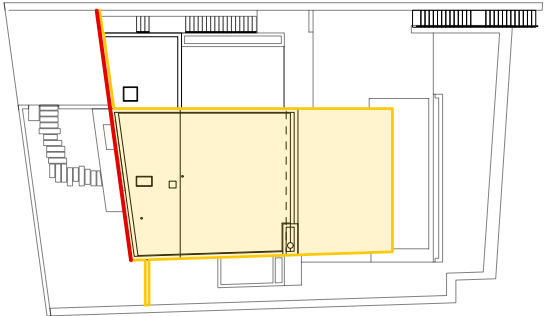

Meilen

Pfannenstielstrasse 60. Neubau Einfamilienhaus

Bauherrschaft / Grundeigentümer

Coleen Critchley und Gion Emanuel Pagnoncini
Schützenmattstrasse 3
8802 Kilchberg

Architekt

Wiel Arets Architects AG
Limmatstrasse 256, 8005 Zürich
www.wielaretsarchitects.com


WAA

Planbezeichnung


Wandansichten

Schalungsbild Nord
Hauptgebäude

Plannummer	462	AP	430-03	B
	Projekt	Phase	Plan	Index
Massstab	1:100	Format	A3	
Datum	18.03.2025	gezeichnet / geprüft	EME / HSC	

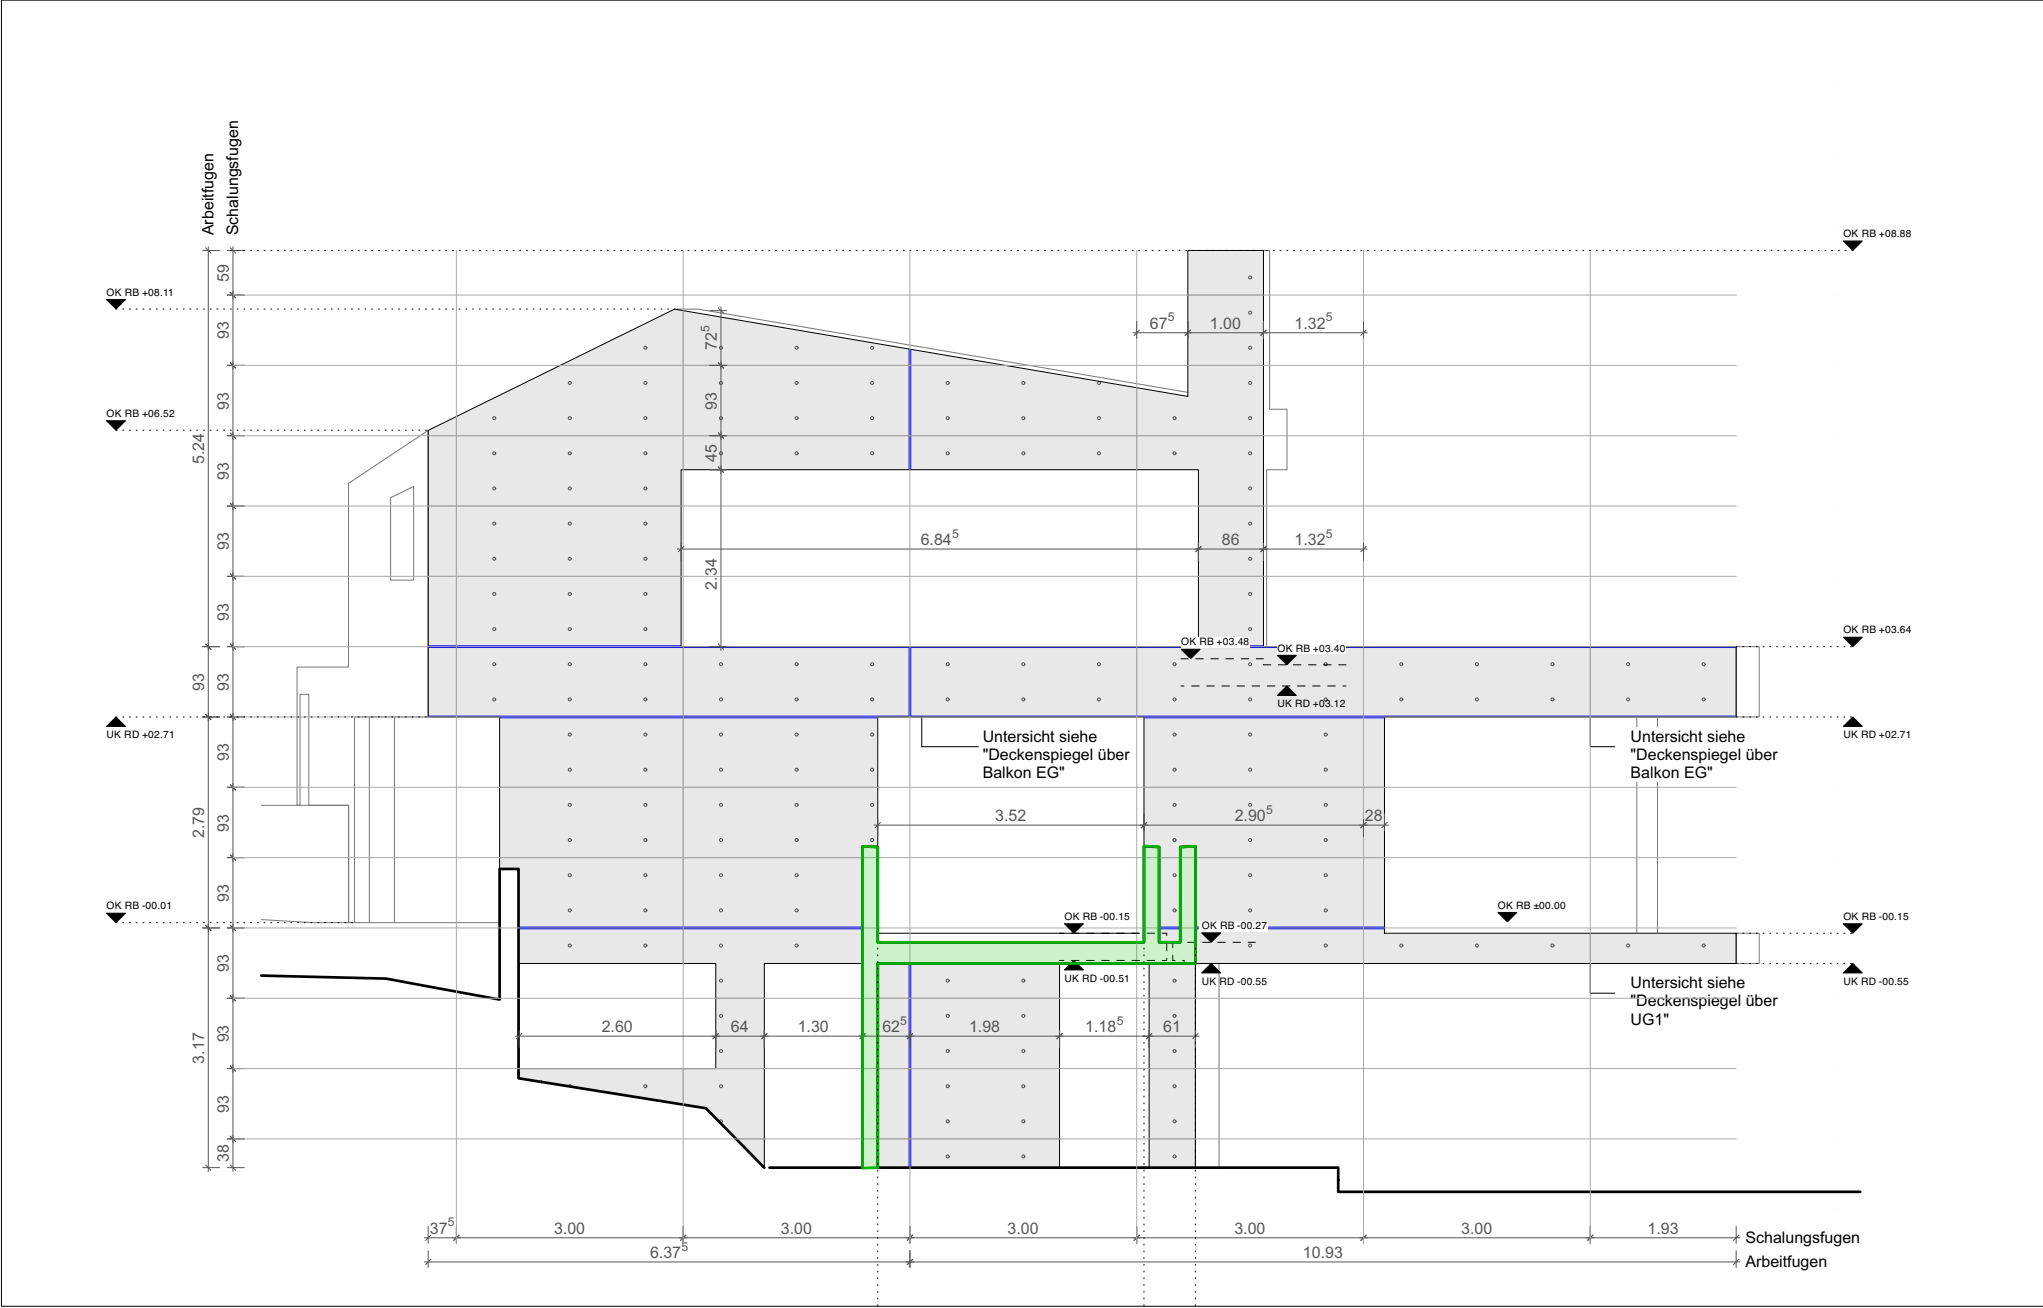


Hauptgebäude Ansicht West

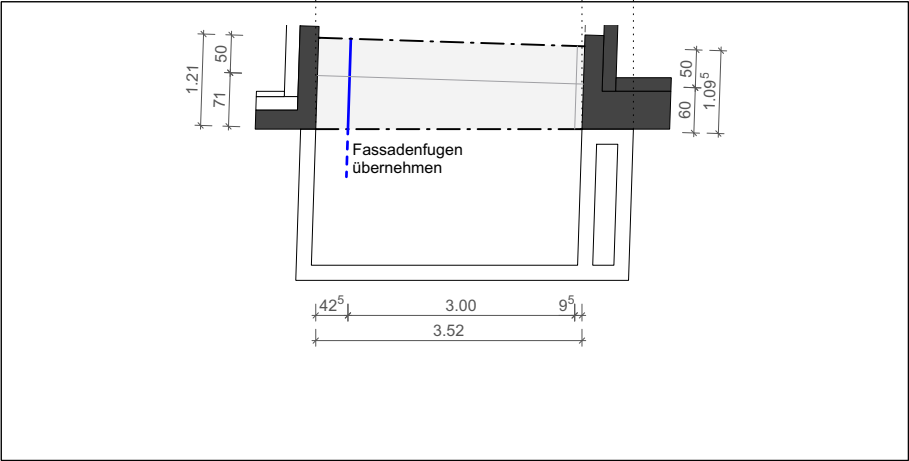

Deckenspiegel über Balkon EG

- Generell:
- Fassade in Ortbeton, Weissbeton
 - Schalungstyp 4.4
 - Schaltafeln 3.0 x 0.93m Querformat
 - Ankerlöcher in gleichm. Anordnung nach Vorgabe Arch.
 - Alle Schalungsfugen in Leibung übernehmen

- Legende:
- Arbeitsfugen Betonierabschnitte
 - Schaltafeln (Plattenformat 3.0 x 0.93m)
 - Fugen von Fassade übernehmen

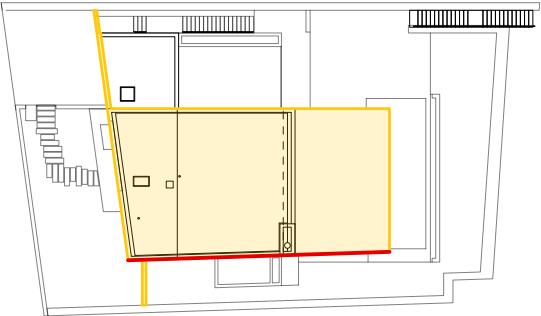

Meilen
Pfannenstielstrasse 60. Neubau Einfamilienhaus


Bauherrschaft / Grundeigentümer
Coleen Critchley und Gion Emanuel Pagnoncini
Schützenmattstrasse 3
8802 Kilchberg

Architekt
Wiel Arets Architects AG
Limmatstrasse 256, 8005 Zürich
www.wielaretsarchitects.com




Planbezeichnung
Wandansichten
Schalungsbild West
Hauptgebäude


Plannummer	462	AP	430-04	B
	Projekt	Phase	Plan	Index
Massstab	1:100	Format	A3	
Datum	18.03.2025	gezeichnet / geprüft	EME / HSC	

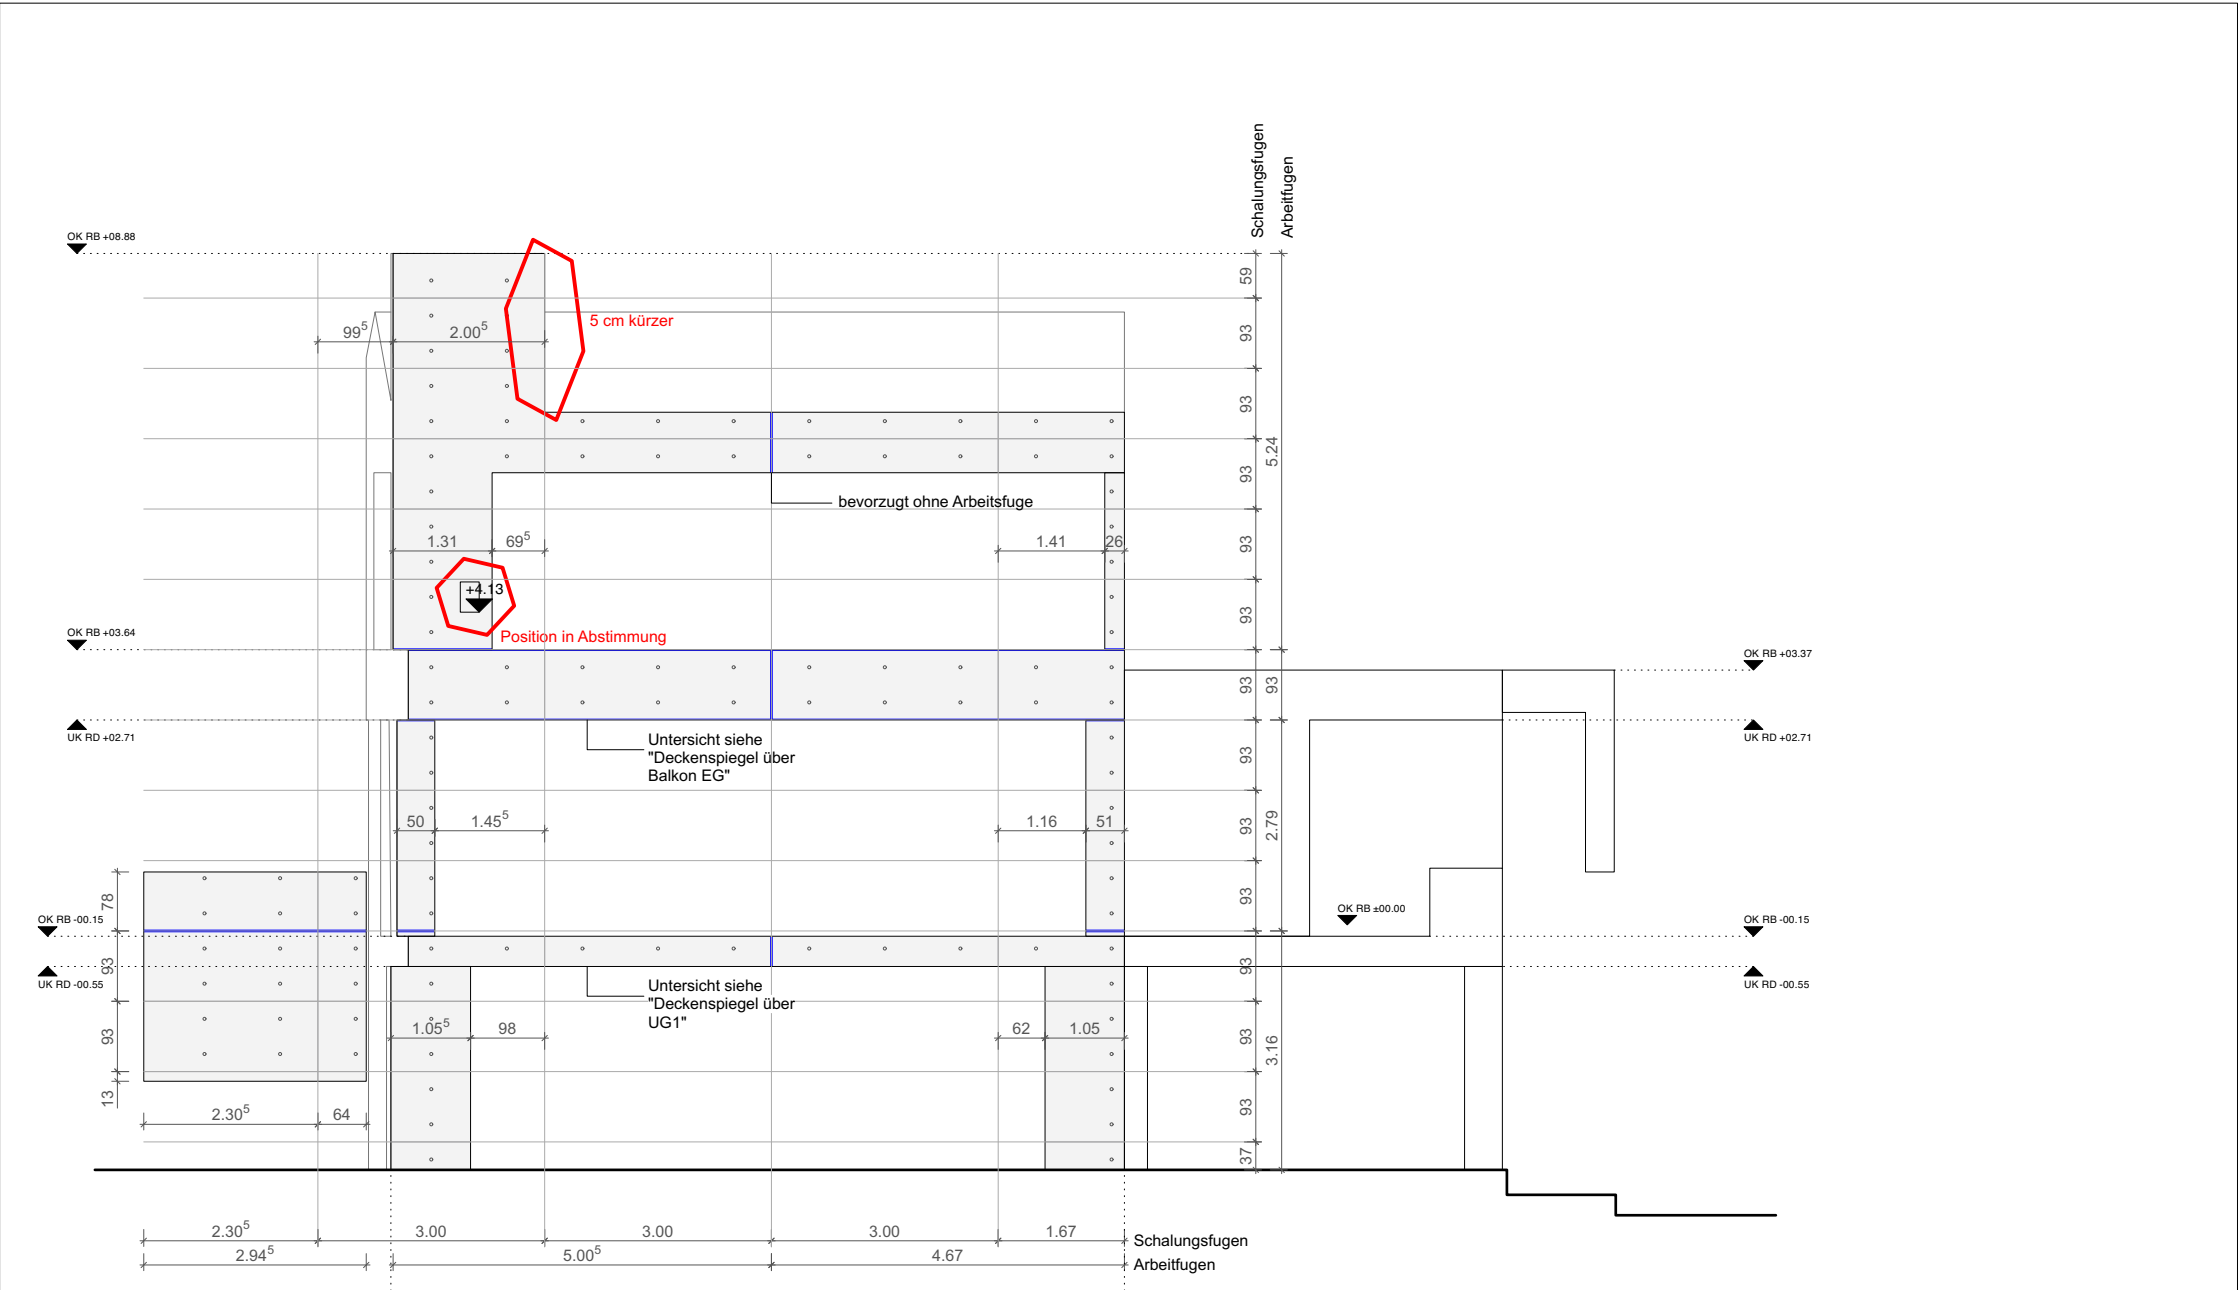

Hauptgebäude Ansicht Süd

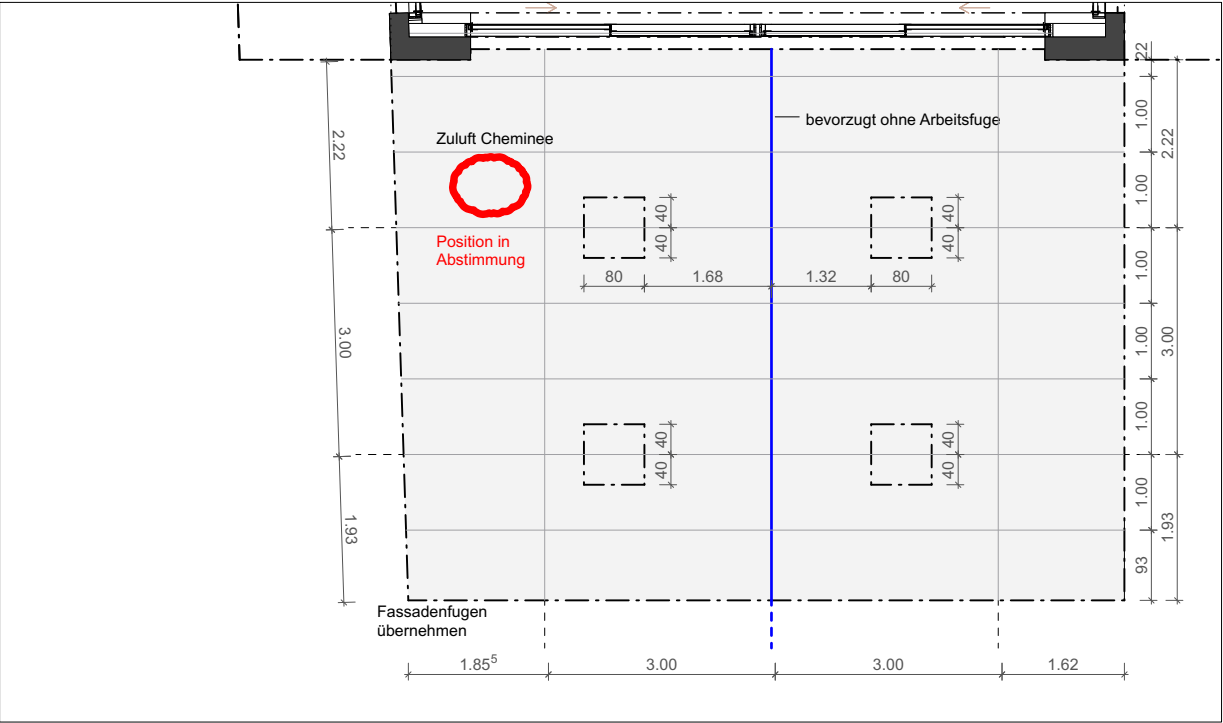


Deckenspiegel über UG1

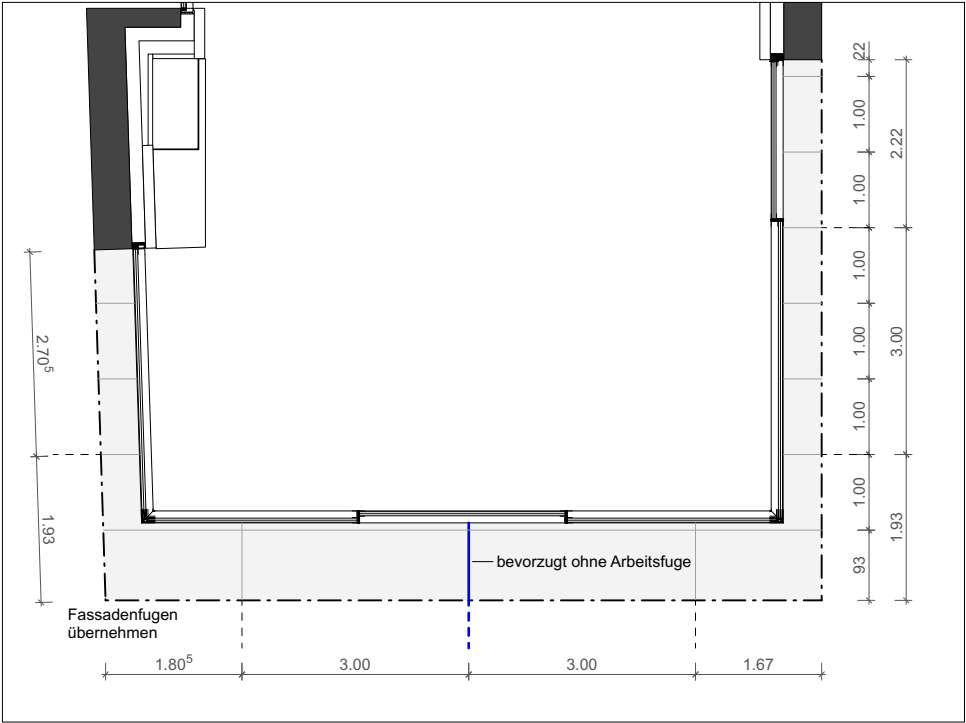

Deckenspiegel über Balkon EG

- Generell:
- Fassade in Ortbeton, Weissbeton
 - Schalungstyp 4.4
 - Schaltafeln 3.0 x 0.93m Querformat
 - Ankerlöcher in gleichm. Anordnung nach Vorgabe Arch.
 - Alle Schalungsfugen in Leibung übernehmen

- Legende:
- Arbeitsfugen Betonierabschnitte
 - Schaltafeln (Plattenformat 3.0 x 0.93m)
 - Fugen von Fassade übernehmen

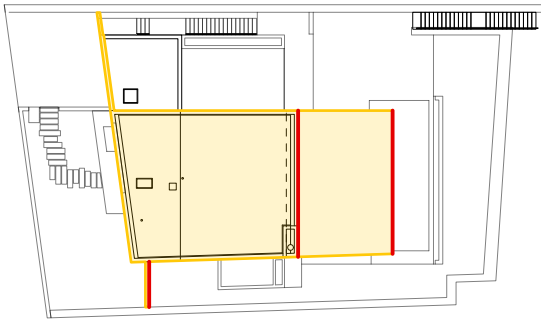

Meilen

Pfannenstielstrasse 60. Neubau Einfamilienhaus

Bauherrschaft / Grundeigentümer

Coleen Critchley und Gion Emanuel Pagnoncini
Schützenmattstrasse 3
8802 Kilchberg

Architekt

Wiel Arets Architects AG
Limmatstrasse 256, 8005 Zürich
www.wielaretsarchitects.com








WAA

Planbezeichnung

Wandansichten

Schalungsbild Süd
Hauptgebäude

Plannummer	462	AP	430-05	B
	Projekt	Phase	Plan	Index
Massstab	1:100	Format	A3	
Datum	18.03.2025	gezeichnet / geprüft	EME / HSC	

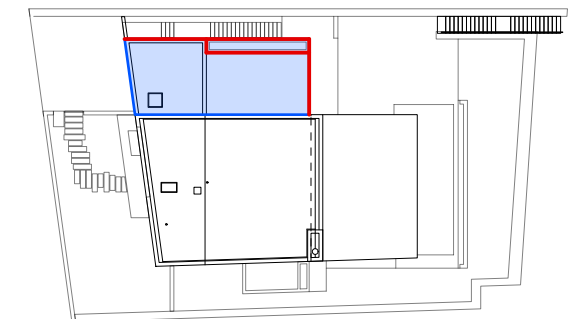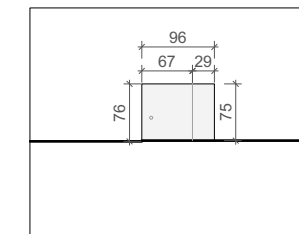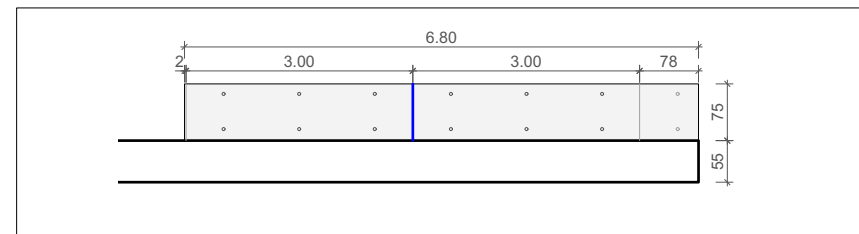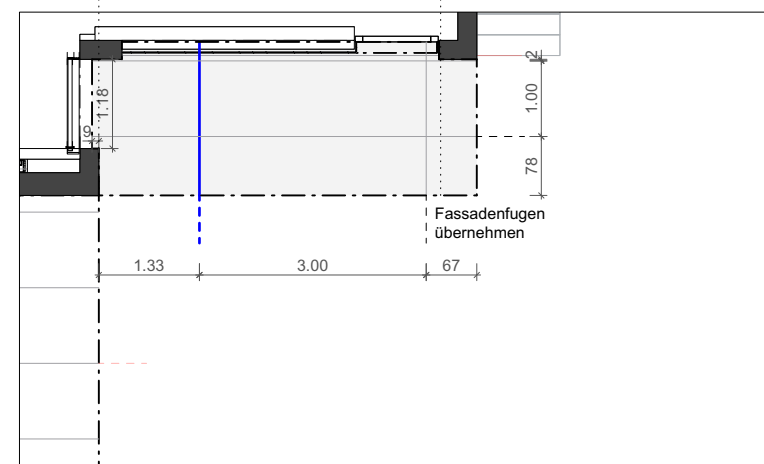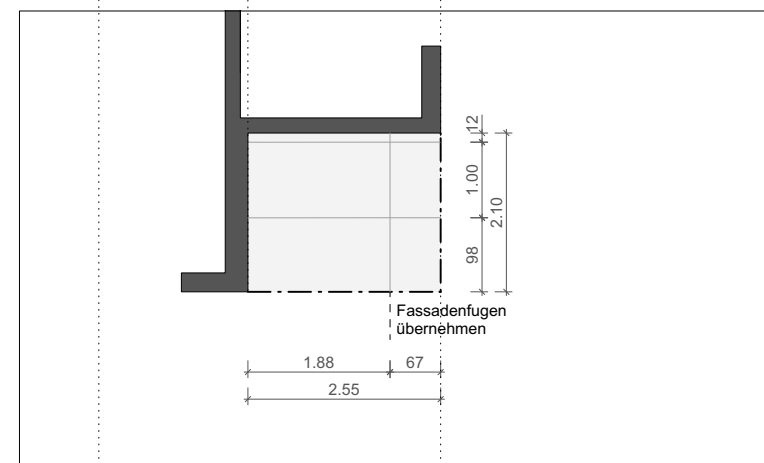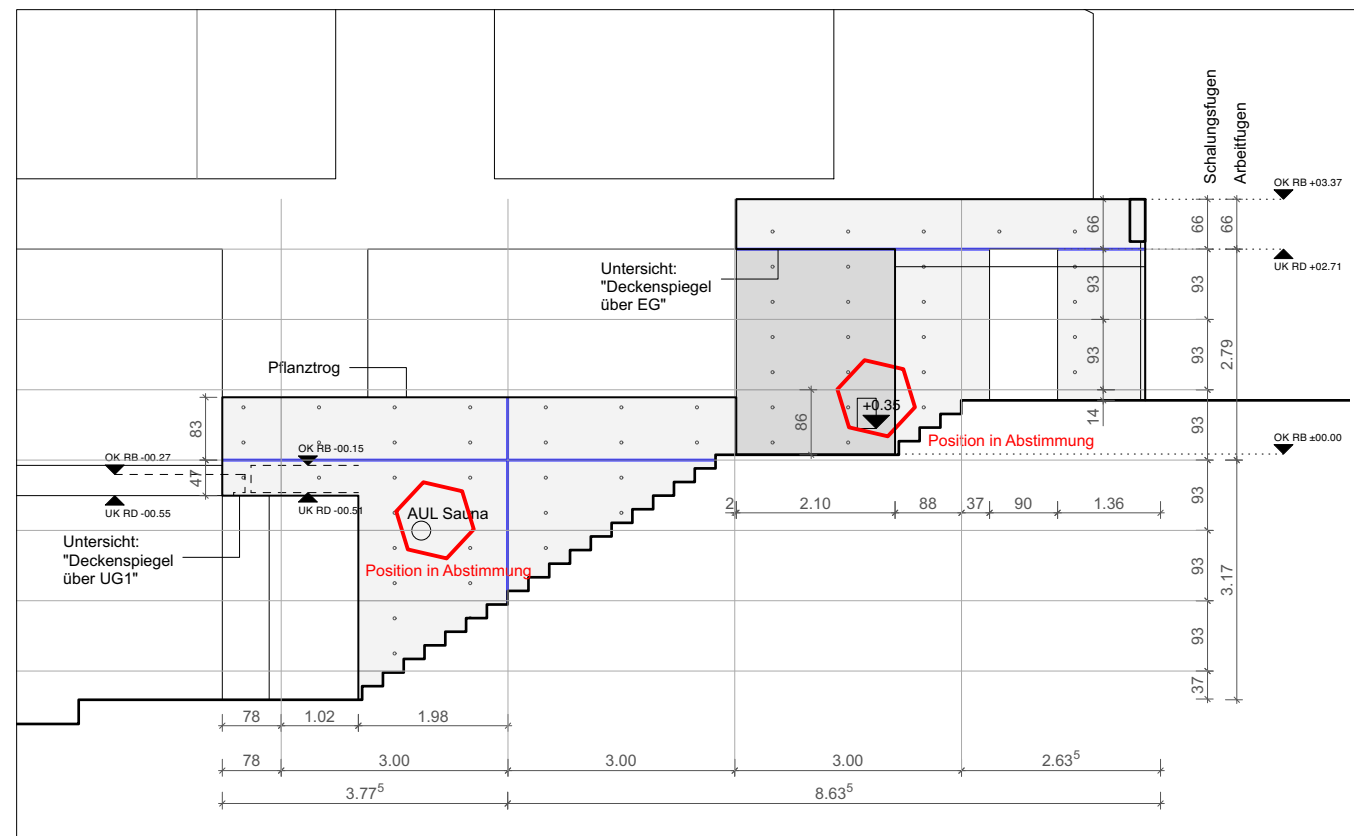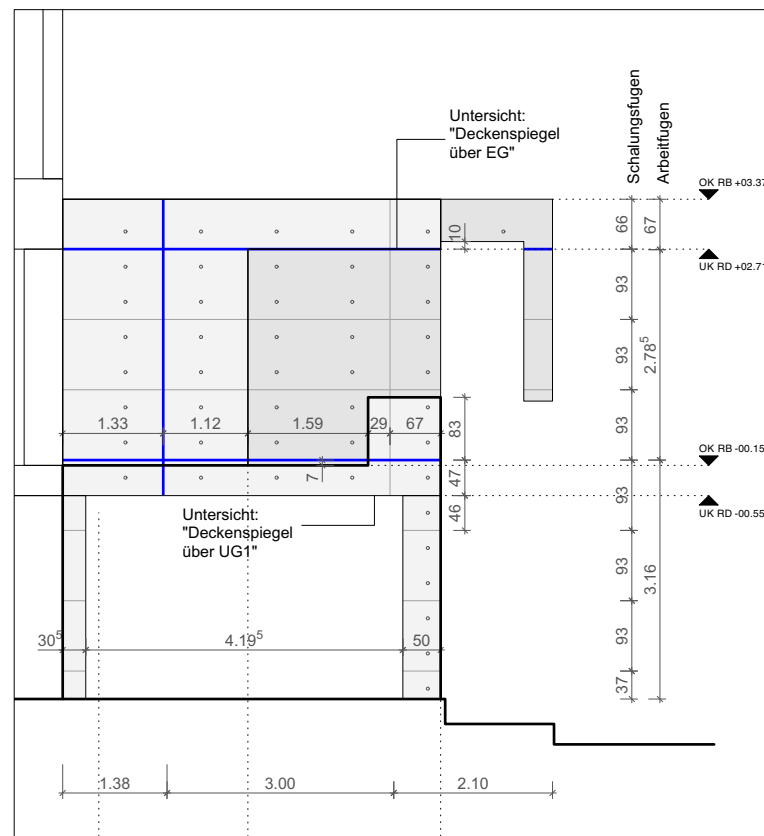

Generell:

- Fassade in Ortbeton, Weissbeton
- Schalungstyp 4.4
- Schaltafeln 3.0 x 0.93m Querformat
- Ankerlöcher in gleichm. Anordnung nach Vorgabe Arch.
- Alle Schalungsfugen in Leibung übernehmen

Legende:

- Arbeitsfugen Betonierabschnitte
- Schaltafeln (Plattenformat 3.0 x 0.93m)
- - - Fugen von Fassade übernehmen

Meilen

Pfannenstielstrasse 60. Neubau Einfamilienhaus

Bauherrschaft / Grundeigentümer

Coleen Critchley und Gion Emanuel Pagnoncini
Schützenmattstrasse 3
8802 Kilchberg

Architekt

Wiel Arets Architects AG
Limmatstrasse 256, 8005 Zürich
www.wielaretarchitects.com

WAA

Planbezeichnung

Wandansichten

Schalungsbild Ost und Süd

Gebäudeteil ost

Plannummer


462 | AP | 430-06 | B
Projekt Phase Plan Index

Massstab 1:100

Format	A3
--------	----

Datum	18.03.2025
-------	------------


gezeichnet / geprüft EME / HSC

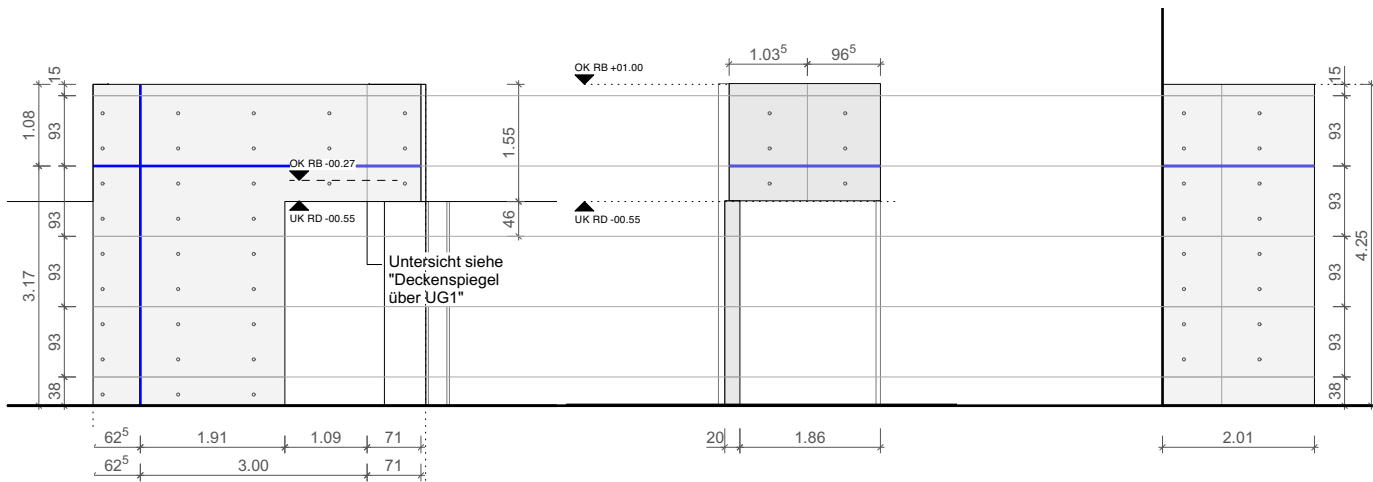


Ansicht West

Ansicht Süd

Ansicht Nord

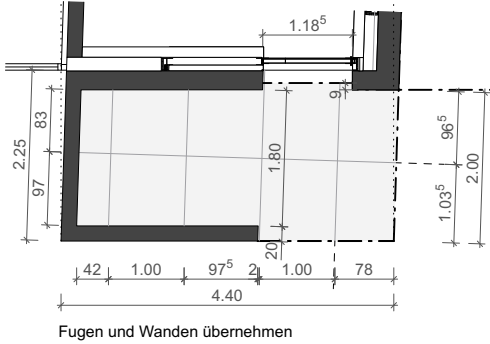

Deckenspiegel über UG1

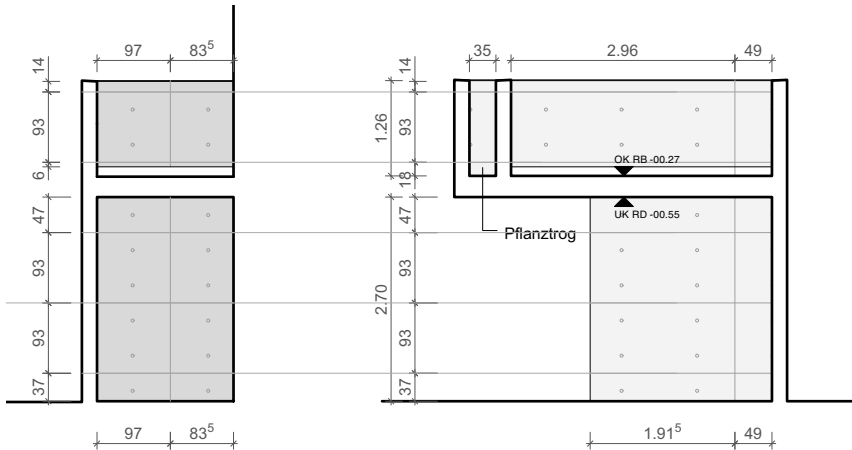

Innenansicht Süd

Innenansicht Ost

- Generell:
- Fassade in Ortbeton, Weissbeton
 - Schalungstyp 4.4
 - Schaltafeln 3.0 x 0.93m Querformat
 - Ankerlöcher in gleichm. Anordnung nach Vorgabe Arch.
 - Alle Schalungsfugen in Leibung übernehmen

- Legende:
- Arbeitsfugen Betonierabschnitte
 - Schaltafeln (Plattenformat 3.0 x 0.93m)
 - Fugen von Fassade übernehmen



Meilen

Pfannenstielstrasse 60. Neubau Einfamilienhaus

Bauherrschaft / Grundeigentümer

Coleen Critchley und Gion Emanuel Pagnoncini
Schützenmattstrasse 3
8802 Kilchberg

Architekt

Wiel Arets Architects AG
Limmatstrasse 256, 8005 Zürich
www.wielaretsarchitects.com

WAA

Planbezeichnung

Wandansichten

Schalungsbild

Balkon West

Plannummer

462 | AP | 430-07 | B
Projekt Phase Plan Index

Massstab 1:100

Format

A3

Datum 18.03.2025

gezeichnet / geprüft EME / HSC