


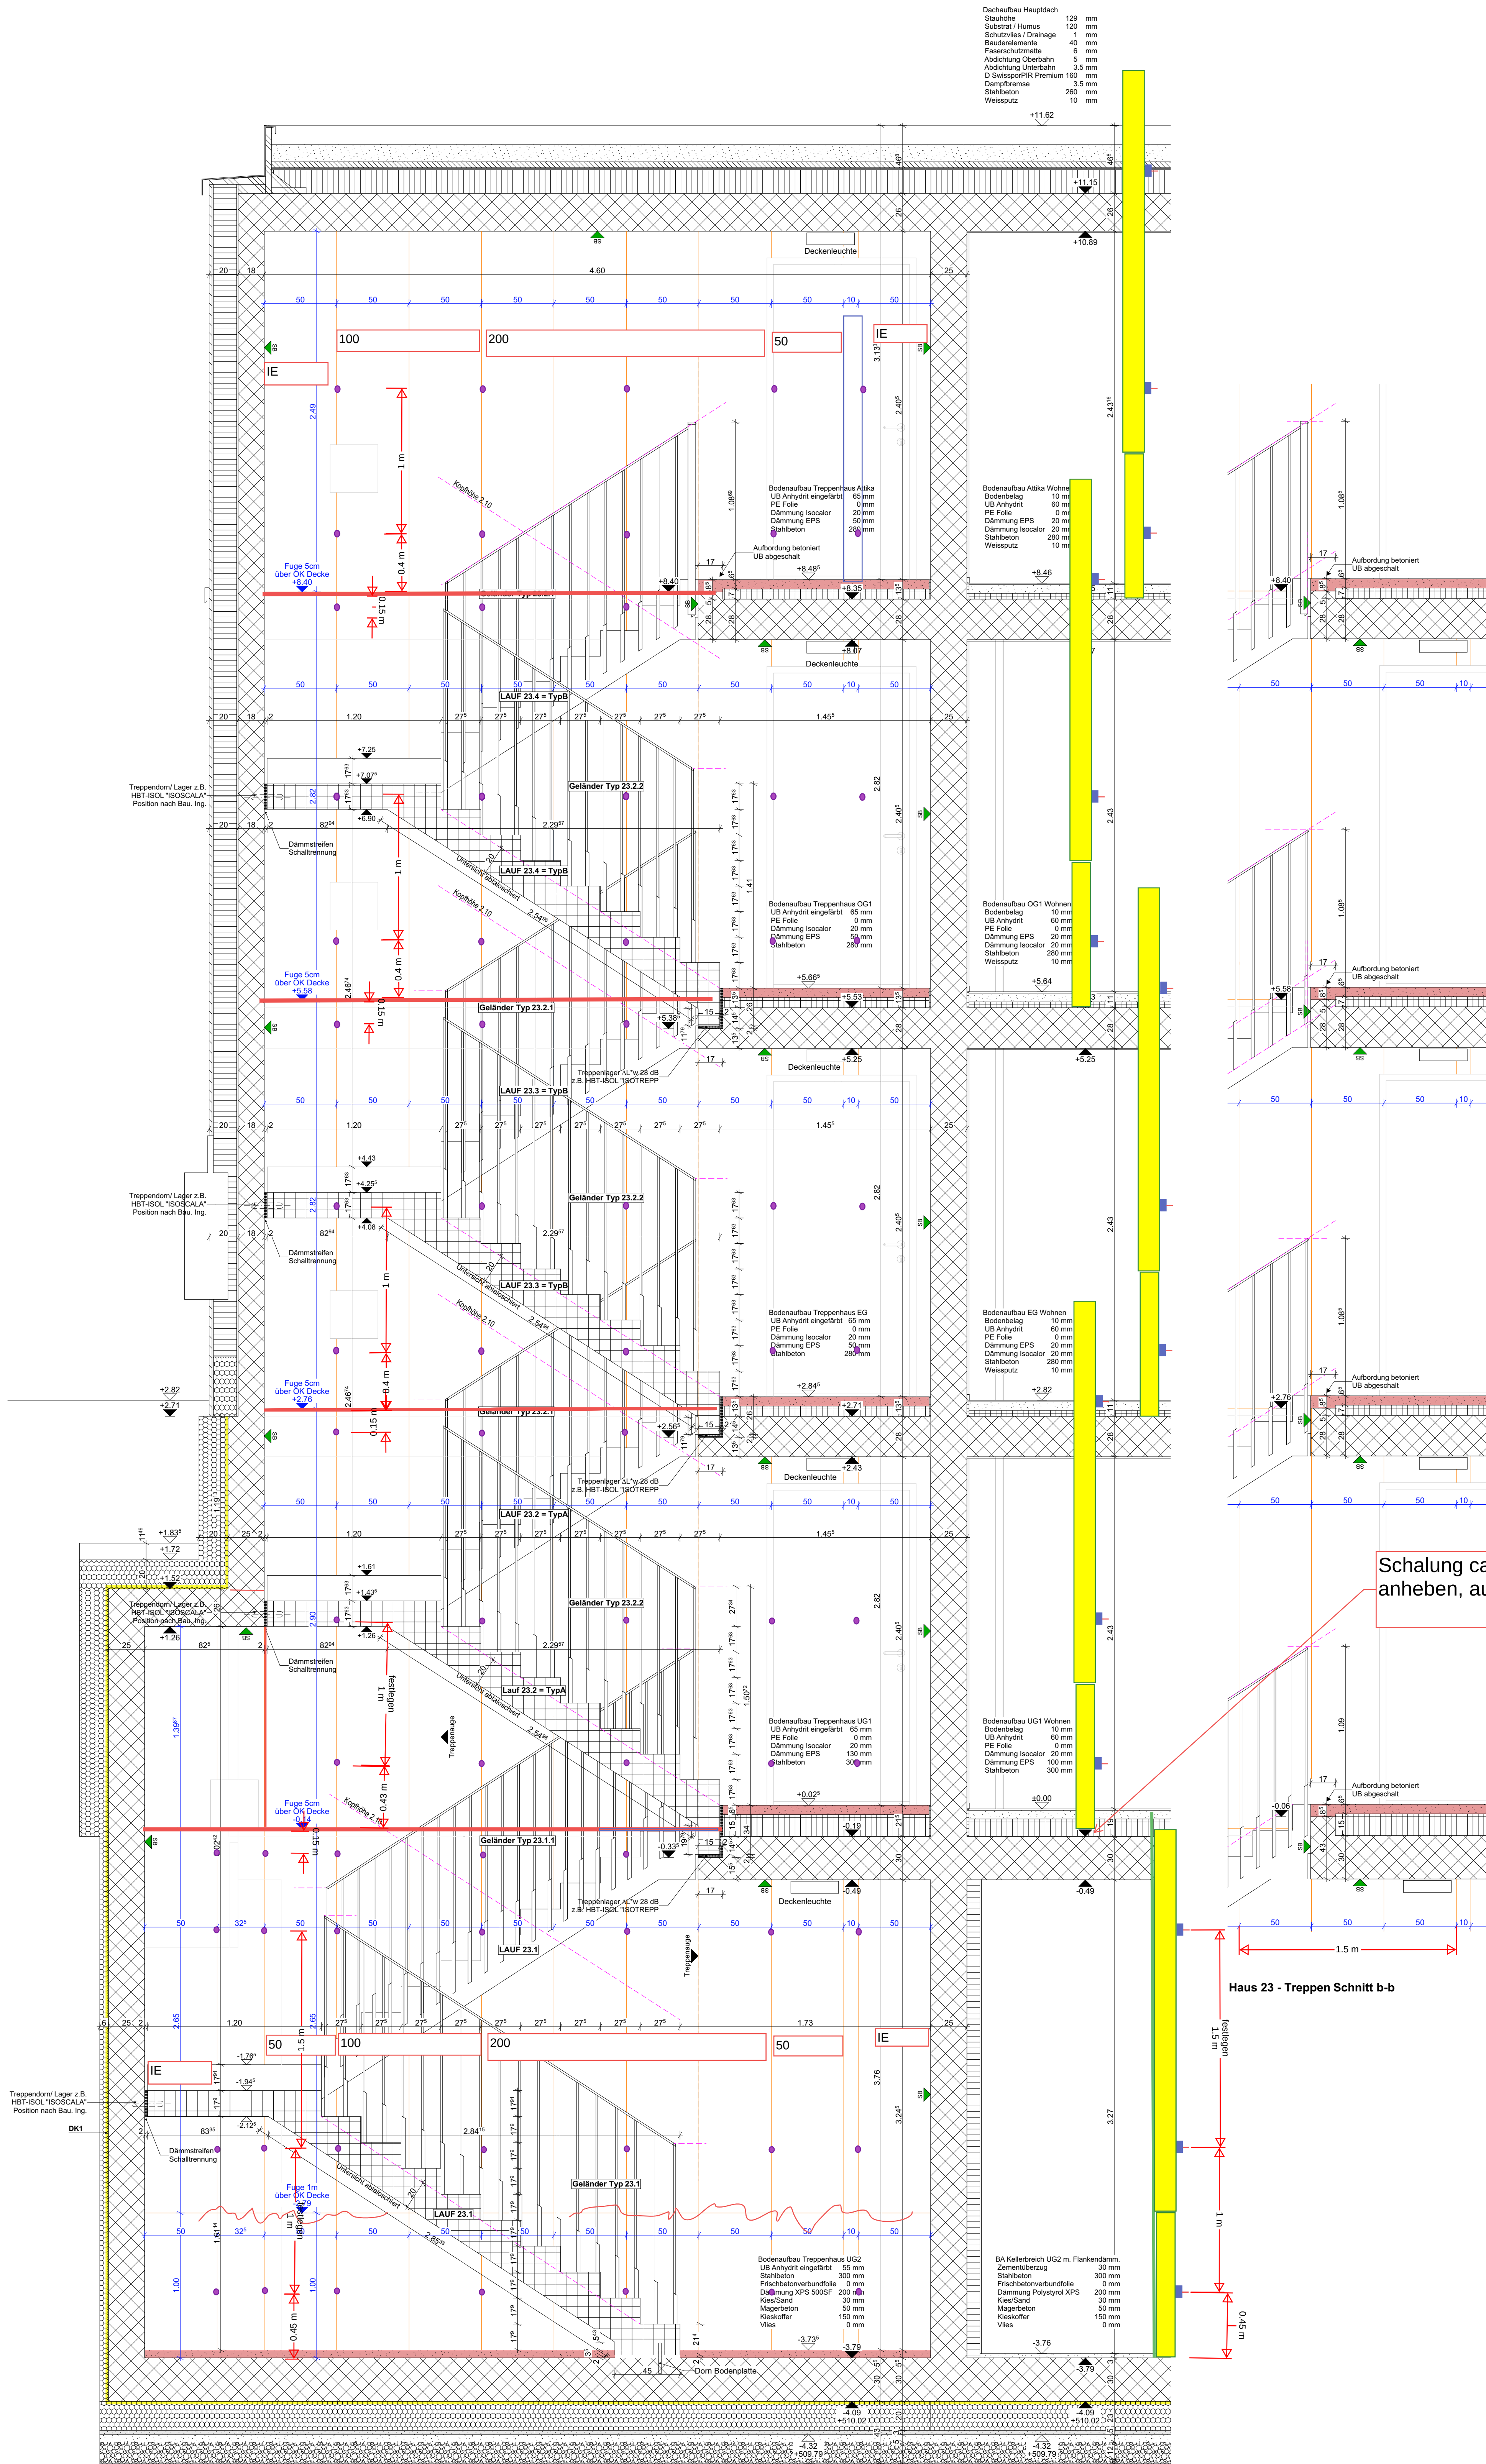

- Planlegende:**
Fertigteilelemente
- Oberfläche Sichtbeton
 - Transportlöcher ausgefüllt
 - Stufenkante 3mm gefast
 - Untersicht abtalschliert
- Planlegende für Sichtbeton SB:**
- Schalungstyp 2
 - geschosshohe Schalungsbretter, scharfkantig,
 - Bindlöcher horizontal und vertikal aufeinander ausge
 - bei sichtbarer Geschosdecke nur 1 Fuge

Die Koordinatenmasse sind Landeskoordinaten und sind vom Geometer einzumessen.
Der Unternehmer hat auf eigene Verantwortung sämtliche Masse am Bau auf ihre Richtigkeit zu kontrollieren.
Brandschutzkonzept, Nutzungs- und Sicherheitsplan sind integrierter Bestandteil der Ausführung und durch den Unternehmer sicher zu stellen.
Im Plan fehlende Masse sind bei der Bauleitung zu erfragen.
Vom Architekt werden keine Toleranzen eingeplant. Toleranzen sind mit der Bauleitung festzulegen.
Dieser Plan ist urheberrechtlich geschützt. Jegliche Weiterverwendung - auch auszugsweise - ist durch BGA Budelmann Gernert Architekten AG schriftlich genehmigen zu lassen. Die Urheber sind auf den Plänen wie unten auf diesem Plankopf als solche zu erwähnen.

A22163_51_23_32

PROJEKT:
A22163 Benedikt-Fontana-Weg 23 + 25
Zwei Mehrfamilienhäuser mit Tiefgarage
8049 Zürich Höngg, Parz. Nr. HG5843

PLANINHALT:
Haus 23 TH Schnitt a-a b-b
Mst: 1:20

BAUHERRSCHAFT:
Lotte + Adolf Holz-Sprenger Stiftung
Weberstrasse 66, 8134 Adliswil
kessel@ak-consulting.ch
043 336 30 90

ARCHITEKT:
Budelmann Gernert Architekten AG
Technoparkstr. 1
8005 Zürich
bgarch.ch
T 044 500 80 00

BAULEITUNG:
Caretta + Glitz AG
Seesstrasse 96
8700 Küsnacht
caretta-glitz.ch
T 043 222 31 80

INDEX:
C

LEGENDE:

B	Ortbofen	P	Parkett	GT	Gewachsenes Terrain	VW	Elektro/Multimediaverteiler
SB	Sichtbeton Oberfläche	H	Holz massiv	NT	Neues Terrain	BN	Bodenheizverteiler
VB	Beton vorfab. - Kunststein	WP	Weissputz	BF	Bodenfläche	WM	Wand
BN	Backstein	PL	Plattenbelag	FF	Fensterfläche	DGL	Deckengleittag
BN	Backstein nicht tragend	GK	Gipskarton	RA	Raumhöhe	BA	Bodenablauf
KN	Kalksandstein			W	Wand		
KN	Kalksandstein nicht tragend			RB	Kote OK roher Boden	MB	Metallfensterbank
MB	Magerbeton			FB	Kote OK fertig Boden	RAF	Raffamentenstrebe
HB	Hartholz			RD	Kote OK rohe Decke	VM	Verlärkmarkise
ZU	Zementüberzug	K	Kies	FD	Kote OK fertig Decke	SFL	Schieflage
U	Unterlagsboden	G	Geröll	RBR	Kote OK rohe Brüstung	VHS	Vorhangsbühne
D	Wärmedämmung			RSW	Kote OK rohe Schwelle	TS	Türschliesser
PD	Perimeterdämmung			RBR	Kote OK rohe Brüstung	P	Panelschloss
				FB	Kote OK fertig Brüstung	na	nicht abschliessbar
				RST	Kote OK rohe Sturz	SR	Schürzraum
				RST	Kote OK fertig Sturz	SP	Schürzplatte
				AK	Aussenkant	PD	Panzerdeckel
				OK	Oberrand	VA	Ventilationsregler
				UK	Unterrand	OV	Überdruckventil
				IL	im Licht	TC	Trockenloset
				Roh	Rohmass		
				Türhöhe	FS höherer Boden bis RST		

Index Datum Anpassung

A	12.11.2024	Def. Ausführungsplanung 1, Planstand
B	30.11.2024	Angabe Schalungstypen Treppenteller / TH 25 Attika Anpassung Treppenteller zu Whg
C	13.02.2025	Schalungstyp

Druckdatum 13.02.2025

Massstab 1:20

Format 84,1x95

team ID tg ak