
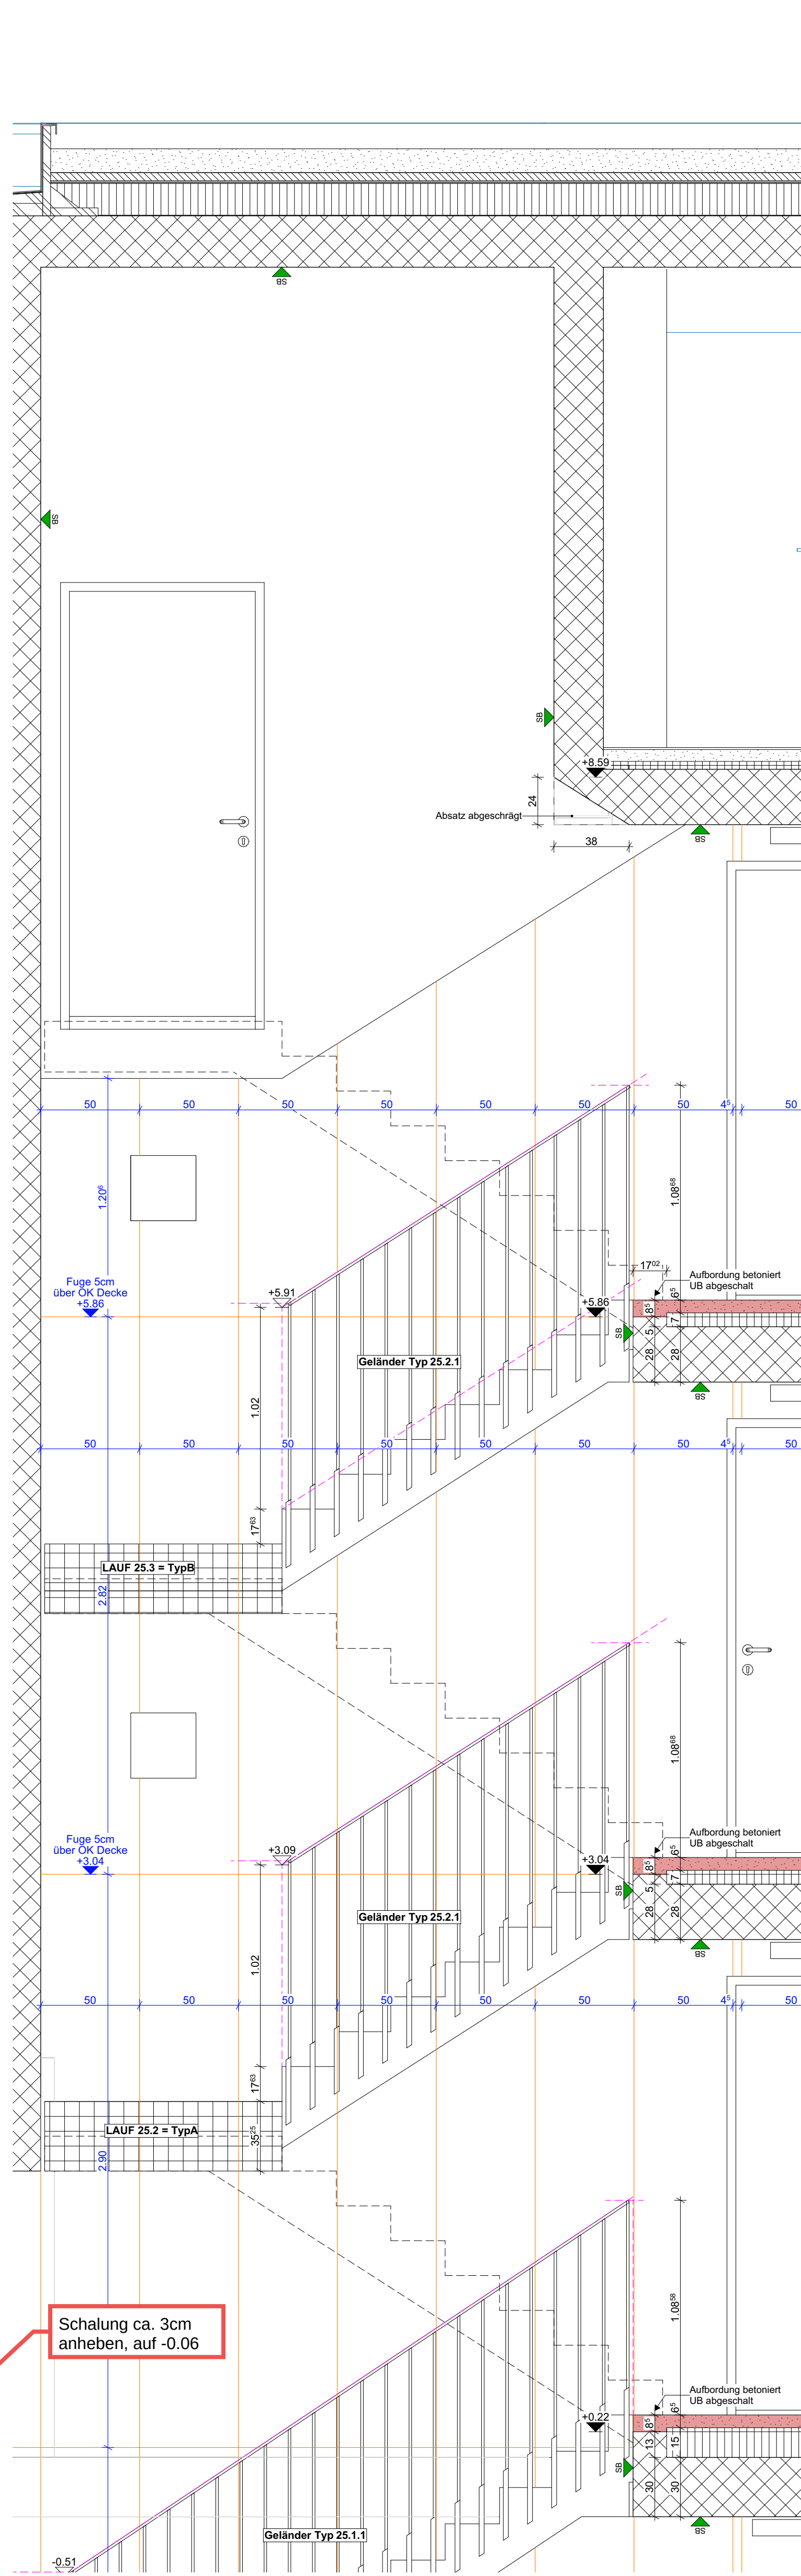


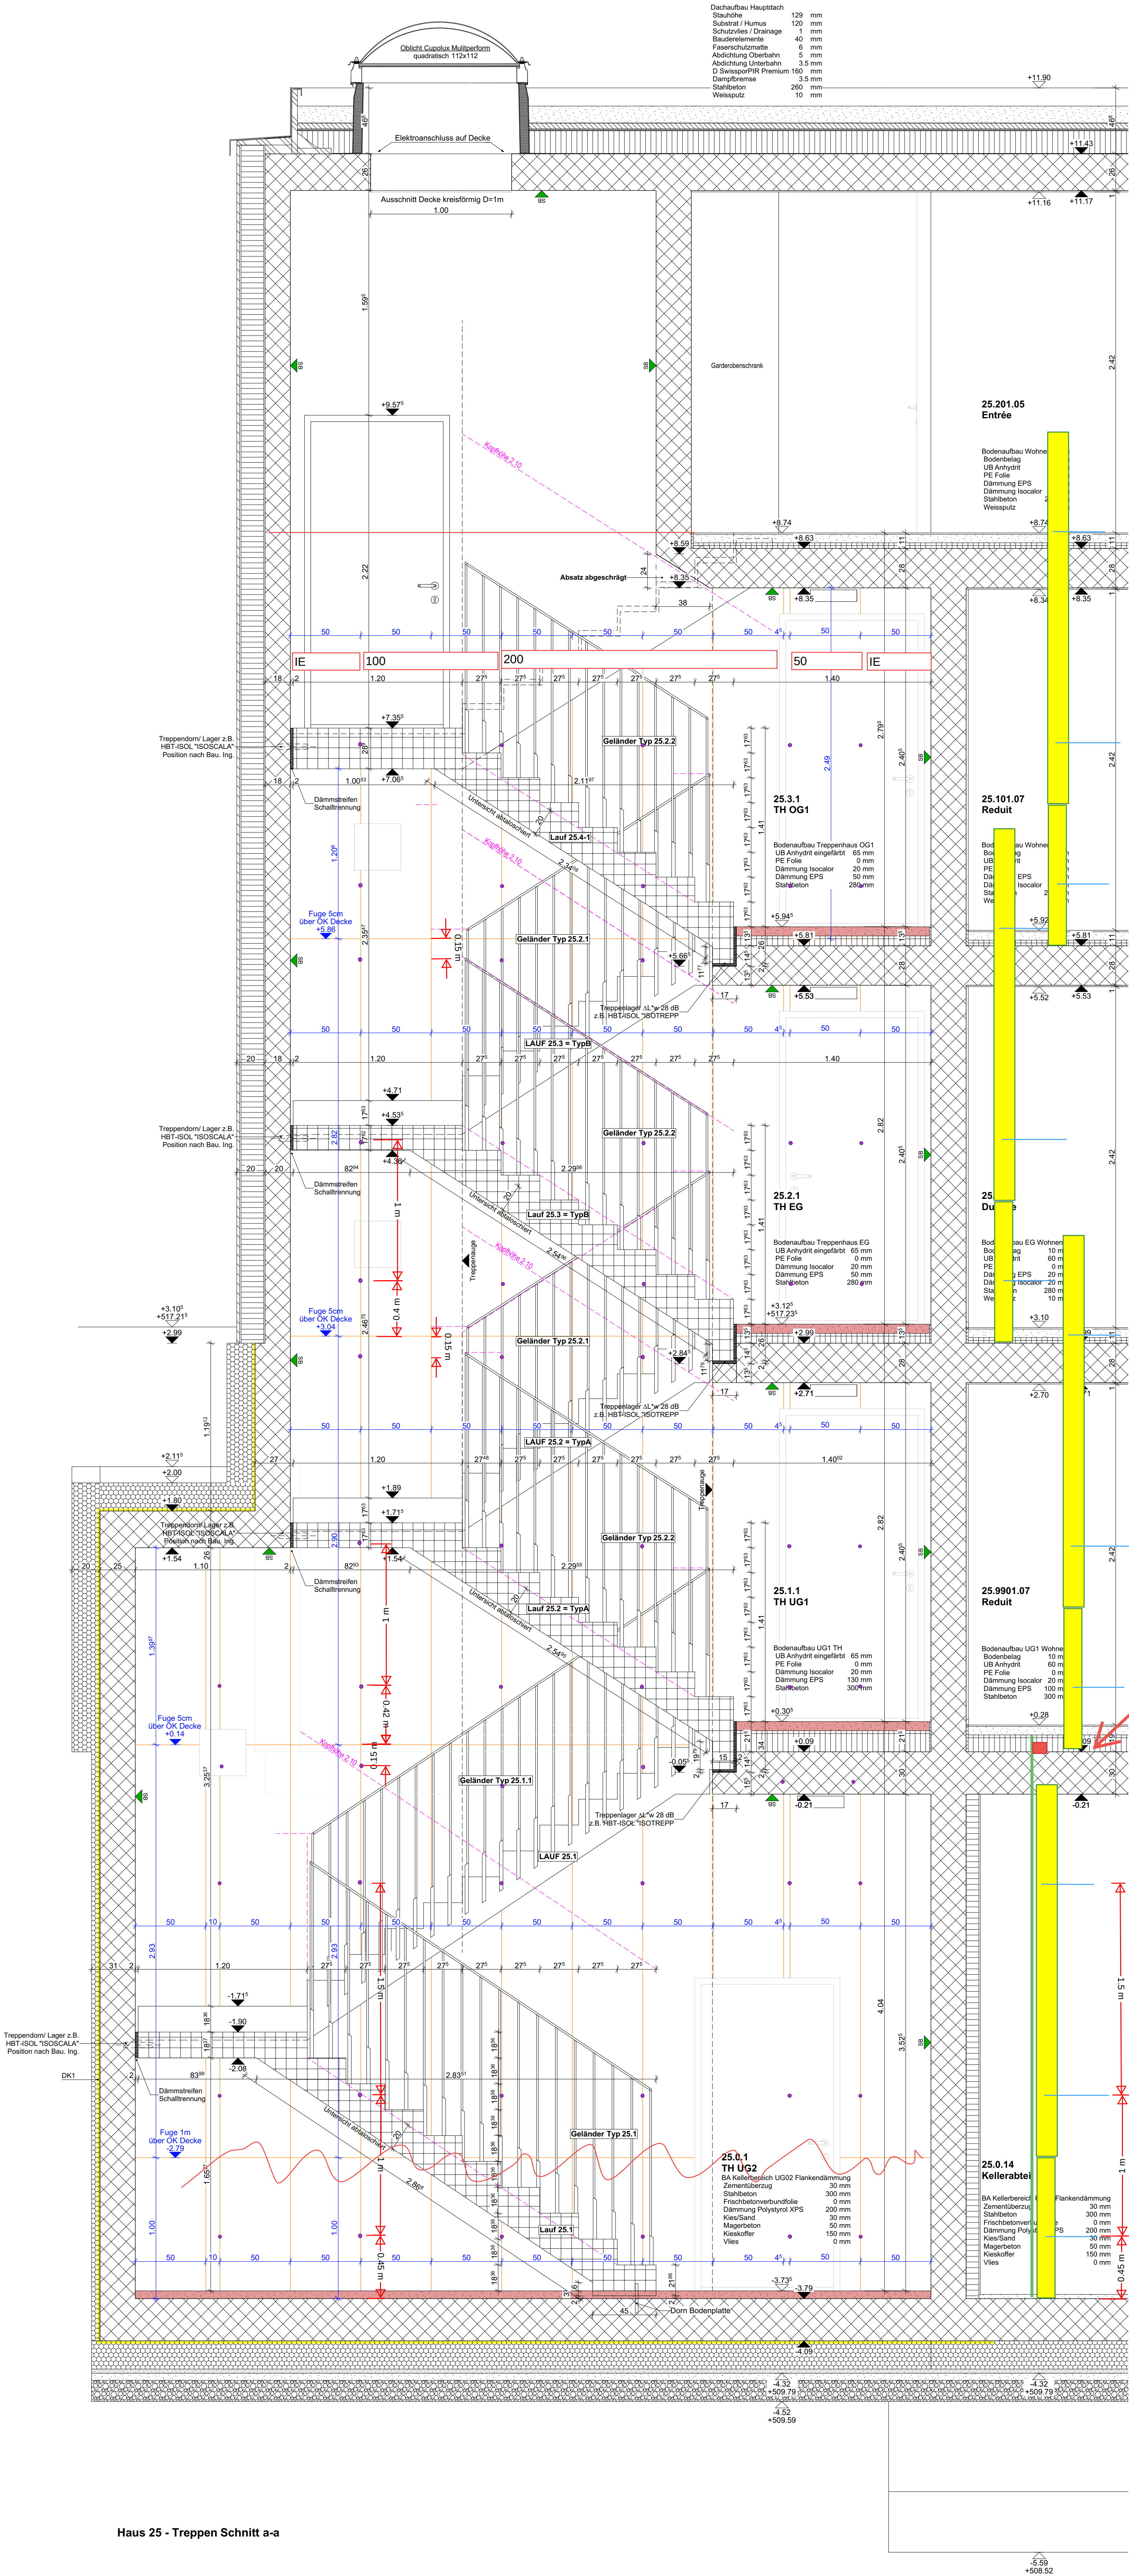

Haus 25 - Treppen Schnitt b-b

- Planlegende:**
Fertigtreppelemente
- Oberfläche Sichtbeton
 - Transportlöcher ausgefüllt
 - Stufenkante 3mm gefast
 - Untersicht abtischlosiert

- Planlegende für Sichtbeton SB:**
- Schalungstyp 2
 - geschosshohe Schalungstreter, scharfkantig,
 - Blindlöcher horizontal und vertikal aufeinander ausge
 - bei sichtbarer Geschosdecke nur 1 Fuge

Die Koordinatenmasse sind Landeskoordinaten und sind vom Geometer einzumessen.
Der Unternehmer hat auf eigene Verantwortung sämtliche Masse am Bau auf ihre Richtigkeit zu kontrollieren.
Brandschutzkonzept, Nutzungs- und Sicherheitsplan sind integrierter Bestandteil der Ausführung und durch den Unternehmer sicher zu stellen.
Im Plan fehlende Masse sind bei der Bauleitung zu erfragen.
Vom Architekt werden keine Toleranzen eingeplant. Toleranzen sind mit der Bauleitung festzulegen.

Dieser Plan ist urheberrechtlich geschützt. Jegliche Weiterverwendung - auch auszugsweise - ist durch BGA Budelmann Gernert Architekten AG schriftlich genehmigen zu lassen. Die Urheber sind auf den Plänen wie unten auf diesem Plankopf als solche zu erwähnen.

A22163_51_25_32

PROJEKT: A22163 Benedikt-Fontana-Weg 23 + 25 Zwei Mehrfamilienhäuser mit Tiefgarage 8049 Zürich Höngg, Parz. Nr. HG5843		BAUHERRSCHAFT: Lotte + Adolf Hotz-Sprenger Stiftung Weberstrasse 66, 8134 Adliswil
PLANINHALT: Haus 25 TH Schnitt a-a b-b Mst: 1:20		ARCHITEKT: Budelmann Gernert Architekten AG Technoparkstr. 1 8005 Zürich bgarch.ch T 044 500 80 00
BAULEITUNG: Caretta + Glitz AG Seestrasse 96 8700 Küsnacht caretta-glitz.ch T 043 222 31 80		INDEX:
LEGENDE: B Ortbeton SB Sichtbeton Oberfläche VB Beton vorlief., Kunststein BN Backstein KN Kalksandstein MB Magerbeton HB Hartbeton ZU Zementüberzug UB Unterlagboden D Wärmedämmung PD Perimeterdämmung P Parkett H Holz massiv WP Weissputz PL Plattenbelag GK Gipskarton S Stahl geschnitten E Erdreich K Kies G Geröll GT Gewachsenes Terrain NT Neues Terrain BF Bodenfläche FF Fensterfläche RA Raumnische B Boden D Decke W Wand RB Kote OK roher Boden FB Kote OK fertig Boden RD Kote OK rohe Decke FD Kote OK fertig Decke RBR Kote OK rohe Brüstung RSW Kote OK rohe Schwelle RBR Kote OK fertig Brüstung RST Kote OK fertig Sturz AK Ausserkante OK Oberkante UK Unterkante IL im Licht TL im Rohr Türhöhe FS höherer Boden bis RST VW Elektro/Multimediaverteiler BVV Bodenheizverteiler VM TV Viaschrum DGL Deckengleittiger BA Bodenablauf MFB Metallfensterbank RAF Raffalamentore VM Vertikalmarkise SFL Schenklügel VHS Vorhangschiene TS Türschliesser P Panzerdeckel SR Schutzraum PT Panzerplatte V Ventilationsregulator OV Überdruckventil TC Trockenklosett		Index Datum Anpassung 12.11.2024 Def. Ausführungsplanung 1. Planstand 30.11.2024 Angabe Schalungsmass Treppentage / TH 25 Adika Anpassung Treppentage zu Whg 14.01.2024 Wechsel oberster Lauf von Fertigblech zu Ortbetonlauf 13.02.2025 Schalungstyp
Druckdatum 13.02.2025		Massstab 1:20
Format 84,1x95		team ID tg ak