Grundriss 1:50

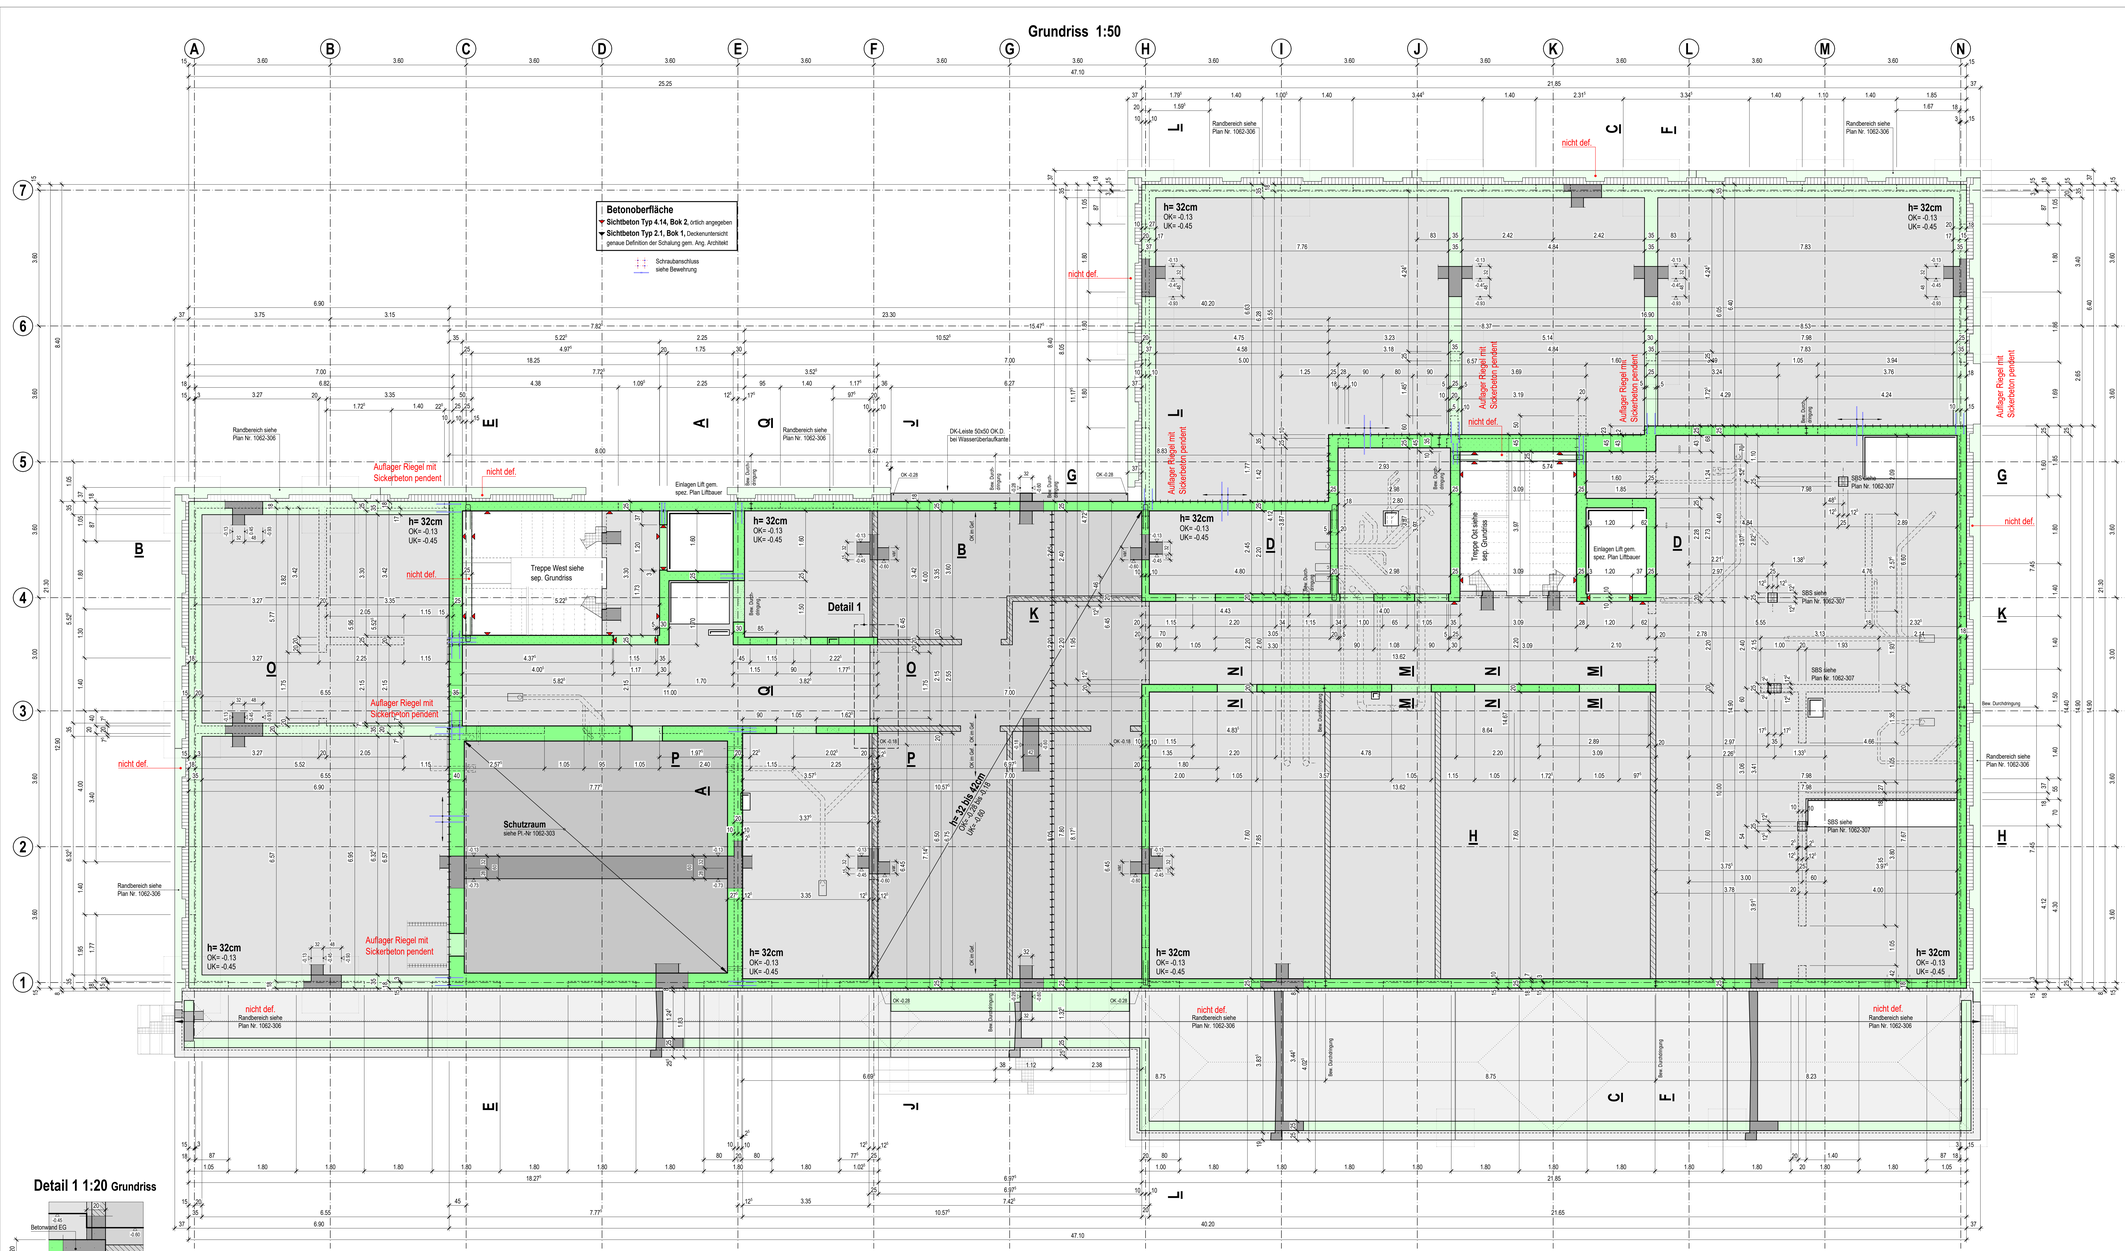

Detail 1 1:20 Grundriss

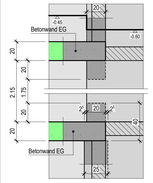

Vorschlag Arbeitsfugen Sichtbeton, 1:20 Grundriss

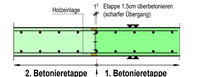

Grundriss 1:50 Treppe / Lift West

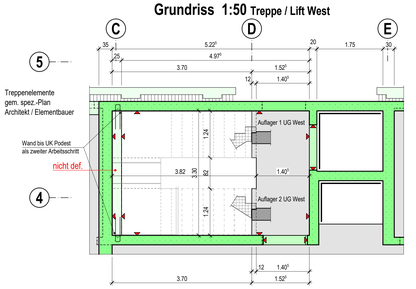

Auflager 1 UG West 1:20
Treppenlager gem Elementbauer

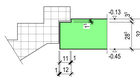

Auflager 2 UG West 1:20
Treppenlager gem Elementbauer

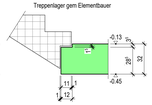

Grundriss 1:50 Treppe / Lift Ost

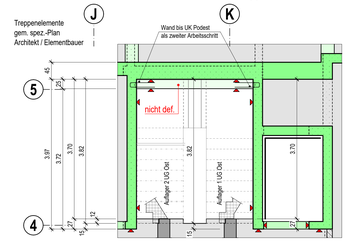

Auflager 1 UG Ost 1:20
Treppenlager gem Elementbauer

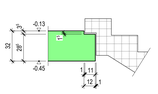

Auflager 2 UG Ost 1:20
Treppenlager gem Elementbauer

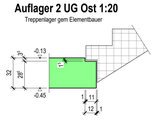

Aussparungen und Einlagen gemäss Architekten- und spez. Aussparungsplänen
SB: Sichtbeton, Schalungsbild und Bindestellen gemäss Angaben Architekt

Oberflächenbeschaffenheit: abtaloschiert, fein abgezogen, aufgeraunt nach Angabe Arch.
Alle Betonbauteile sind scharfkantig auszuführen.

Spitz- und Bohrarbeiten in Betonkonstruktionen und tragendem Mauerwerk dürfen nur mit Einwilligung des Ingenieurs ausgeführt werden.
Ausschalfristen:
- Decken: mindestens 7 Tage, anschliessend Umspriessen während 2 Monaten
- Wände: mindestens 2 Tage

Ganze Abdichtung nach Angabe Bauleitung.
-bei sämtliche erdberührten Bauteilen, Arbeitsfugen
Aussparungen und Durchdringungen

Dazugehörige Pläne:
1062-303, Schutzraum
1062-304, Grundriss
1062-305, Schnitte
1062-306, Randbereich, Einlagen
1062-307, Vorfabricierte Bützen

Dazugehörige Listen:
siehe Plan Nr. 1062-306

Legende:
- Beton
- Beton unter Bodenplatte / über Decke
- Mauerwerk tragend
- Sichtbeton Typ 4.14, Bok 2, Definition gem Ang. Architekt
- Sichtbeton Typ 2.1, Bok 1, Definition gem Ang. Architekt
- vorfabrizierte Betonbauteile

Betonqualität

Bezeichnug:	Bauteil:	Grundlegende Anforderungen
BE01	Bodenpl. EG Fundamente erdberührt Bauteile	C30/37, XC4(CH), XF1(CH) D_{max} 32, Cl 0.1, C3
BE02	Innenwände / Decken	C30/37, XC1 (CH) D_{max} 32, Cl 0.1, C3
BE03	Sichtbeton Innenfläwnde und Decken	C30/37, XC1(CH) D_{max} 32, Cl 0.1, C3 Schwind- und Kriecharm
BE04	Aussenwände <<gelbe Wannen>> erdberührt Bauteile	C30/37, XC4(CH), XF1(CH) D_{max} 32, Cl 0.1, C3 schwind- und kricharm
BE05	SCC Beton Decken, Innenwände	C30/37, XF1(CH) D_{max} 32, Cl 0.1, SF2

0m 0.5m 1m 2m 3m 4m 5m
1:50

Index	Änderungen	Datum:	Bearb.
-	zur Kontrolle	02.12.2025	RoTo

± 0.00 = 374.35 m.ü.M (OK Fertig Erdgeschoss)

Kontrollexemplar 02.12.2025

Objekt:
Ersatzneubau Wohnheim Obstgarten
Bibersteinerstrasse 54, 5022 Rombach

Bauherr:
Heilsarmee Schweiz, Laupenstr. 5
3001 Bern

Ausführungsplan
Wä. + De UG, Bodenplatte EG
Grundriss / Schnitte Schalung

Massstab: 1:50/20
Datum: 02.12.2025
Gezeichnet:
Plan Nr. **1062 - 304**
Grösse: 75 x 116
Plan: RoTo

HI HALLERINGENIEURE AG Dipl. Bauingenieure
Lindenstrasse 4 6340 Baar Tel. 041 725 32 32 e-Mail: info@halleringenieure.ch