




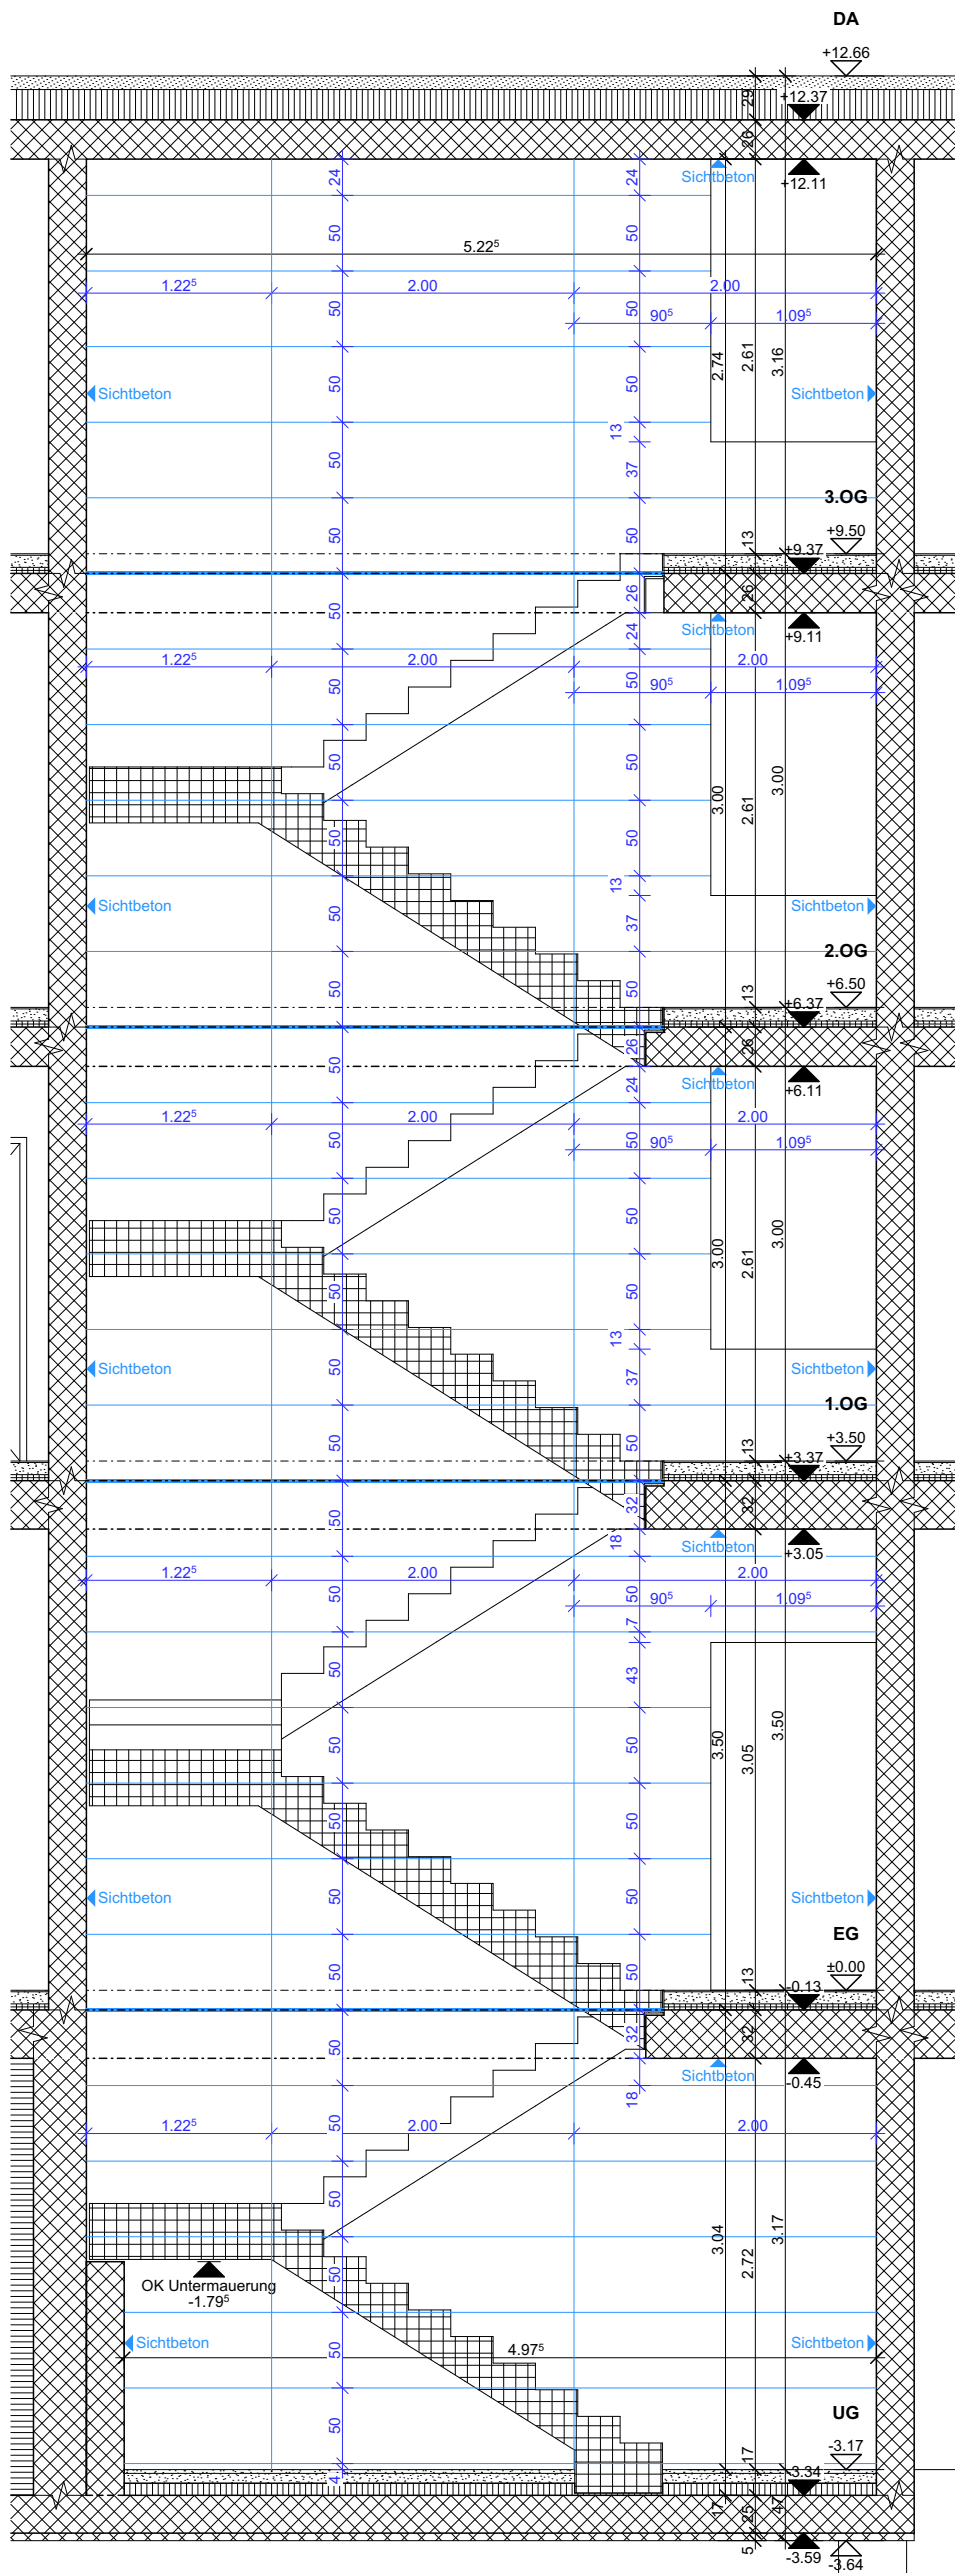


Schnitt TW 1

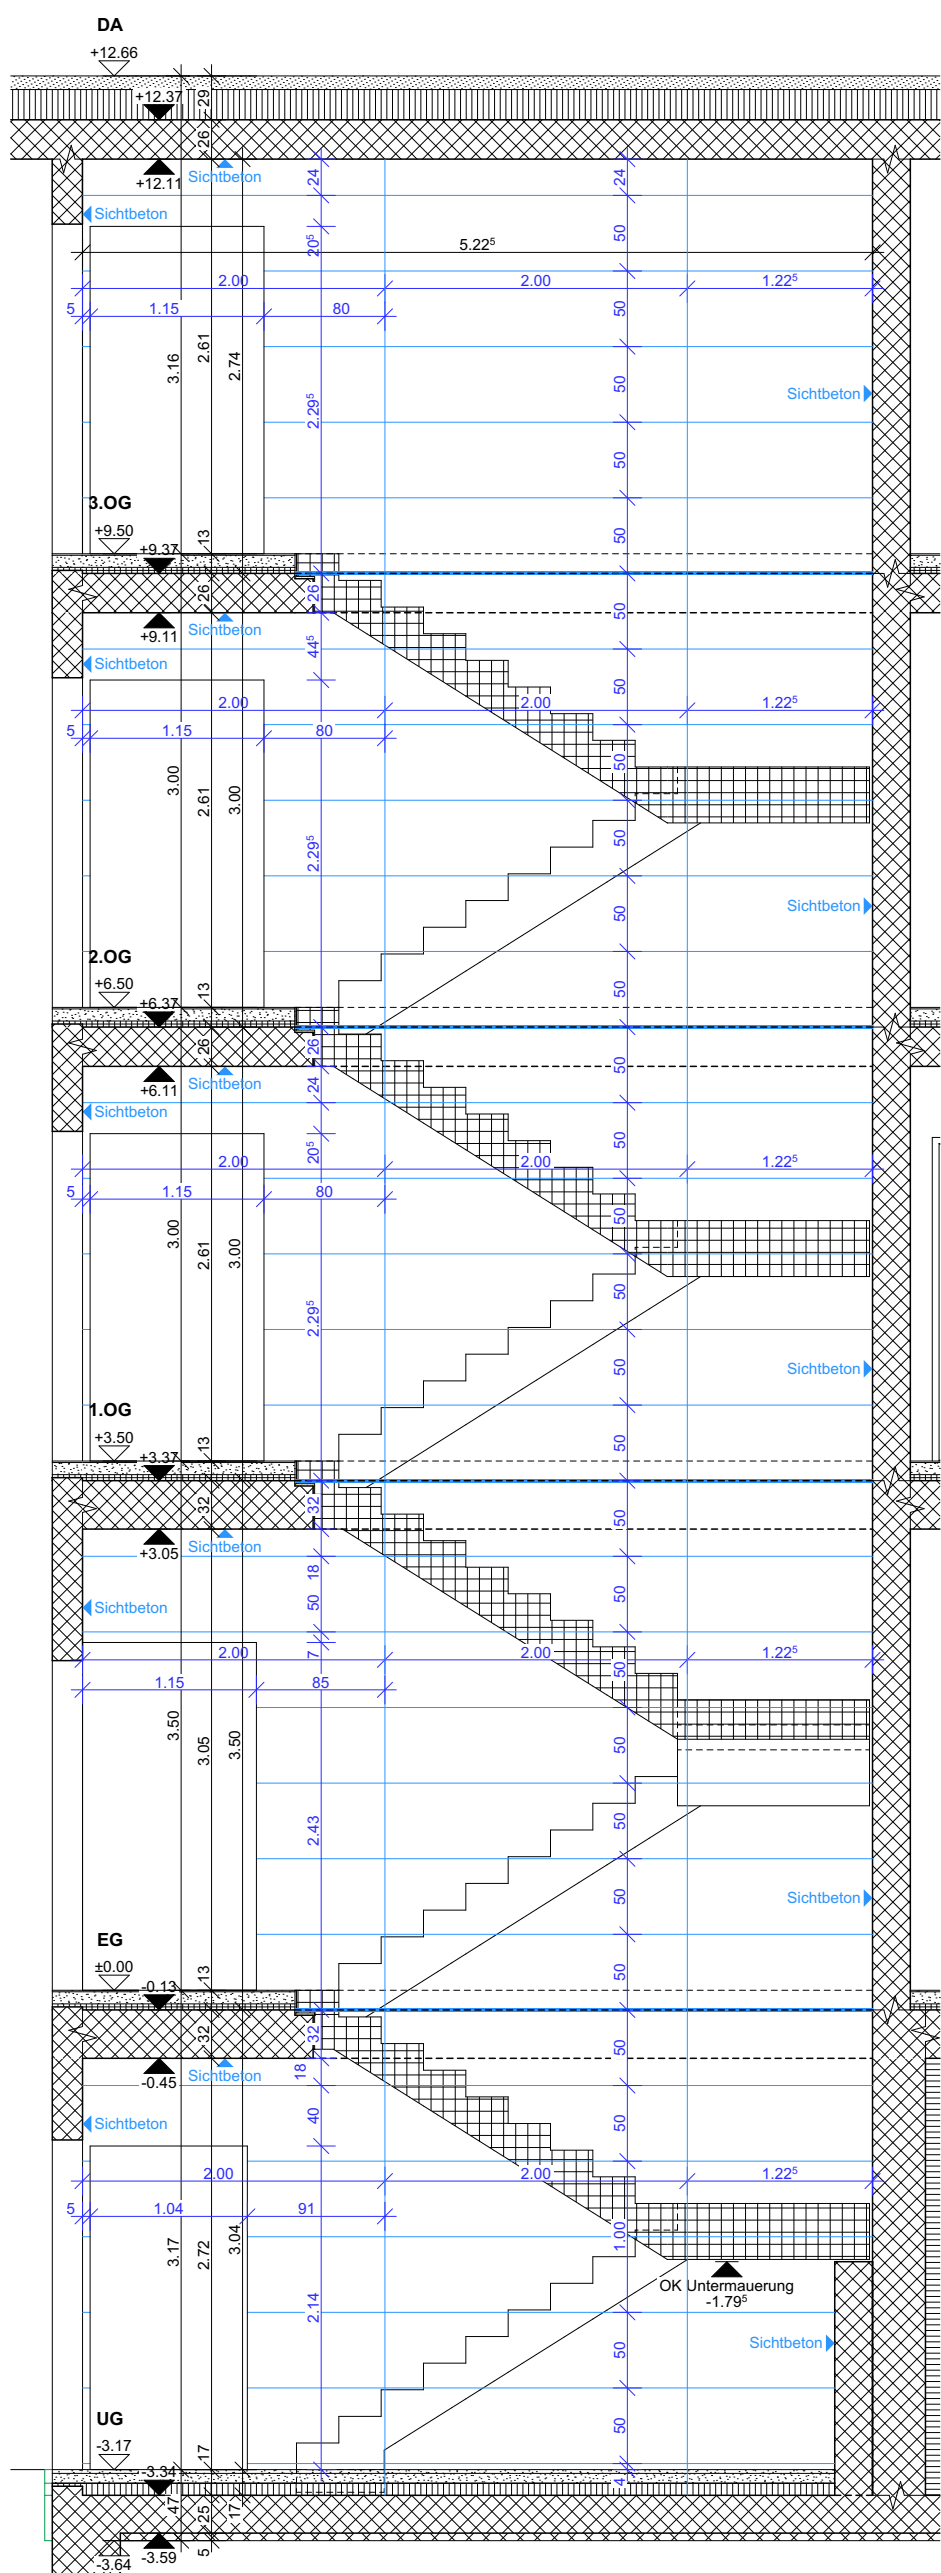

Schnitt TW 2

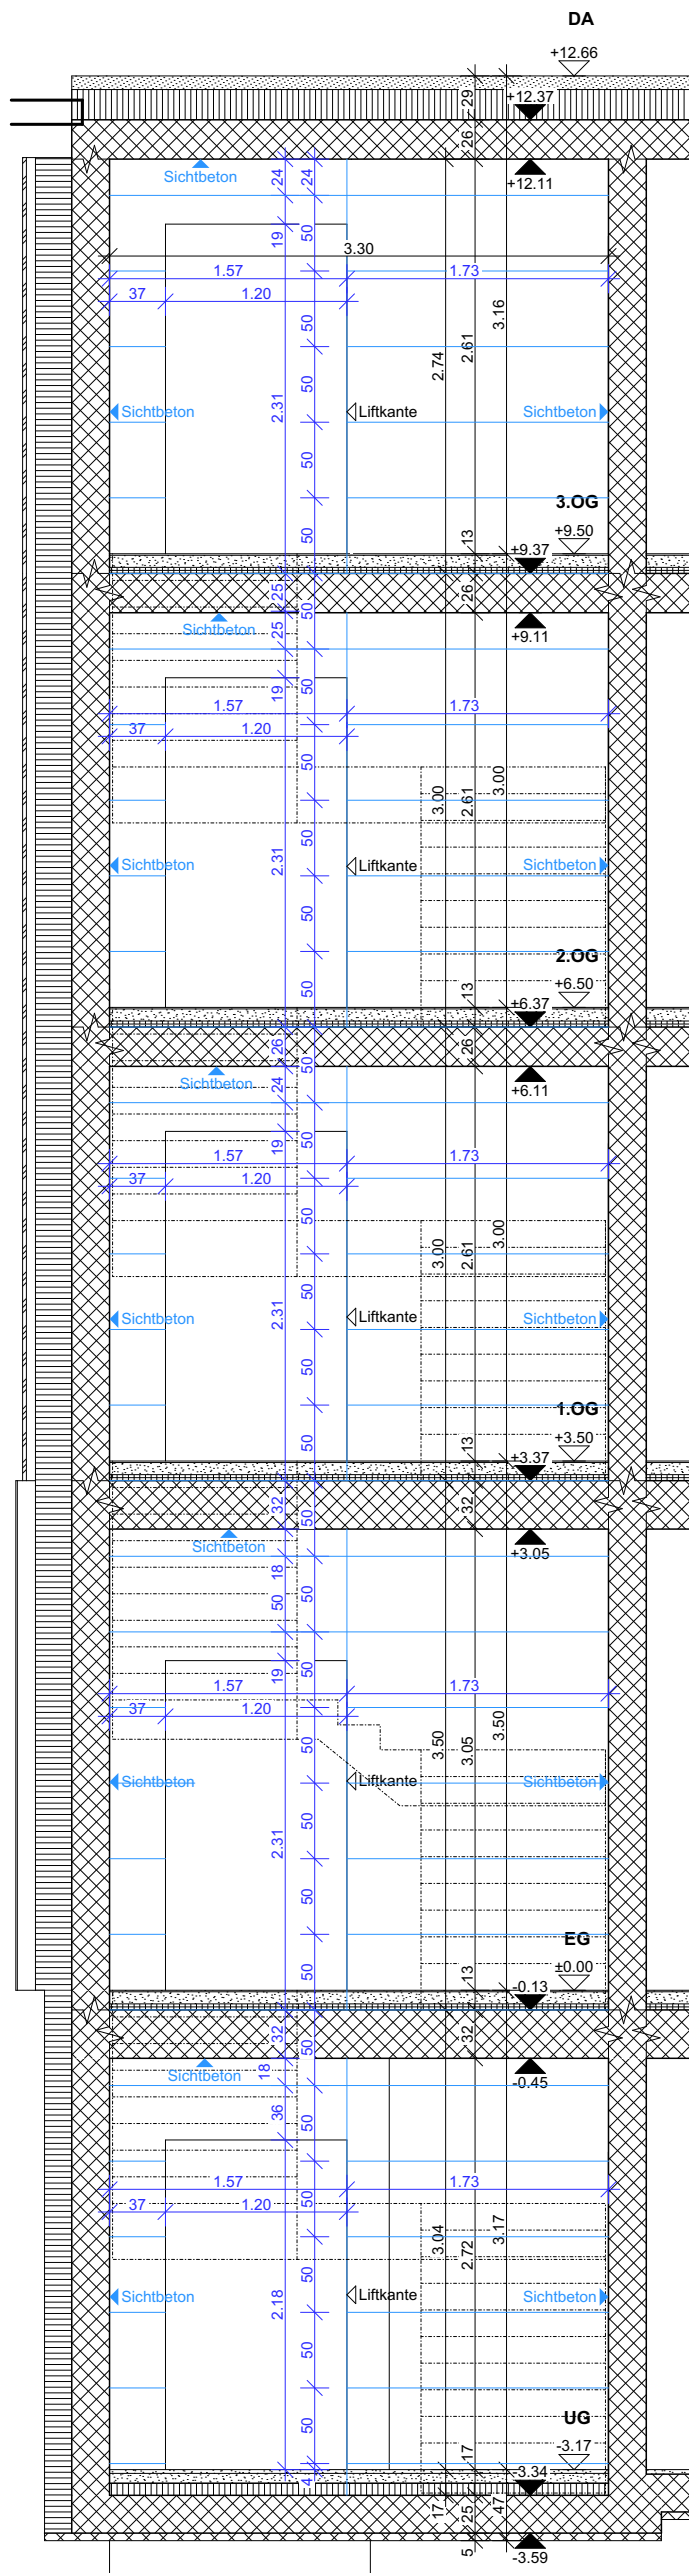

Schnitt TW 4

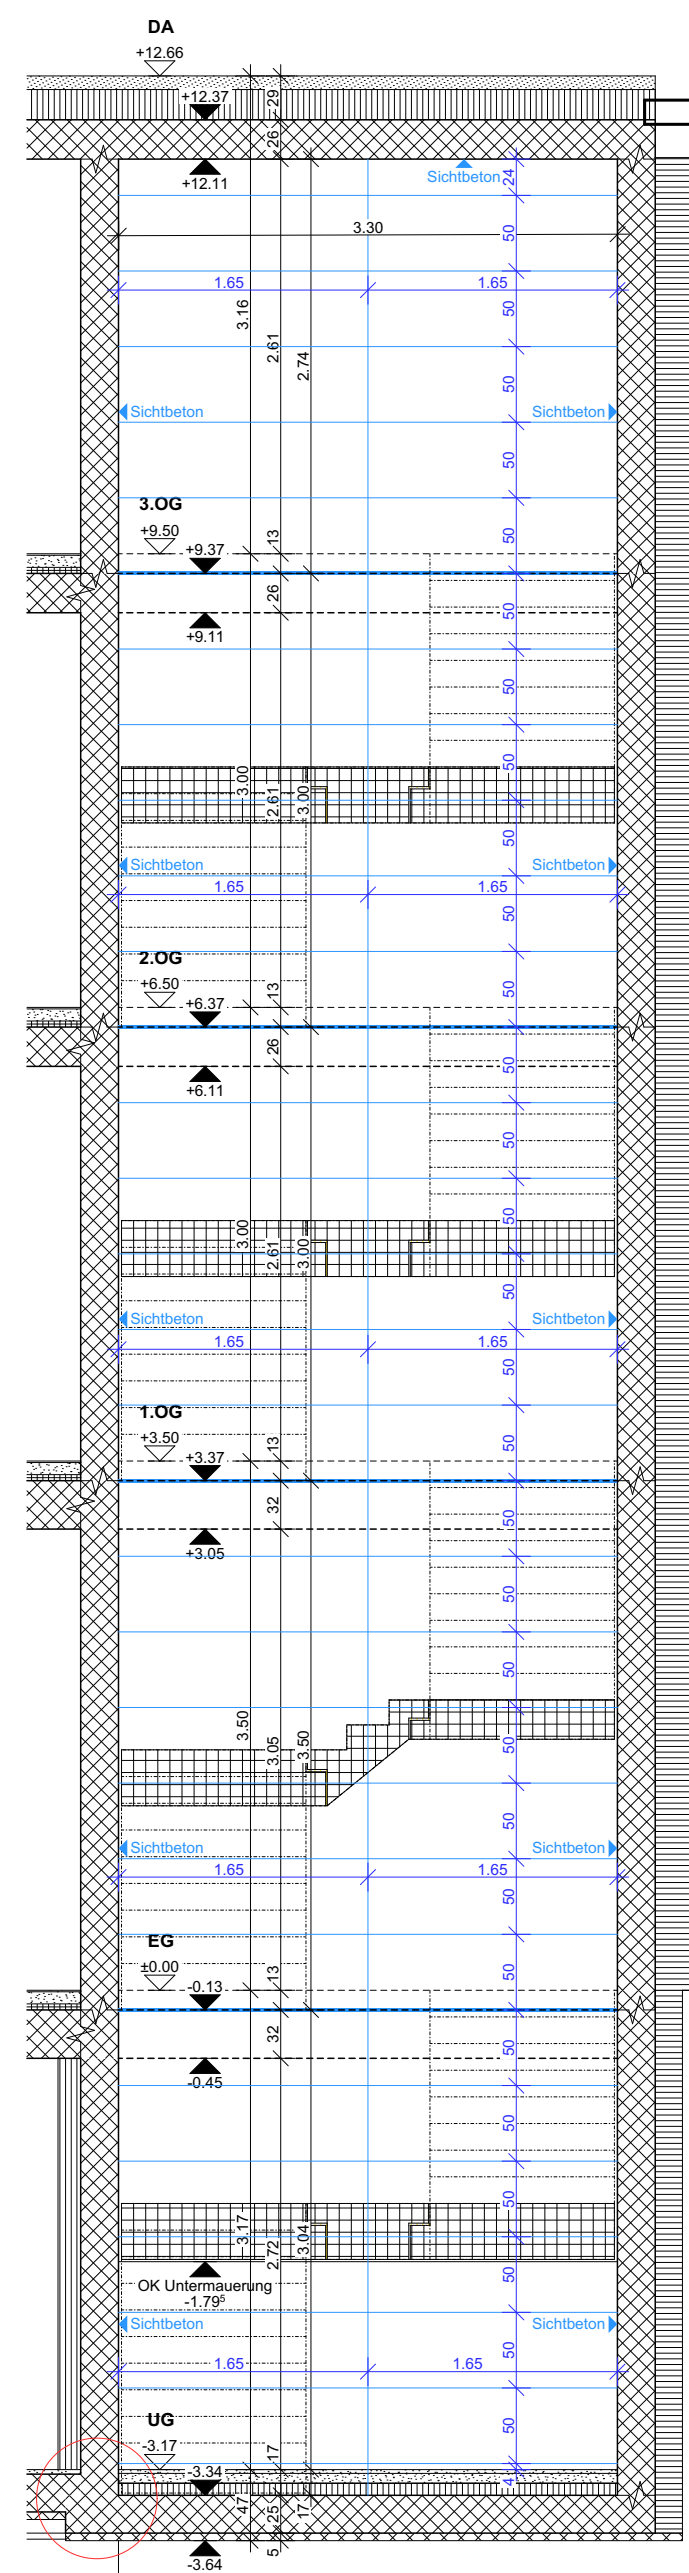


Schnitt TW 5

Alle Masse sind Rohmasse und vom Unternehmer am Bau zu kontrollieren.

Legende	
	Beton
	Backstein
	BN Thermur
	Kalksandstein
	Betonelemente
	Mörtel, Gips
	Dämmstoffe
	Naturstein
	Massivholz
	Holzwerkstoff
	Sperrschicht
	OK oberkant
	UK unterkant
	AK ausserkant
	SW OK Schwelle
	BR OK Brüstung
	ST UK Sturz roh
	FB fertig Boden
	RB roh Boden
	RD roh Decke
	im Licht
	Sichtbeton
	Rohbeton

Tür- und Fensterhöhen gemessen ab OK fertig Boden, resp. OK Fensterbank bis UK Sturz roh

	Kote OK rohe Höhe
	Kote OK fertige Höhe
	Detailbezeichnung
	Schnittbezeichnung

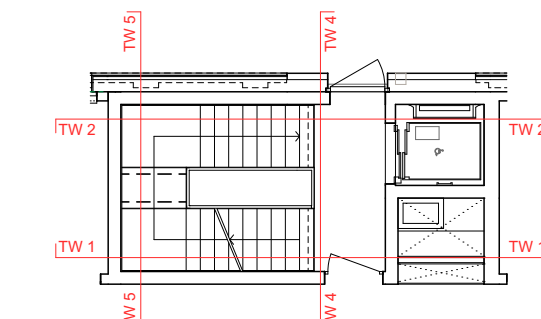

Projektkinformation
ERSATZNEUBAU WOHNHEIM OBSTGARTEN
BIBERSTEINERSTRASSE 54
CH - 5022 ROMBACH AG

Auftraggeber
Genossenschaft Heilsarmee
Laupenstrasse 5, 3001 Bern

Bauherrschaft
Frutiger AG Generalunternehmung
Bahnhofstrasse 2a, 3073 Gümligen

Grundeigentümer
Genossenschaft Heilsarmee
Laupenstrasse 5, 3001 Bern



HUSISTEIN & PARTNER AG
BÜRO FÜR ARCHITEKTUR
UND PLANUNG
SCHACHENALLEE 29 POSTFACH
5001 AARAU 1
T +41 62 823 25 27
INFO@HUSISTEIN.COM
HUSISTEIN.COM

27.11.2025 erstellt bad A2
±0.00 = 374.35

Ausführung
Planung_Skizzen
Schalungsbild TRH West
1:50

X:\01_Objekte\2508_OBGA\PO1_cad\05_Ausführung\2508_OBGA_Georeferenziert.pln

2508_OBGA_W-700.1