




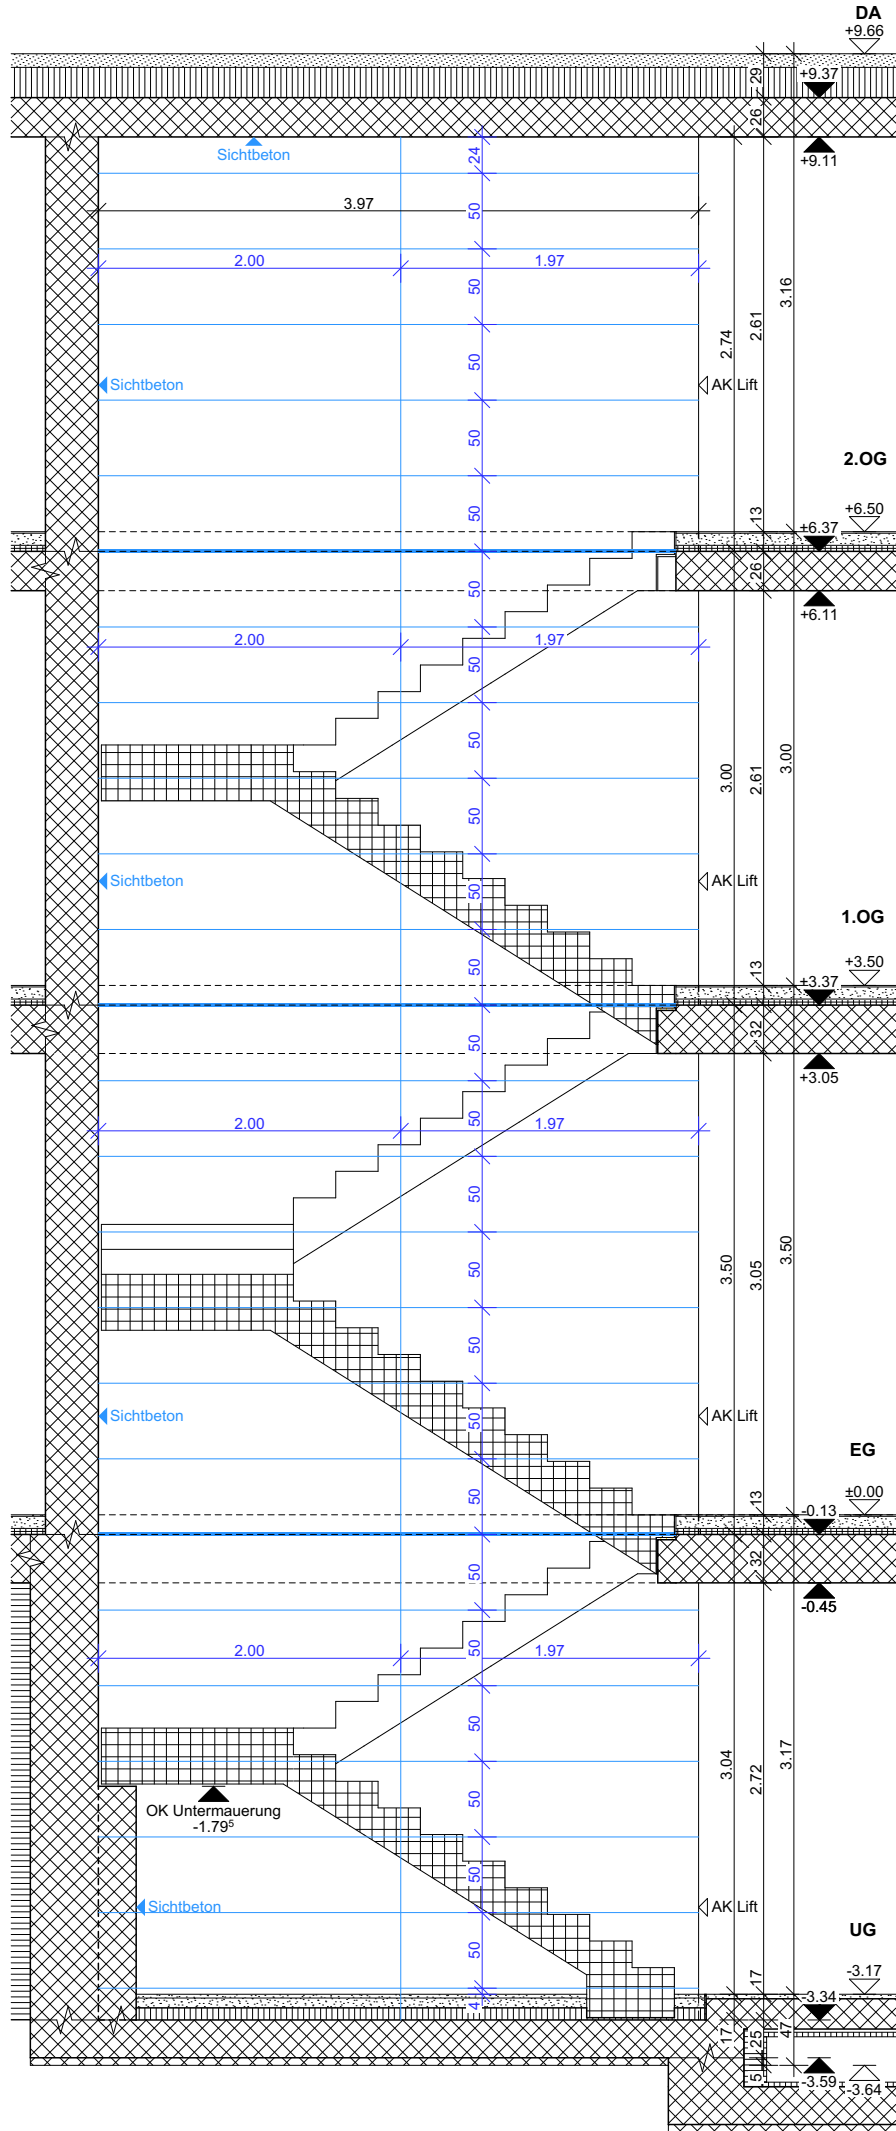


Schnitt TO 1

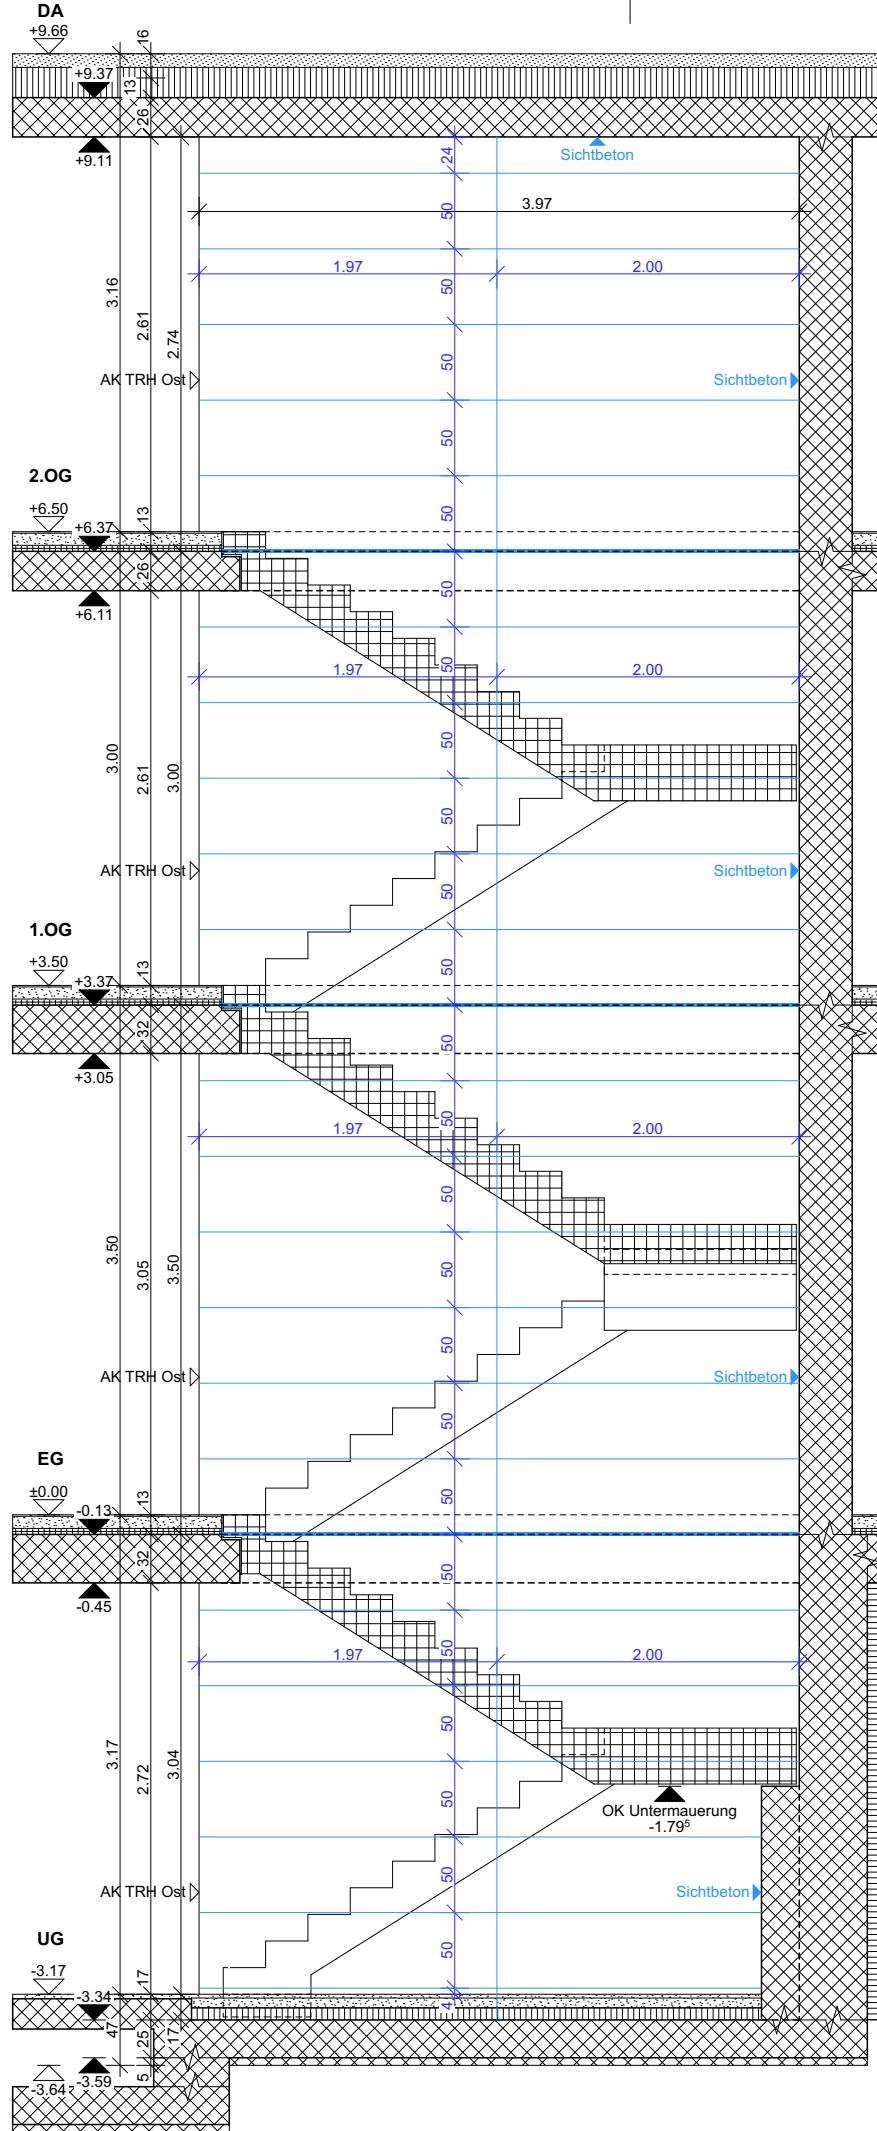

Schnitt TO 2

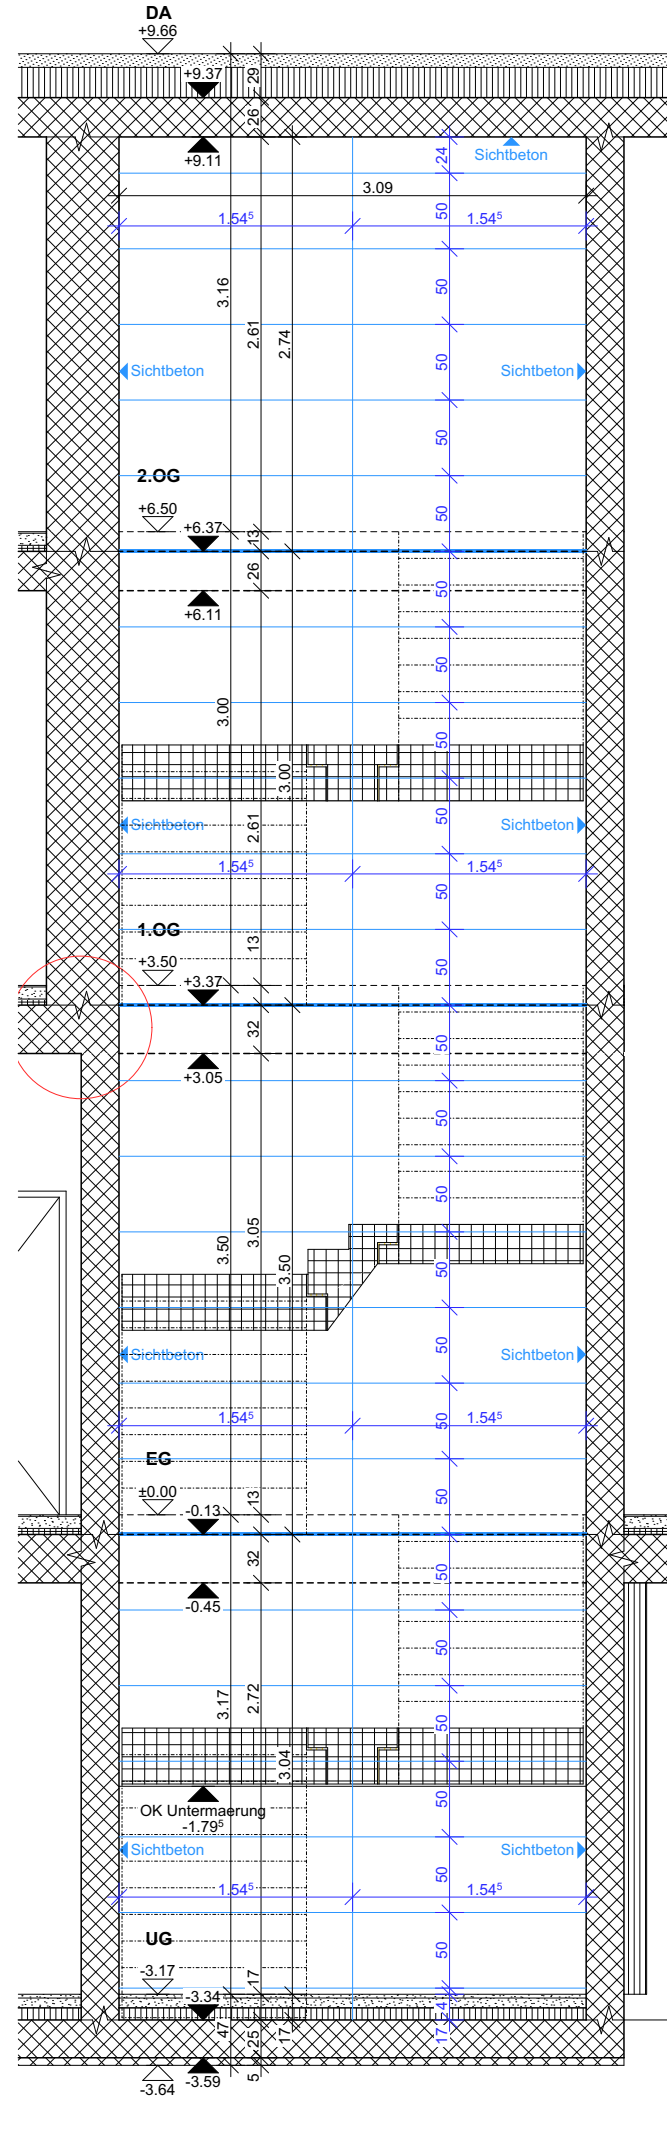

Schnitt TO 4

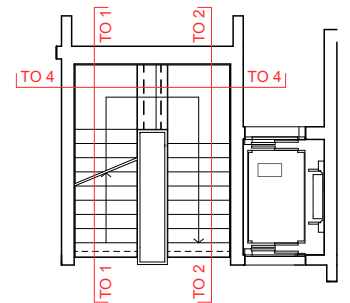

Projektinformation
ERSATZNEUBAU WOHNHEIM OBSTGARTEN
BIBERSTEINERSTRASSE 54
CH - 5022 ROMBACH AG

Auftraggeber
Genossenschaft Heilsarmee
Laupenstrasse 5, 3001 Bern

Bauherrschaft
Frutiger AG Generalunternehmung
Bahnhofstrasse 2a, 3073 G mligen

Grundeigent mer
Genossenschaft Heilsarmee
Laupenstrasse 5, 3001 Bern



HUSISTEIN & PARTNER AG
B RO F R ARCHITEKTUR
UND PLANUNG
SCHACHENALLEE 29 POSTFACH
5001 AARAU 1
T +41 62 823 25 27
INFO@HUSISTEIN.COM
HUSISTEIN.COM

27.11.2025 erstellt bad A3

 0.00 = 374.35

Ausf hrung
Planung_Skizzen
Schalungsbild TRH Ost
1:50

X:\01_Objekte\2508_OBGA\IP01_cad\05_Ausf hrung\2508_OBGA Georeferenziert.pln

2508_OBGA_W-700.2