

Parzelle 8005
40.00-OK-FB: Erdgeschoss Haus A = 529.50 m ü.M.
Koordinaten Fixpunkt 6404 = 2895'509 / 1235'317

N

OK

UK

R

FB

ST

BR

SW

RH

M

MFB

Text

Text

oberkant

unterkant

roher Boden

fertiger Boden

Brüstung

Schwelle

Raumhöhe fertig (OK FB bis UK RD)

Motorisiert

Fensterbank Metall

HLKS-Planung

Elektroplanung

PLANREVISION

DATUM

Stahlbeton

Wärmedämmung

Holzwerkstoff

Massivholz

Kunststein

Leichtbauwand durch Gipsr



Vorwände z.B. GIS oder Gipservorwände

Alle Masse sind Rohmasse. Fertignasse sind mit "Fertig" oder "F" bezeichnet. Sämtliche Masse müssen vom Unternehmer geprüft und am Bau kontrolliert werden. Allfällige Unstimmigkeiten sind dem Architekten / der Bauleitung umgehend mitzuteilen.

Türhöhen beziehen sich auf OK fertiger Boden oder OK fertig Schwelle bis UK roher Sturz.


Fensterhöhen beziehen sich auf OK fertig Fensterbank bis UK fertig Sturz.

Änderungsindex

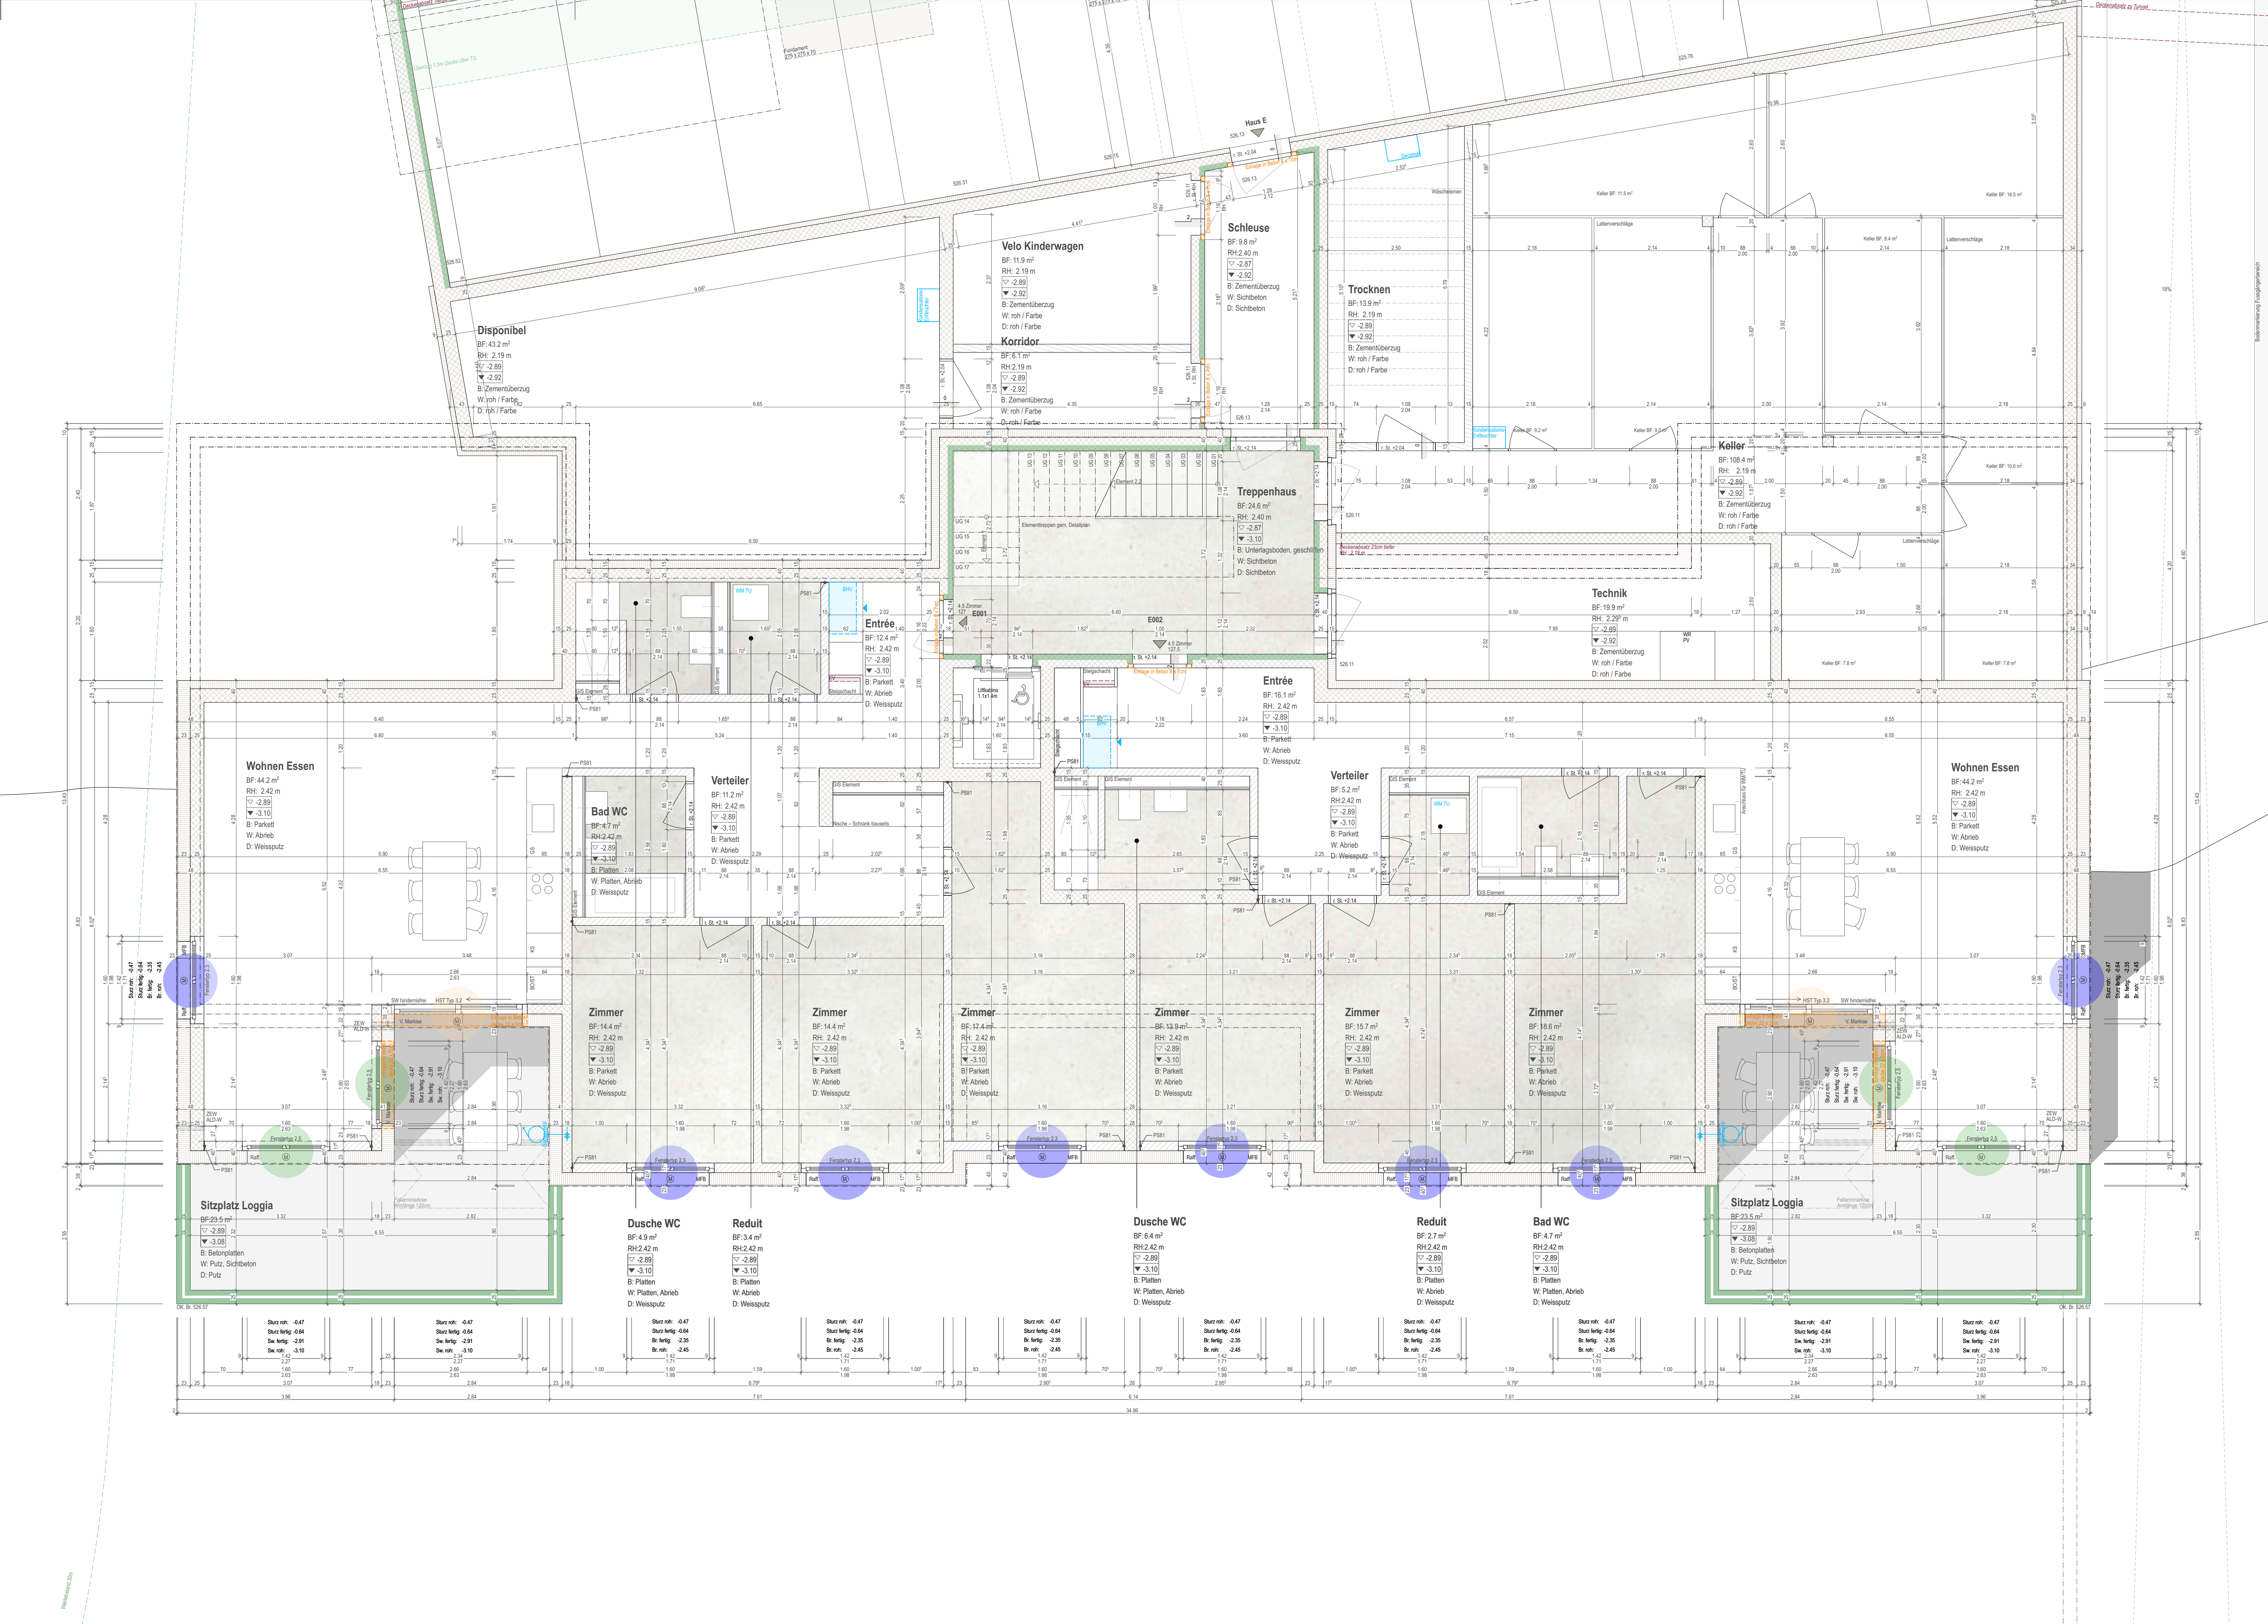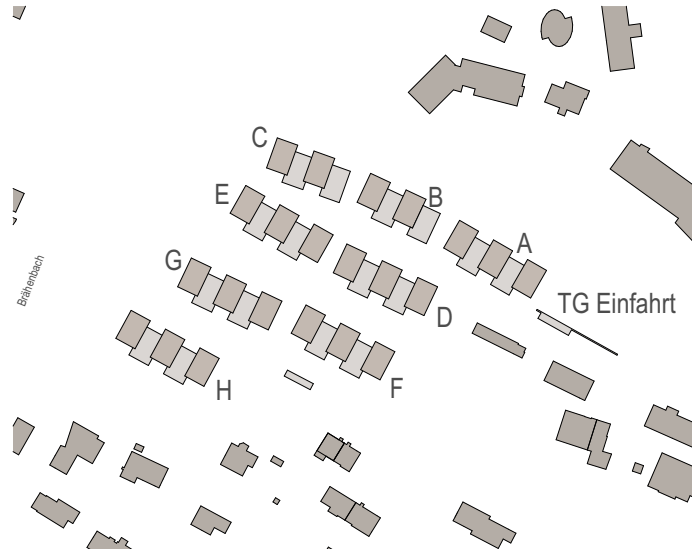

Parzelle 800:

±0.00=OK.FB. Erdgeschoss Haus A = 529.50 m.ü.M.
Koordinaten Fixpunkt 6404 = 2°6'55"509 / 1°23'5"317

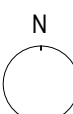


Legende Abkürzungen

OK	:	oberkant
UK	:	unterkant
R	:	roh
F	:	fertig
RB	:	roher Boden
FB	:	fertiger Boden
ST	:	Sturz
BR	:	Breislung
SW	:	Schwelle
RH	:	Raumhöhe fertig (OK FB bis UK RD)
M	:	Motorisiert
MFb	:	Fensterbank Metall
Text	:	HLKS-Planung
Text	:	Elektroplanung


 PLANREVISION
 DATUM


Änderungsindex

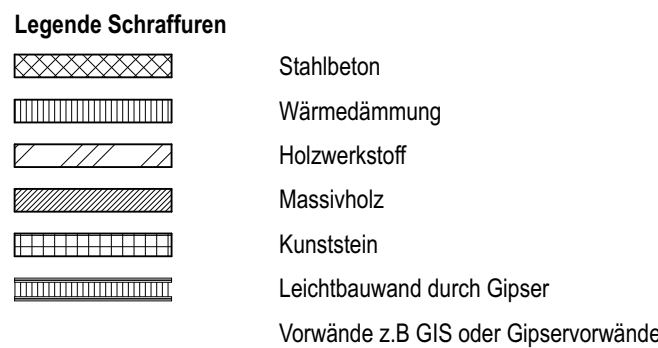

Allgemeine Informationen


Alle Masse sind Rohmasse, Fertigmasse sind mit "Fertig" oder "F" bezeichnet. Sämtliche Masse müssen vom Unternehmer geprüft und am Bau kontrolliert werden. Allfällige Unstimmigkeiten sind dem Architekten / der Bauleitung umgehend mitzuteilen.

Türhöhen beziehen sich auf OK fertig Boden oder OK fertig Schwelle bis UK roher Sturz.
Fensterhöhen beziehen sich auf OK fertig Fensterbank bis UK fertig Sturz

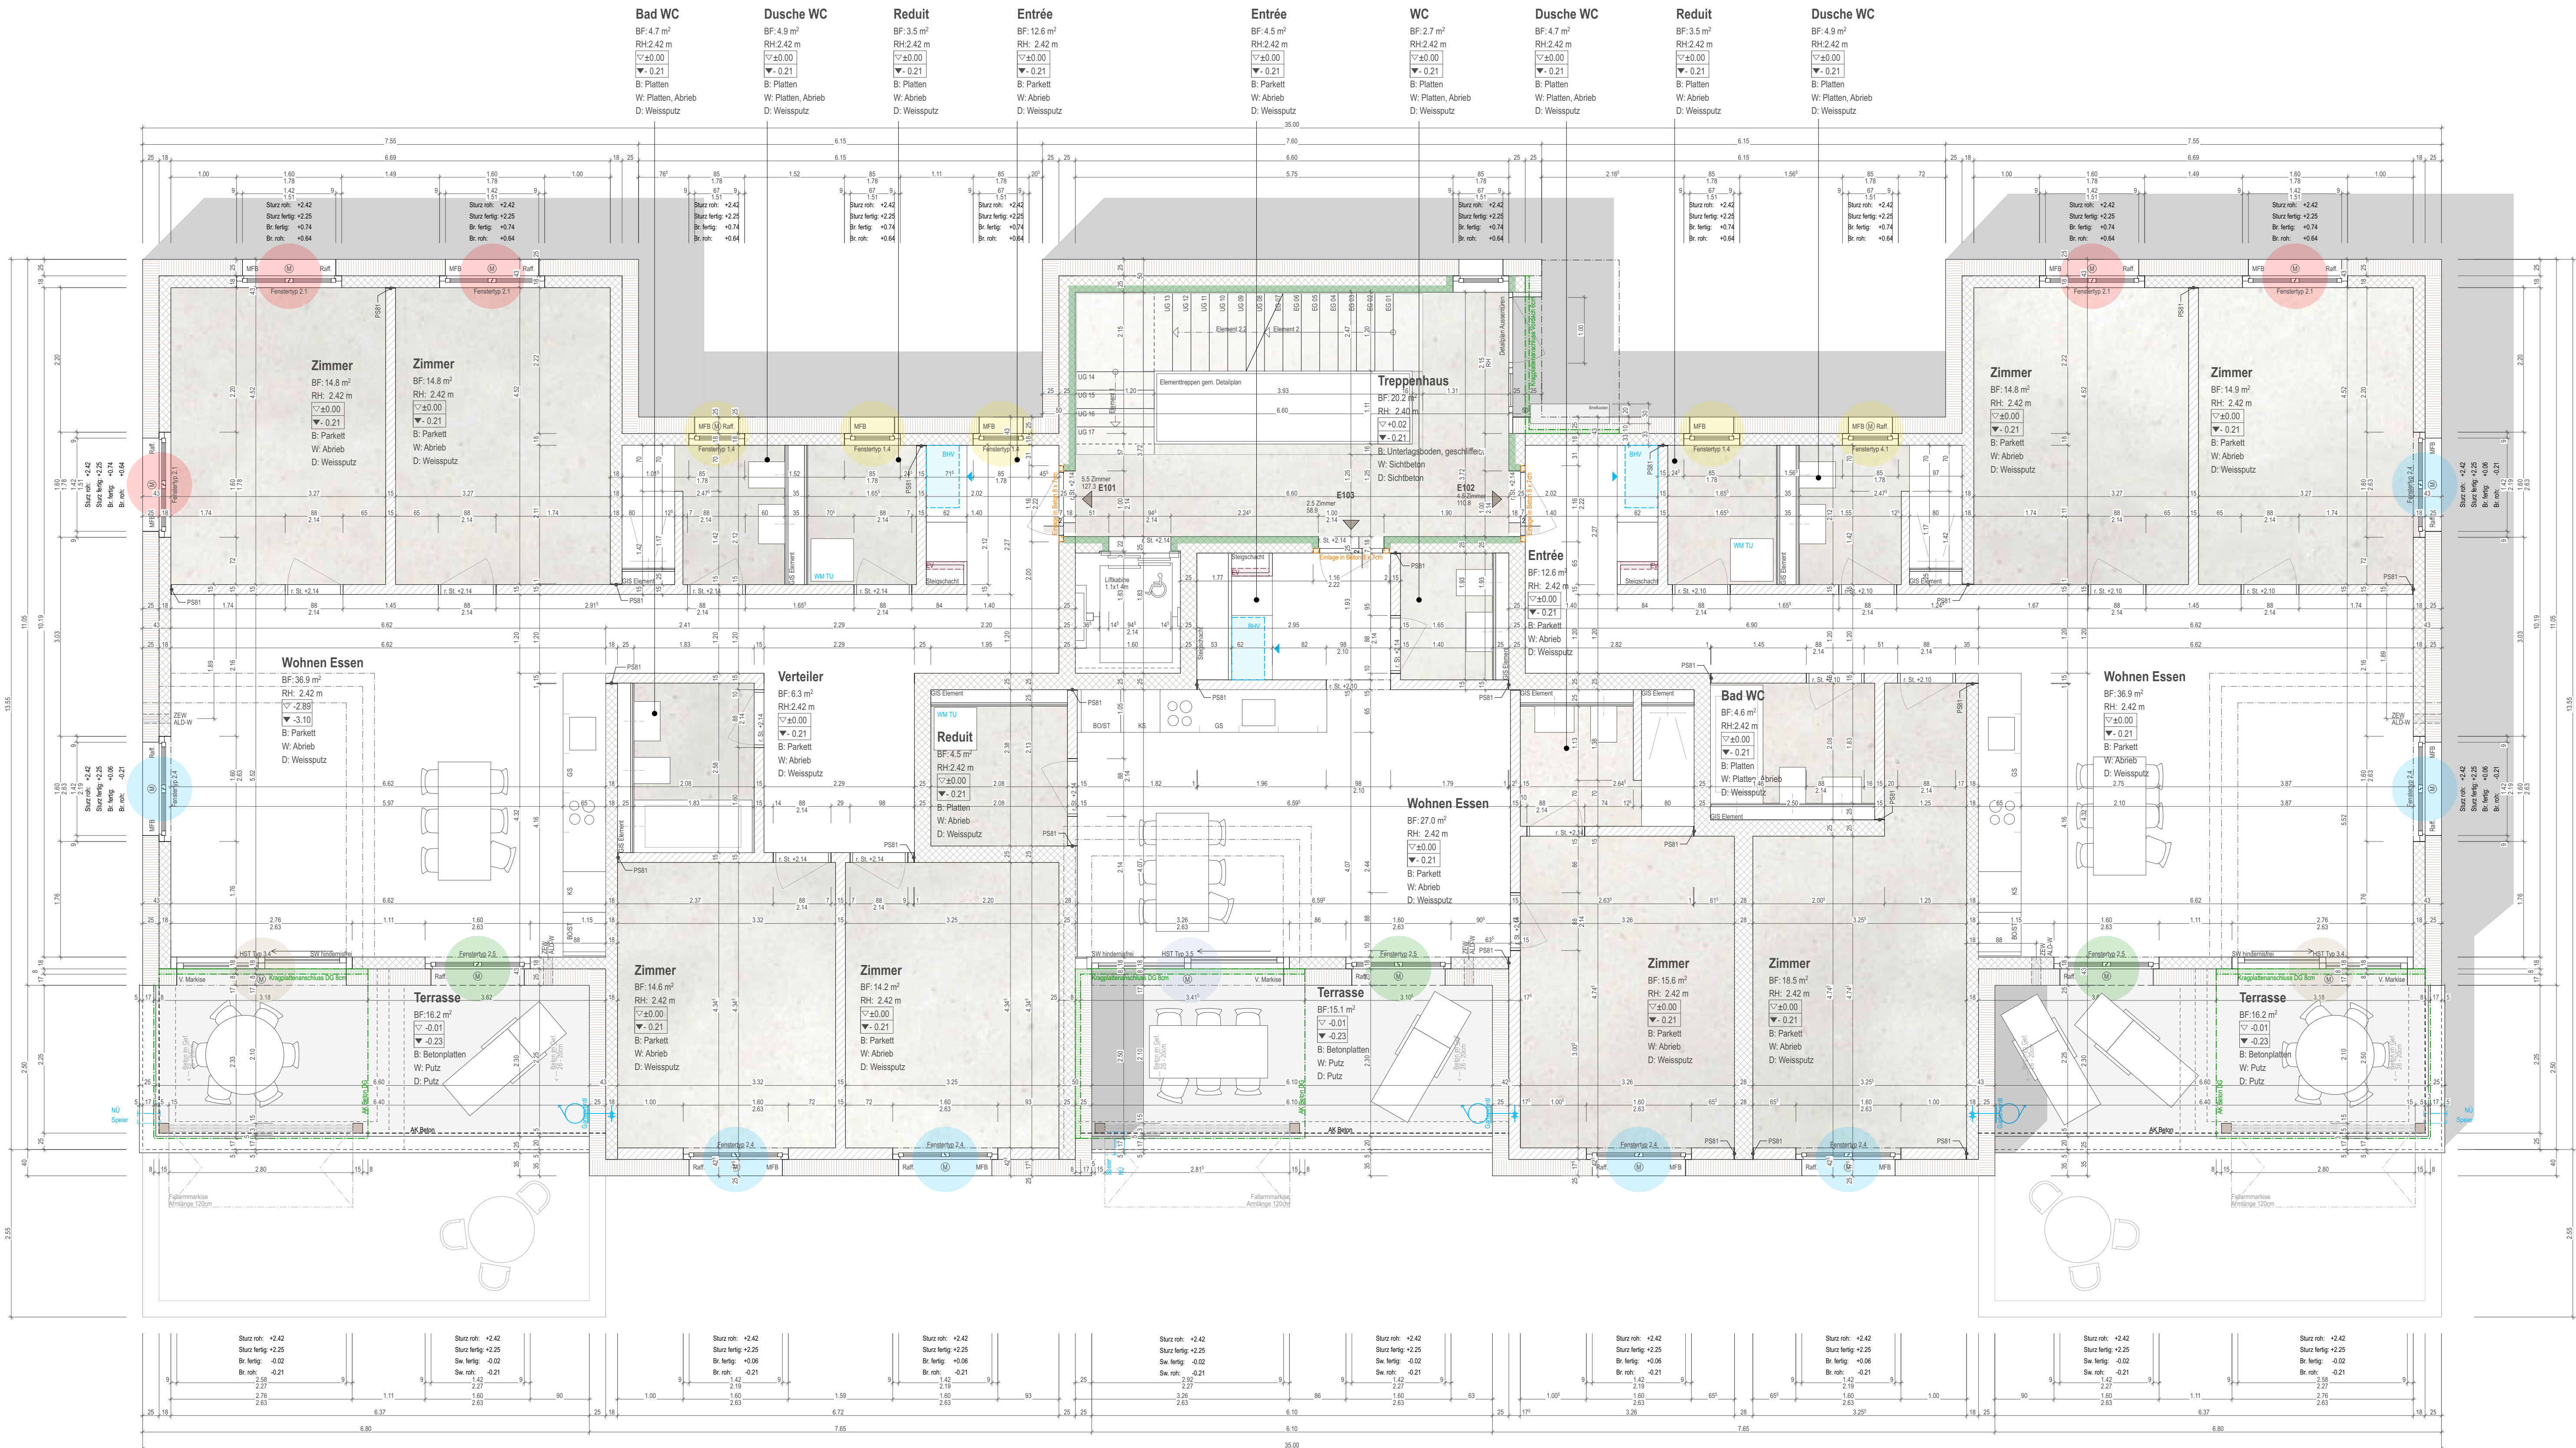

Parzelle 800:

±0.00=OK.FB. Erdgeschoss Haus A = 529.50 m.ü.M.
Koordinaten Fixpunkt 6404 = 2°69'509 / 1°235'317

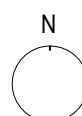


Legende Abkürzungen


OK	:	oberkant
UK	:	unterkant
R	:	roh
F	:	fertig
RB	:	roher Boden
FB	:	fertiger Boden
ST	:	Sturz
BR	:	Brüstung
SW	:	Schwelle
RH	:	Raumhöhe fertig (OK FB bis UK RD)
M	:	Motorisiert
MFB	:	Fensterbank Metall
Text ...	:	HLKS-Planung
Text ...	:	Elektroplanung


PLANREVISION
DATUM

Änderungsindex

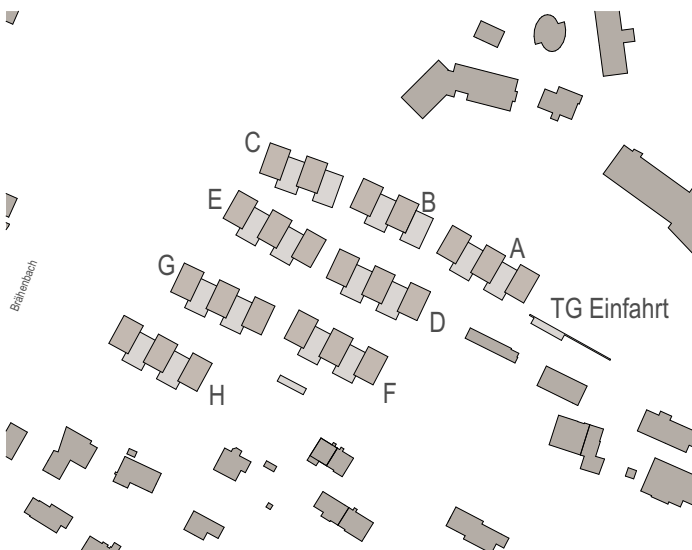

Legende Schraffuren

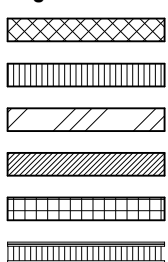

- Stahlbeton
- Wärmedämmung
- Holzwerkstoff
- Massivholz
- Kunststein
- Leichtbauwand durch Gips
- Vorwände z.B. GIS oder Gipservorwände

Allgemeine Informationen

Alle Masse sind Rohmasse, Fertigmasse sind mit "Fertig" oder "F" bezeichnet. Sämtliche Masse müssen vom Unternehmer geprüft und am Bau kontrolliert werden. Allfällige Unstimmigkeiten sind dem Architekten / der Bauleitung umgehend mitzuteilen.

Türhöhen beziehen sich auf OK fertig Boden oder OK fertig Schwelle bis UK roher Sturz.
Fensterhöhen beziehen sich auf OK fertig Fensterbank bis UK fertig Sturz.

