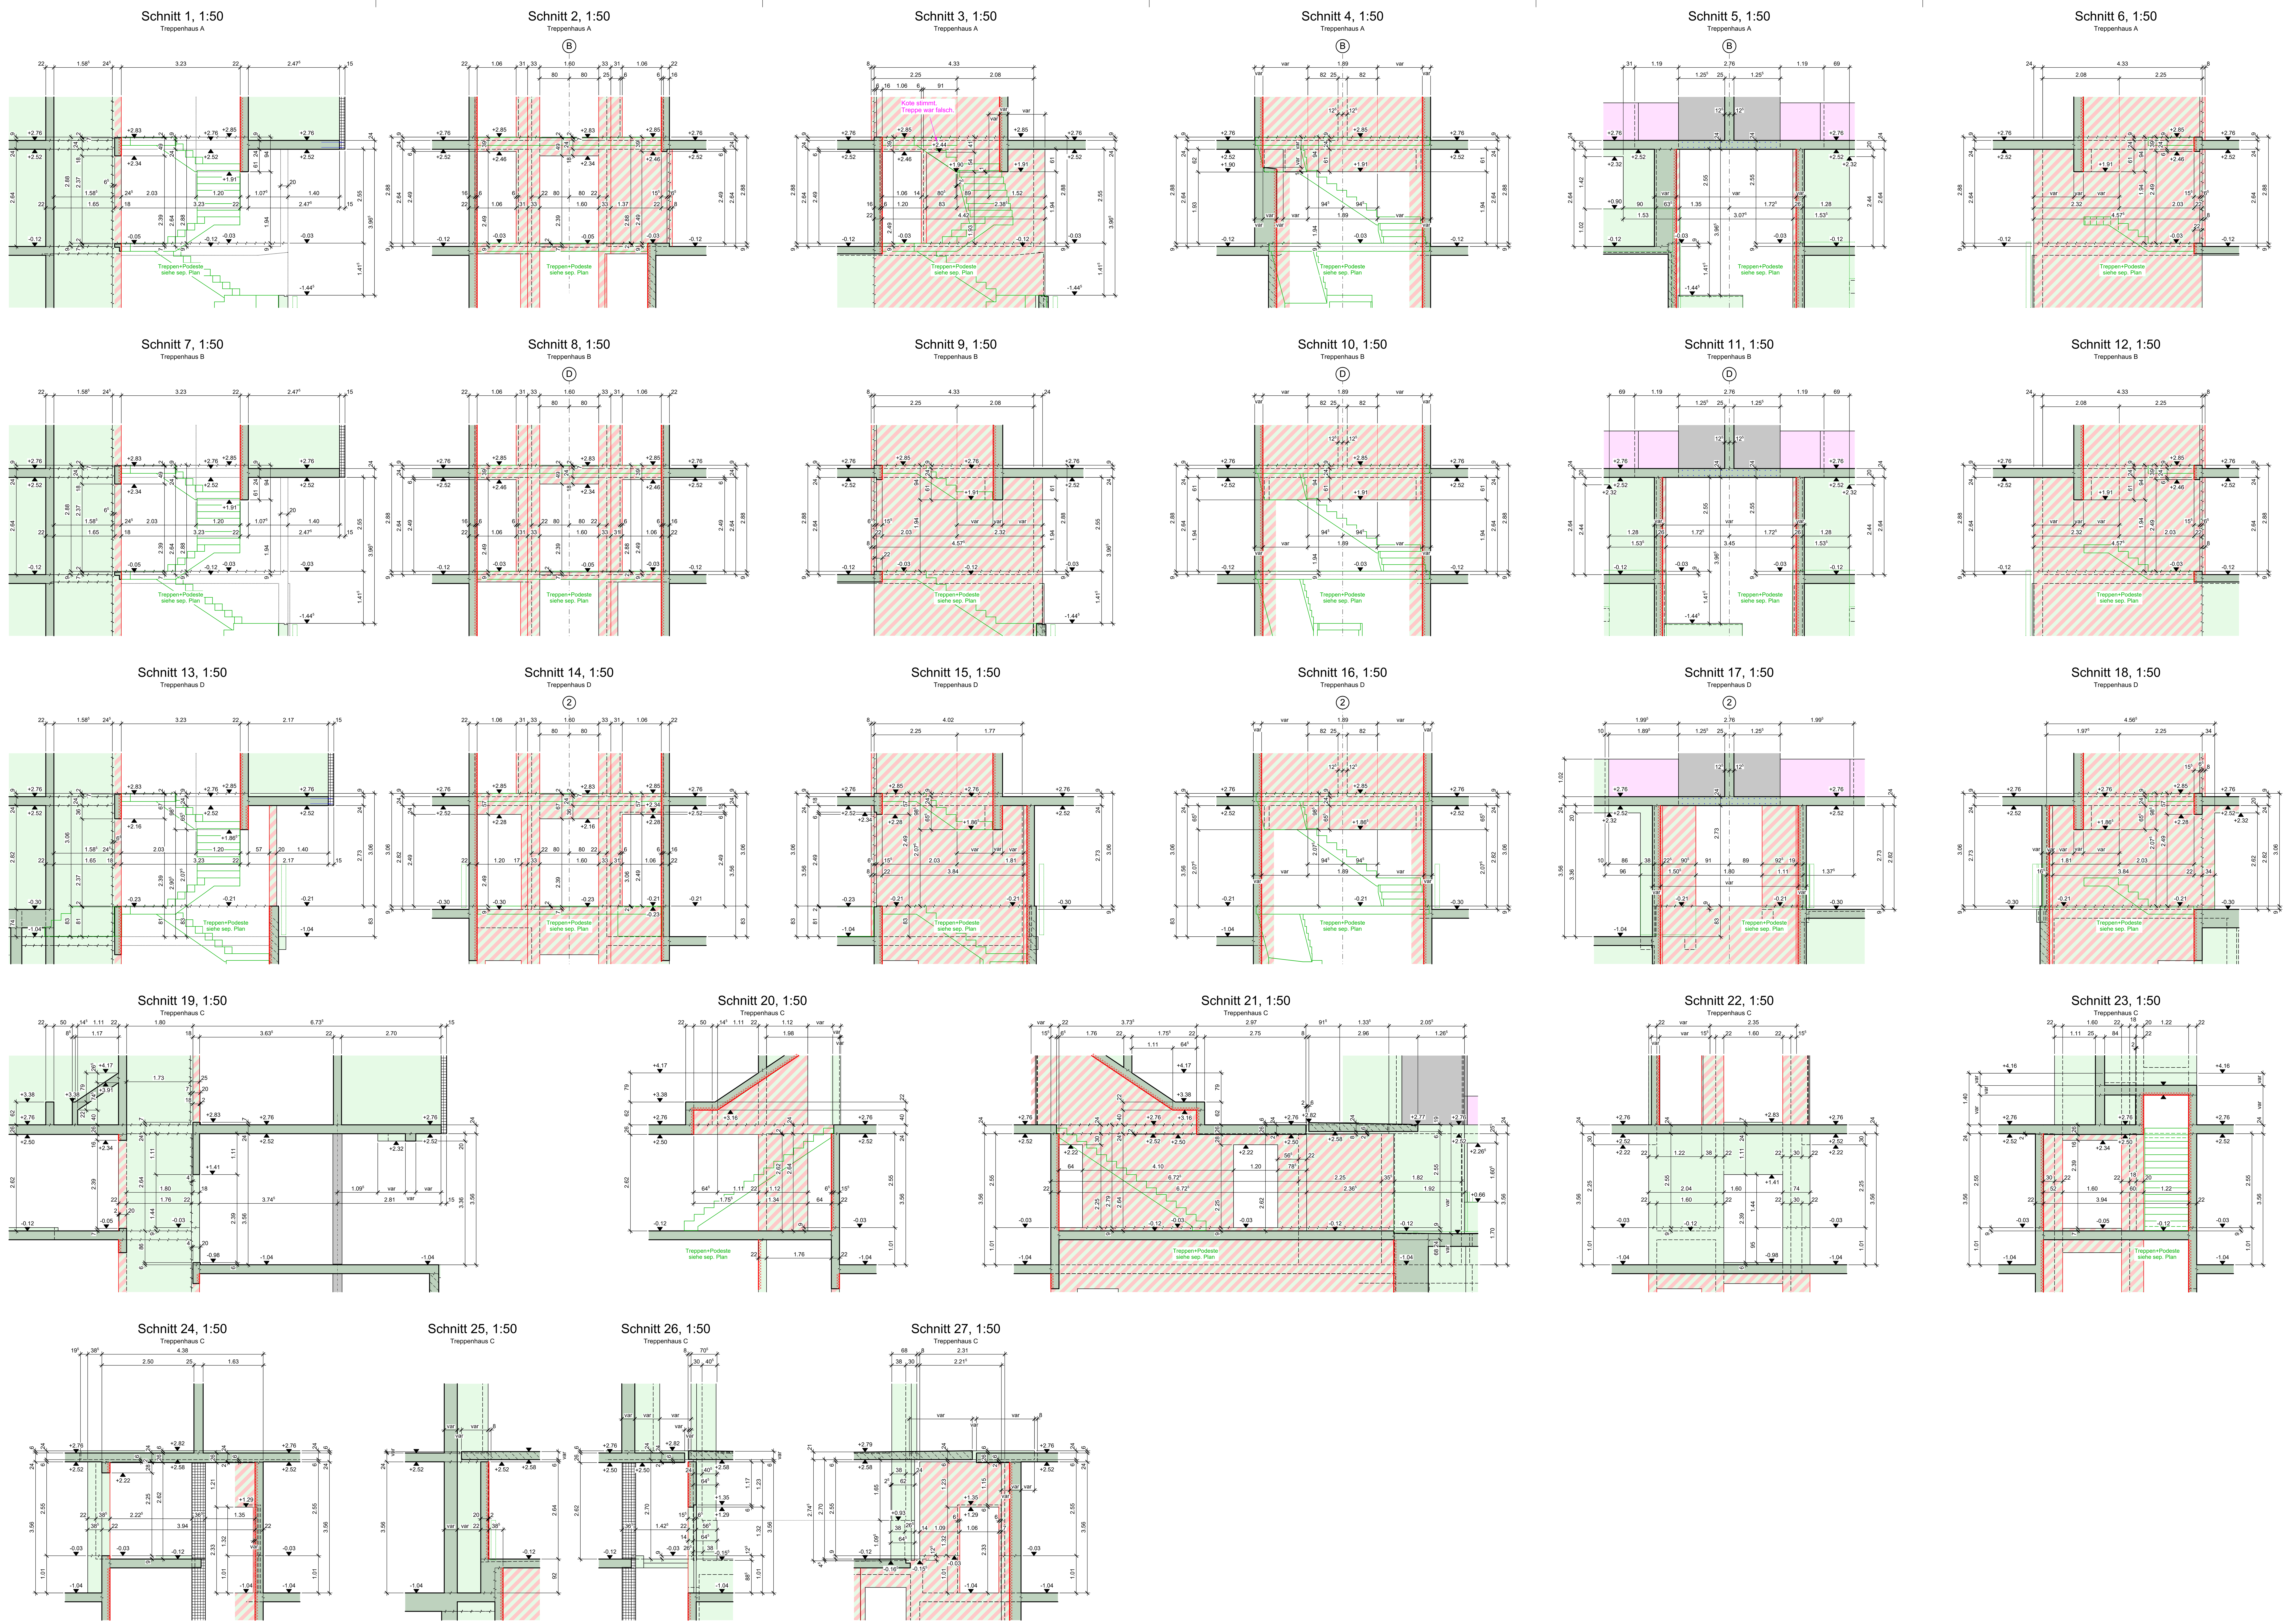

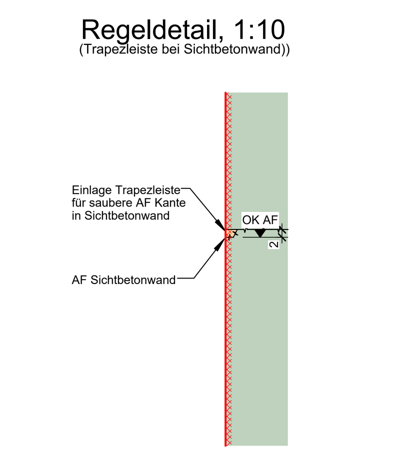

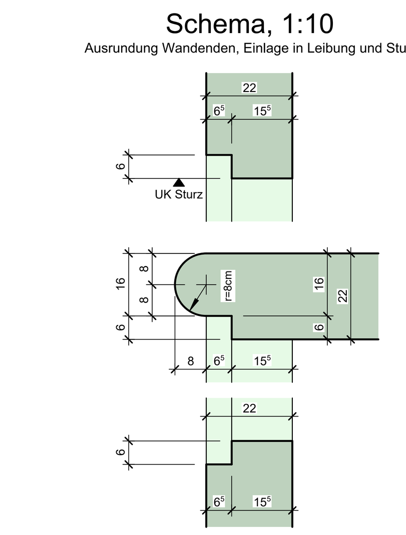

LEGENDE

Baustoffe:

Magerbeton	Sauberkeitsschicht (NPK 0), RC-M40, X0, D_{max}16, (erdfeucht), (CEM II/B oder CEM III/B oder ZN/D, 150 kg/m³)
Beton WD (BE 1)	Bodenplatte und Aussenwände (Weisse Wanne), Balkonplatten, Stützmauerwände NPK C, C30/37, RC-C25 E30, XC4, XF1, D_{max}32, Cl 0.20, C3 oder F4, E_{rcm} ≥ 30 kN/mm², (CEM II/B oder CEM III/B, 300 kg/m³)
Beton (BE 2)	Wände, Brüstungen und Decken im Innenbereich, Erdbebenwände, Überbeton Filigranplatten, Stützmauerfundamente C30/37, RC-C25 E30, XC2, D_{max}32, Cl 0.20, C3 oder F4, E_{rcm} ≥ 30 kN/mm², (CEM II/B oder CEM III/B oder ZN/D, 280 kg/m³)
Beton (BE 3)	Dünne oder hochbewehrte Bauteile im Innenbereich (Wände 20 cm) C30/37, RC-C25 E30, XC2, D_{max}16, Cl 0.20, F4, (CEM II/B oder CEM III/B oder ZN/D, 280 kg/m³)
Beton SCC (BE 4)	Dünne oder hochbewehrte Bauteile im Innenbereich (Brüstungen 15/20 cm) C30/37, XC2, D_{max}16, Cl 0.10, SF2, (CEM II/B oder CEM III/B oder ZN/D, 280 kg/m³)
Beton WD (BE 5)	Aussen- und Innenwände Einstellhalle (Einfahrt, einhpt. Wand Friesstr.) NPK F, C30/37, XC4, XD3, XF2, D_{max}32, Cl 0.10, C3 oder F4, FT, LP ≥ 3 %, (CEM II/B oder CEM III/B, 320 kg/m³)
Beton WD (BE 6)	Rampe und Bodenplatte Einstellhalle NPK G, C30/37, XC4, XD3, XF4 D_{max}32, Cl 0.10, C3 oder F4, FT, LP ≥ 3 %, (CEM II/B oder CEM III/B, 320 kg/m³)
Beton (BE 7)	Füllbeton, untergeordnete Bauteile C25/30, RC-C25 E25, XC2, D_{max}32, Cl 0.20, C3 oder F4, E_{rcm} ≥ 25 kN/mm², (CEM II/B oder CEM III/B oder ZN/D, 280 kg/m³)
Beton SCC (BE 8)	Ortbetonsockel NPK F, C30/37, XC4, XD3, XF2, D_{max}16, Cl 0.10, SF2, (CEM II/B oder CEM III/B, 320 kg/m³)

- Betonfertigteil tragend (vorfabriziert)
- Betonfertigteil nichttragend (vorfabriziert)
- Mauerwerk Kalksandstein tragend
- Mauerwerk Backstein tragend
- Beton Ansicht
- Sichtbeton Ansicht
- Betonfertigteile Ansicht tragend (vorfabriziert)
- Betonfertigteile Ansicht nichttragend (vorfabriziert)
- Mauerwerk Kalksandstein tragend Ansicht
- Mauerwerk Backstein tragend Ansicht
- Beton im nächsten Geschoss (für Anschlussbewehrung)
- Mauerwerk tragend im nächsten Geschoss
- Sichtbeton, Monobeton
  Schalungsbild, Beschaffenheit, Fugenteilung nach Angaben des Architekten
  oder nach Angaben im Schalungsplan
- Arbeitsfuge

Abkürzungen:

UK = Unterkante
OK = Oberkante
Br. = Brüstung
Bd. = Bord
St. = Sturz
AF = Arbeitsfuge
DF = Dehn-/Dilatationsfuge
FB = Fugenband
BD = Bodendurchbruch
WD = Wanddurchbruch
DD = Deckendurchbruch
BS = Bodenschlitz
WS = Wandschlitz
DS = Deckenschlitz
Schw. = Schwelle
n.G. = nächstes Geschoss
opt. = optional

- Massnahmen, welche zur Erzielung eines wasserdichten Betons vorgesehen werden, sind nach Angaben und Plänen des Systemgaranten auszuführen.
- Allfällige Änderungen der Schalungspläne sind mit der Bauleitung und dem Bauingenieur abzusprechen.

- Sämtliche Aussparungen siehe Spezialpläne. Nur für die Bewehrung massgebende Aussparungen sind eingezeichnet.
- Einlagen gemäss Plänen des Architekten und den Fachplanern.
- Einlagen, Tableaus, Ankerschienen, Lastösen in den Liftschächten gemäss Liftplaner /-hersteller
- Sämtliche Masse sind vor Baubeginn zu kontrollieren.
- Unstimmigkeiten sind umgehend der Bauleitung oder dem Architekten mitzuteilen.
- Nachbehandlung des Betons gemäss Absprache mit Bauleitung und Bauingenieur.
- Betonieren bei Frost gemäss separaten Anweisungen.

- Der Bauingenieur ist min. 24 Std. vor dem Betonieren für eine Bewehrungsabnahme zu verständigen.

- Betonkontrollen sind gemäss Kontrollplan durchzuführen.

- Der Baumeister darf keine Nachbesserung am Sichtbeton ausführen!
  Kaschieren von Kiesnestern, Wiederherstellen von ausgebrochenen Kanten
  nur in Absprache mit der Bauleitung.

- Details zur Ausführung der Schachtdeckel (Bodenplatte UG) sh. Fachplaner und/oder Architektenpläne

BFZ_51_BAI_SCN_100_133_SCH-EG-W+D-SN1 22731-133

Revisionen

Index	Ergänzungen / Änderungen

Zugehörige Listen:

Nr.	Inhalt:

Zugehörige Pläne:

Nr.	Inhalt
22731-131	Schalung Wände Grundriss
22731-132	Schalung Decke Grundriss
22731-134	Schalung Wände + Decke Schnitte 2
22731-126	Vorfabr. Stützen hexagonal
22731-127	Vorfabr. Stützen Abfanfung
22731-130	Vorfabr. Stützen

Übersicht

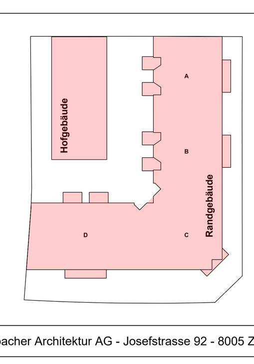

± 0.00 = 437.11 m ü.M

ARCHITEKT	Studio Esch Rickenbacher Architektur AG - Josefstrasse 92 - 8005 Zürich
BAUHERR	Terresta Immobilien- und Verwaltungs AG - Neuwiesenstrasse 15 - 8400 Winterthur
OBJEKT	Neubau - Binzmühle-/Friesstrasse - Zürich

Massstab	1:50
Plangrösse	1470 x 891

	Datum	gez.	gepr.
Erst.			
Rev.	05.02.2025	ras	mma

Erdgeschoss
Wände und Decke
Schnitteplan 1

Schalung, Schnitte

INGENIEUR
dsp Ingenieure + Planer AG
Zürichstrasse 4 CH-8610 Uster T +41(0)44 905 88 88 www.dsp.ch

Planstatus
Kontrollexemplar

Plannummer
22731-133

Projektpfad: L:\cad\nem\allplan\prj\22 731 Neubau Binzmühle-Friesstrasse Zürich CAD-Intern:133/senay.raimondi Plotdatum: 14.02.2025 Zeit: 14:53