Inhalt:	**Treppen_Schnitte 2-2; 3-3**
Plannummer:	**2306_A_ARC_DET_7303_41**

Projekt:	**2306; Überbauung Zwyssigmatte**	Massstab:	**1:20**
Adresse:	Zwyssigmatte, 6462 Seedorf	Kote:	± 0.00 Haus A = 444.0 m ü.M.
Phase:	Ausschreibung	Plangrösse:	89.1/84.0
Gezeichnet:	AKem	Datum:	19.11.2024

BauherrIn:
Zwyssigmatte AG
C/O Gipsergeschäft Franz Kempf AG
Gurtenmundstrasse 27
6460 Altdorf

AUSSCHREIBUNGSPLAN

ArchitektIn:
hts architektur ag
Hellgasse 23, 6460 Altdorf
Tel. 041 871 03 34
info@hts-architektur.ch
hts-architektur.ch

Sämtliche Masse sind Rohmasse und vom Unternehmer auf eigene Verantwortung zu prüfen und am Bau zu nehmem. Unstimmigkeiten müssen der Bauleitung gemeldet werden. Bei Sichtbeton ist das Rohmass zugleich das Fertigmass. Fensterhöhen ab OK. fertig Fensterbank bis UK fertig Sturz. Innere Türsturzhöhen ab fertig höherem Boden oder fertig Schwelle bis UK. roher Sturz. Raumhöhen im Licht ab fertig Boden bis UK. fertig Decke.

Planrevisionen:

Index: Datum: Änderungen:

hts architektur

hts architektur ag
Hellgasse 23
CH-6460 Altdorf
—
041 871 03 34
info@hts-architektur.ch
hts-architektur.ch

Planlegende:

	Beton tragend		Kalksandstein tragend		Holz
	Beton erdbebensicher		Kalksandstein nichttragend		Dämmstoffe
	Backstein tragend		Betonfertigelement		Naturstein
	Backstein nichttragend		Mörtel, Gips		Leichtbauwand

RH	Raumhöhe	OK.R.BR.	OK. Rohe Brüstung	K	Kurbel
D	Decke	OK.F.BR.	OK. Fertig Brüstung	M	Motor / Elektroantrieb
W	Wand	OK.SW.	OK. Schwelle	OL	Oblicht
B	Boden	OK.T.	OK. Terrain	FVT	Futter-und Verkleidungstüre
UK.R.D.	UK. Rohe Decke	MFB	Metallfensterbank	RT	Rahmentüre
OK.R.B.	OK. Roher Boden	BSW	Betonschwelle	ZT	Zargentüre
UK.R.ST.	UK. Roher Sturz	RAF	Raffl amellenstore	DW	Dachwasser
UK.F.ST.	UK. Fertig Sturz	SST	Sonnenstore (Markise)	BA	Bodenablauf

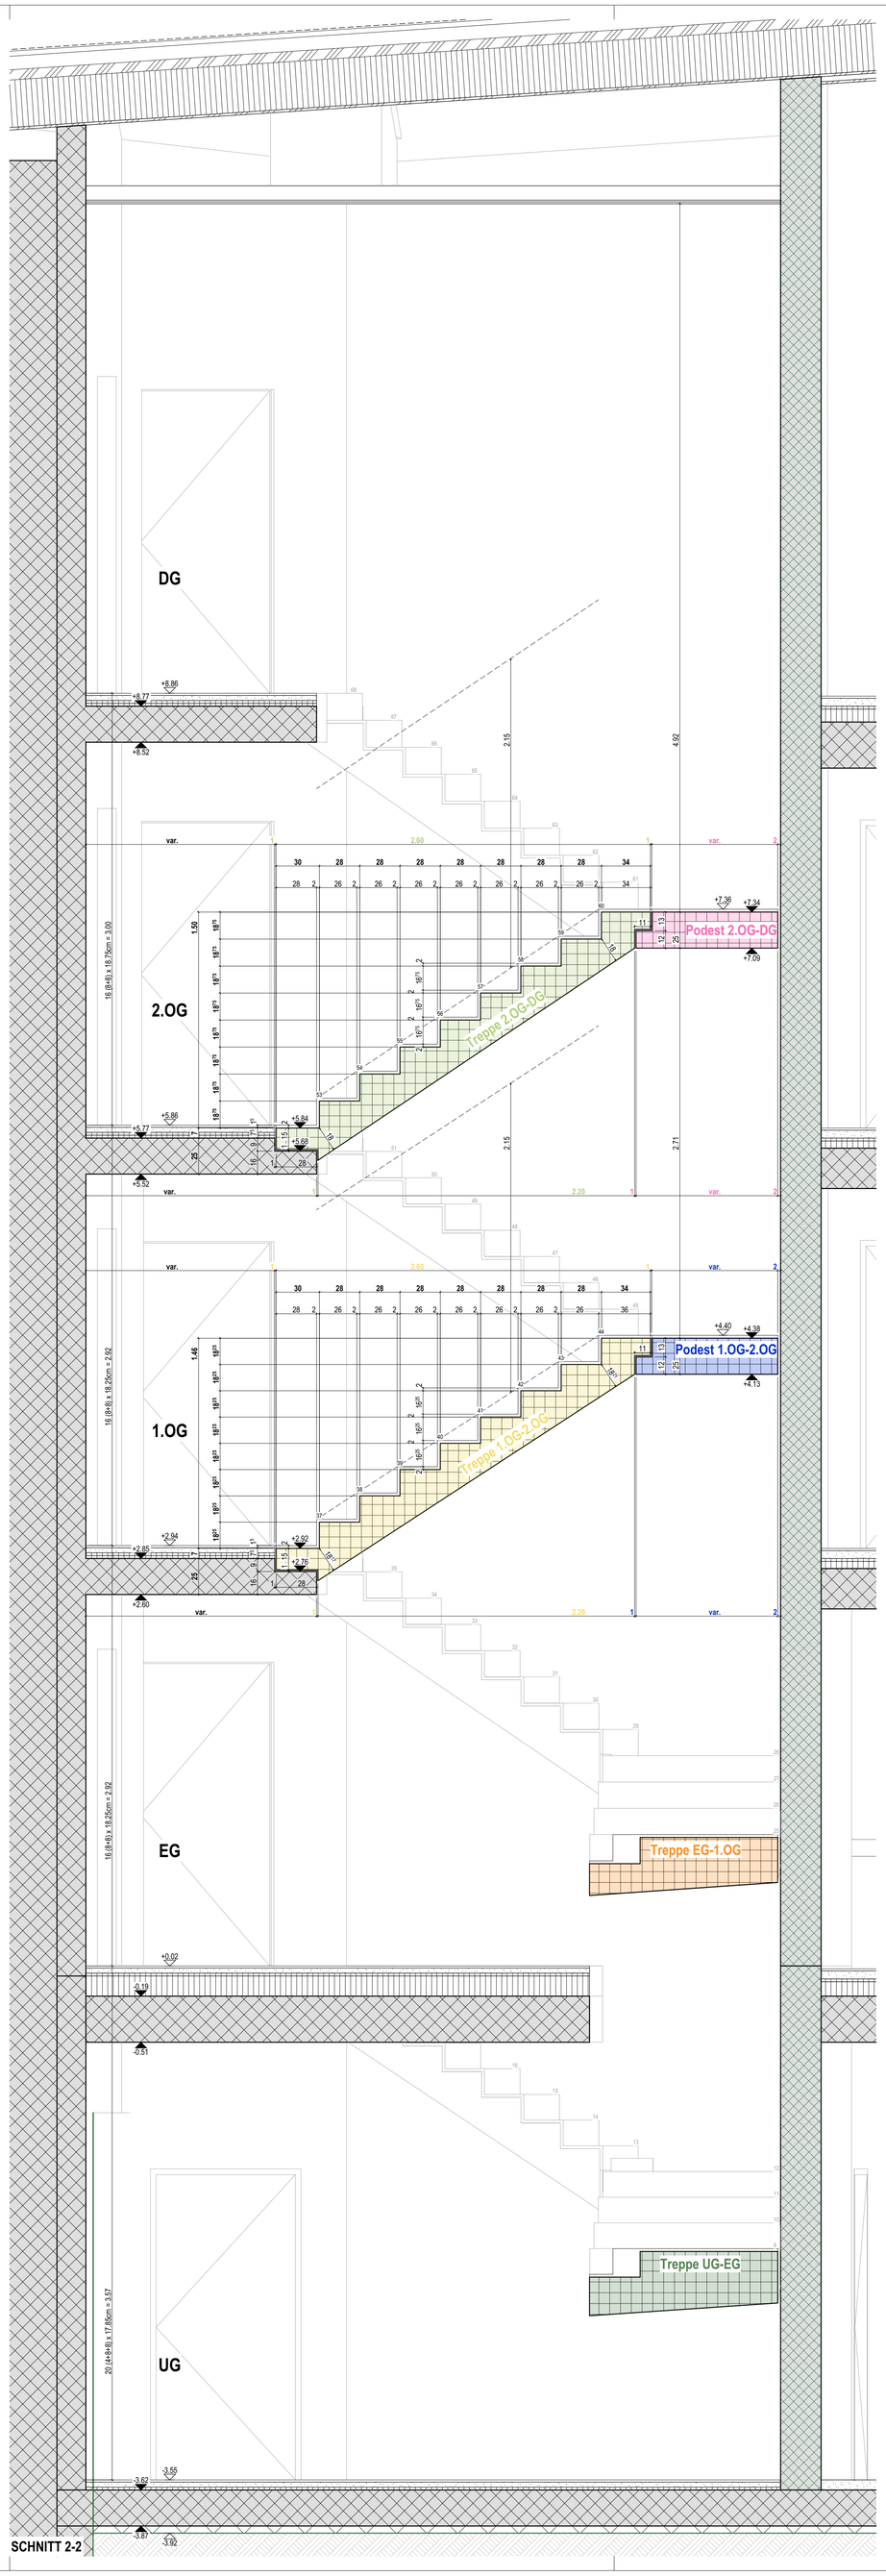

SCHNITT 2-2

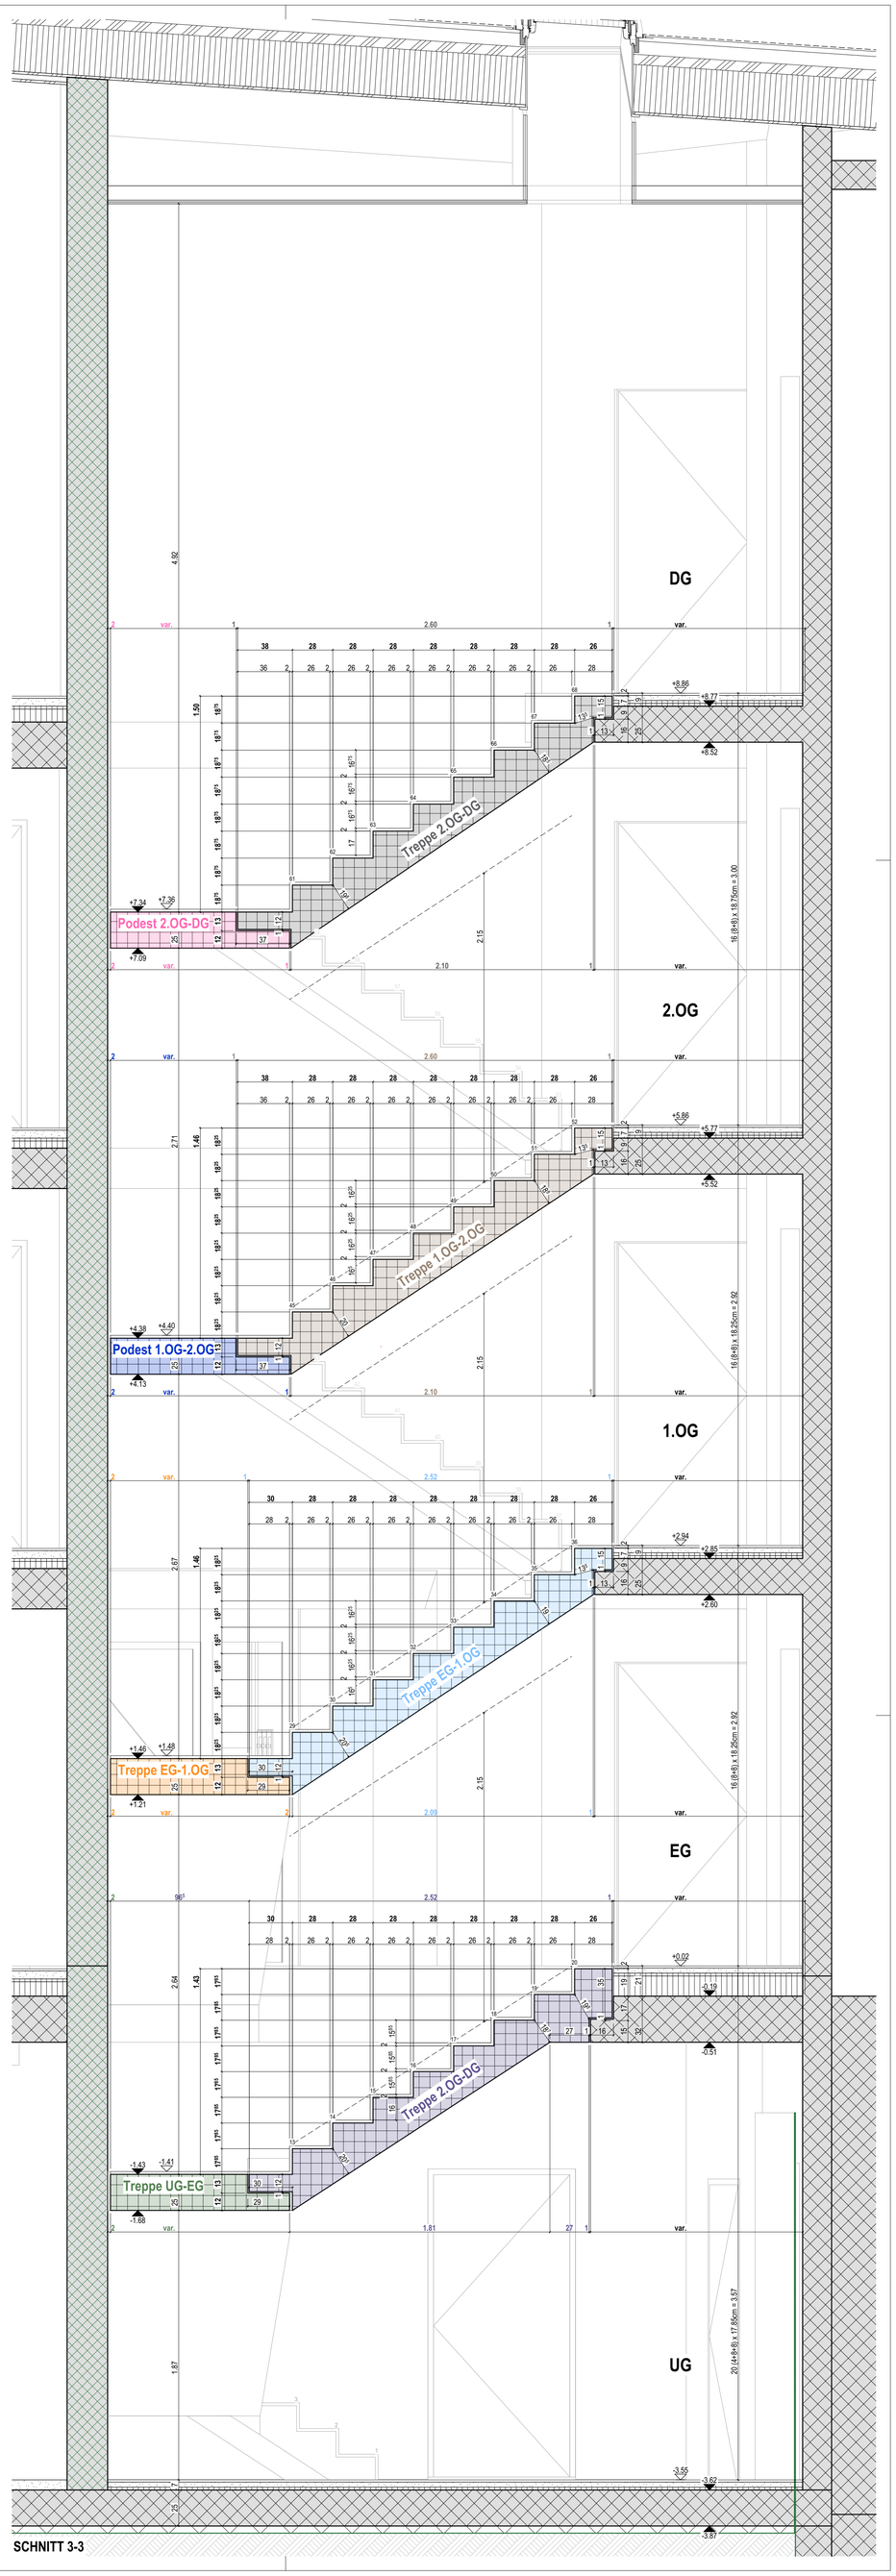

SCHNITT 3-3