
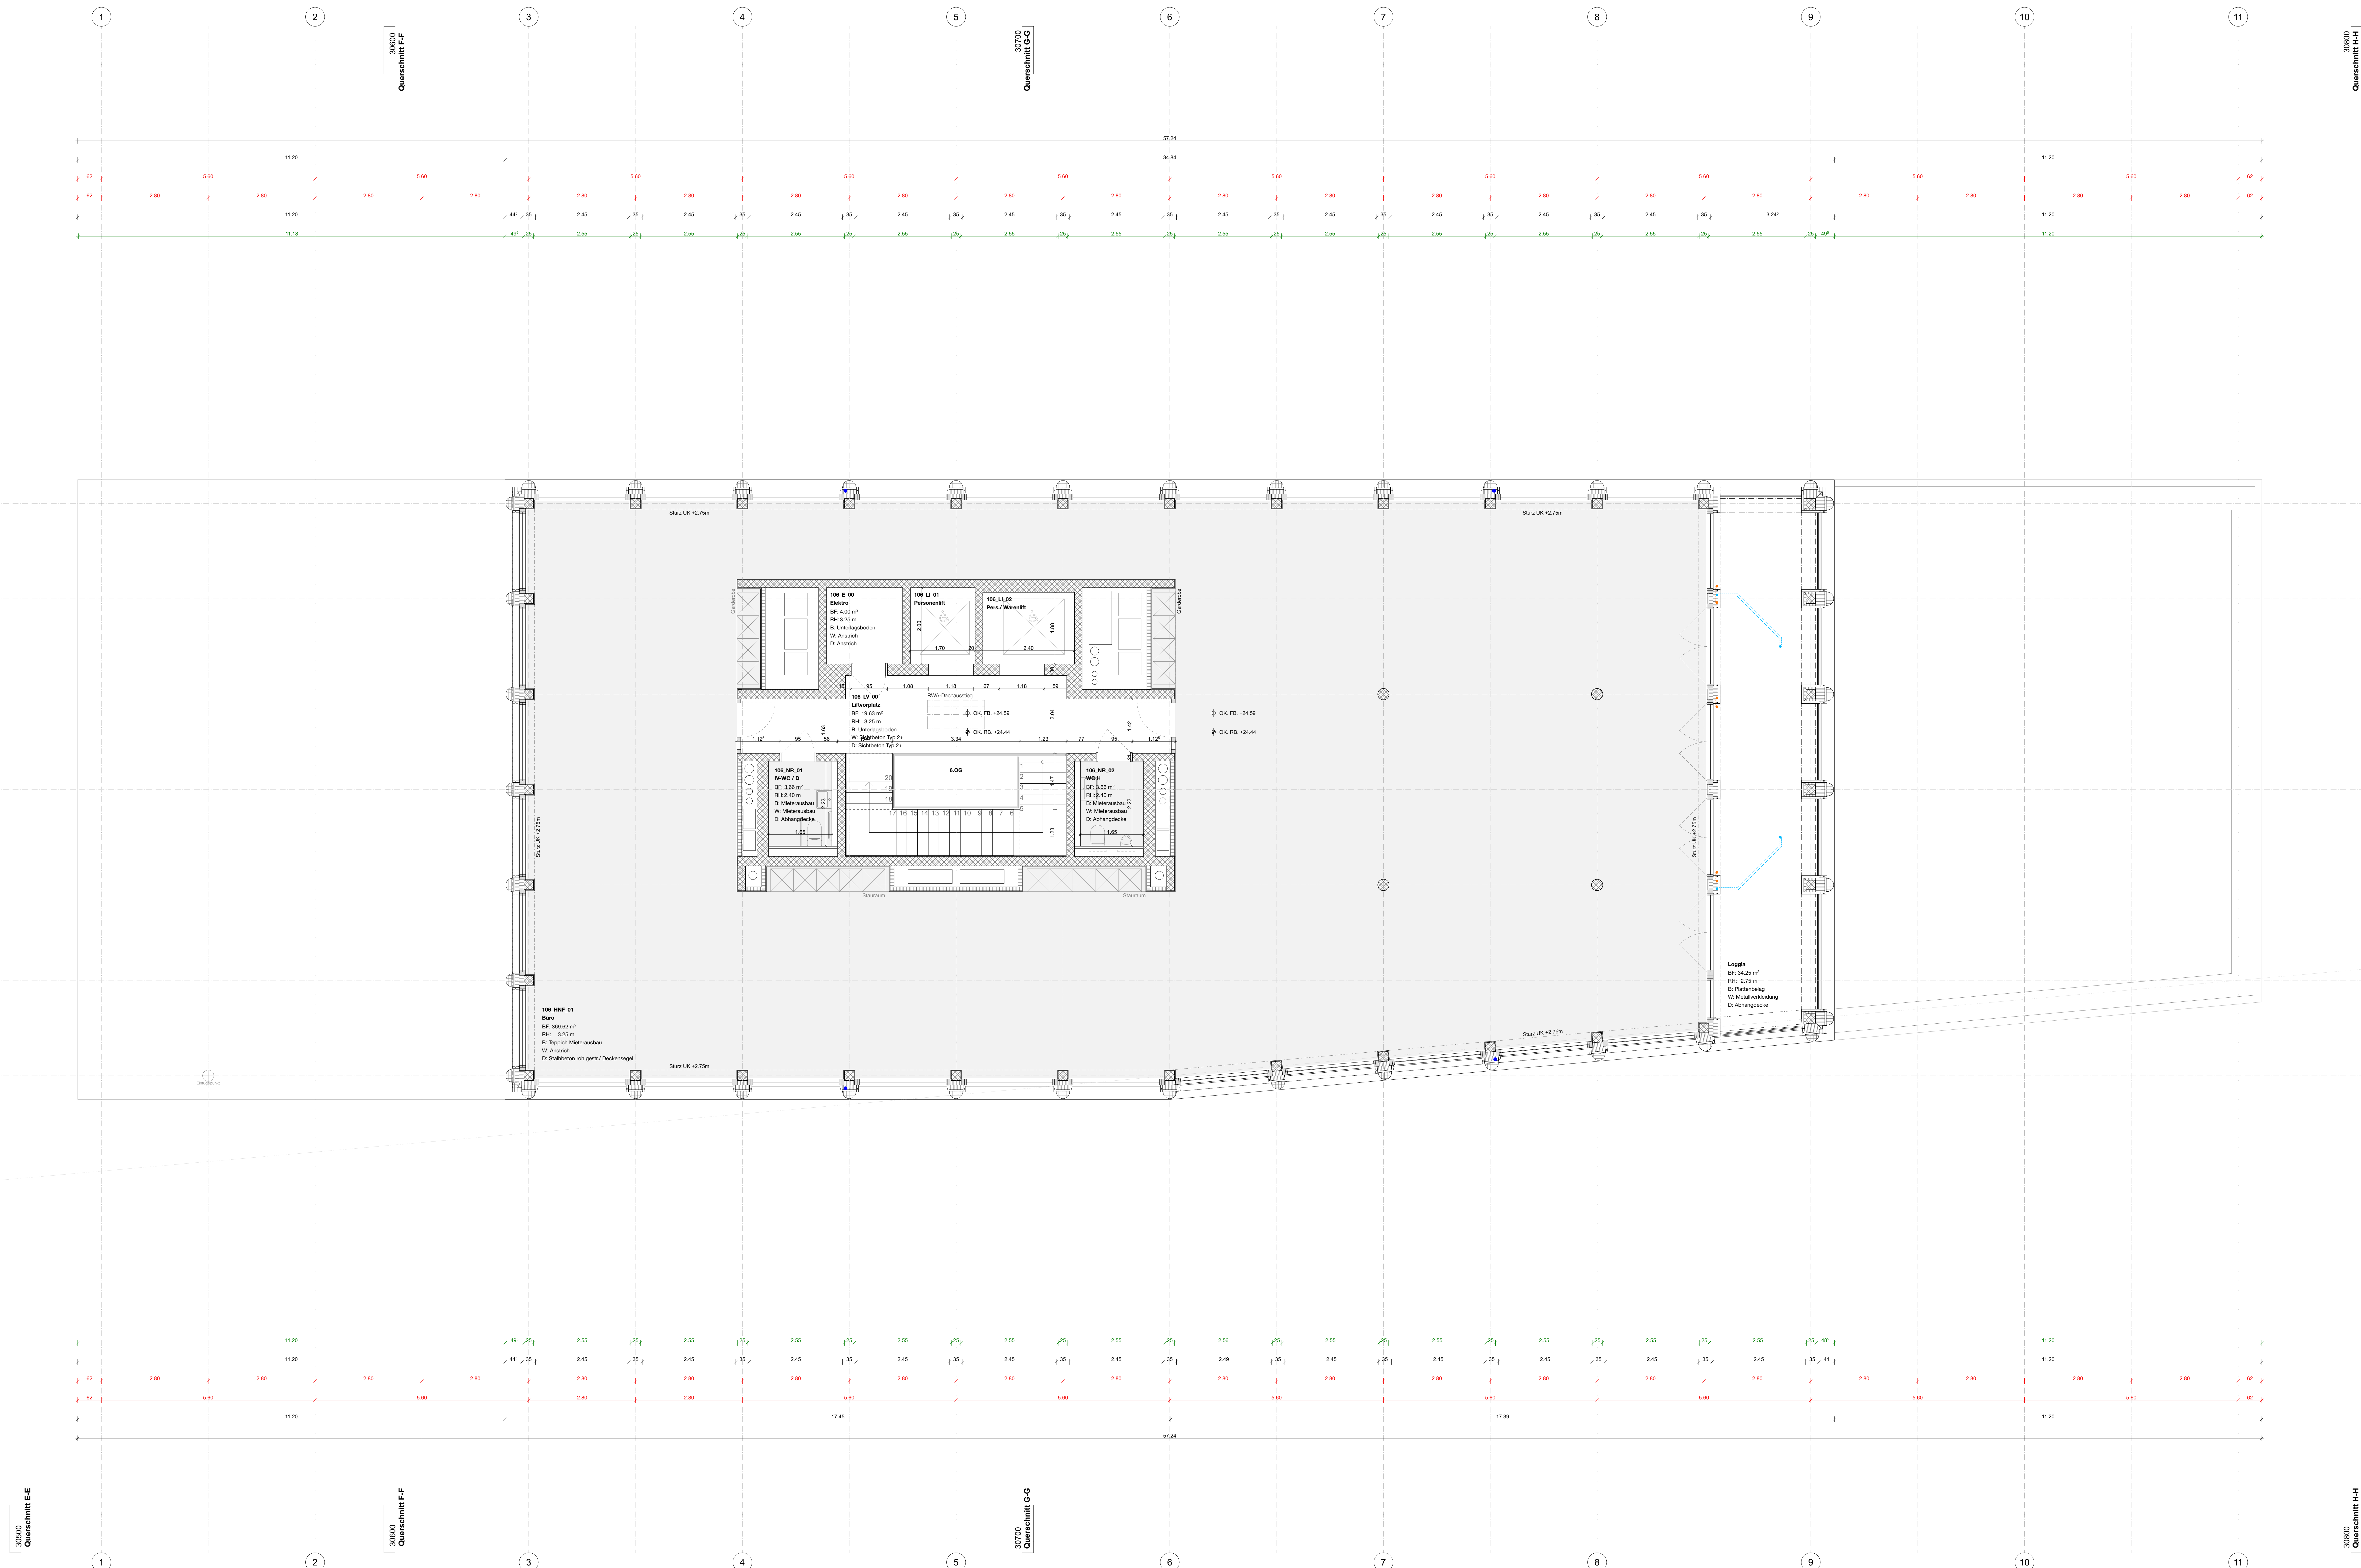
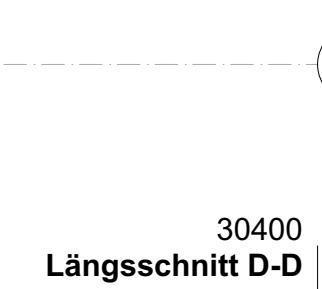


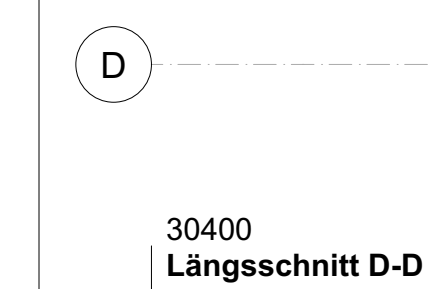

$\pm 0.00 = + 431.00 \text{ m ü. M.}$

Projekt: SGS Sanierung und Ersatzneubau Geschäftshaus Sägereistraße 27
Plan: OG06_Obergeschoss 06

Bauherrschaft: ALPINE IMMOBILIEN AG
Sägereistrasse 25, 8152 Glattbrugg, Schweiz
+41 (0) 44 809 50 00 - info@alpine-immo.ch

Totalunternehmer	WSG AG Sägereistrasse 29, 8152 Glattpburg, Schweiz +41 (0) 44 809 71 11 - info@wsg.ch
Finanzierungs-	MAX BLUE ED AG

Färberstrasse 6, 8008 Zürich, Schweiz +41 (0) 44 454 30 60 - info@maduedler.ch			
Datum / Gezeichnet	03.09.24 / gb	Massstab	1:50
Format	1850 x 891	Nr.	10800
Phase	32 Bauprojekt	Status	-
		Rev.	03.09.24 / -
		Index	-

Rev. 03.09.24 / -