


Bauer	Christian und Daniel Fokas Tel. 041 4431 56 46	Glattnestrasse 525 CH-8183 Rümling
Grundsteinleger	Heli Meier AG Tel. 041 4431 56 46	Eugen-Huber-Strasse 11 CH-8048 Zürich
Architekt	Fanzan AG Tel. 041 3172 88 88	Birmensdorfstrasse 108 CH-8003 Zürich info@fanzan.ch
Bauingenieur	Fanzan AG Tel. 041 3172 88 88	Birmensdorfstrasse 108 CH-8003 Zürich info@fanzan.ch
Sanitärinstallateur	Fanzan AG Tel. 041 3172 88 18	Lagerstr. 10 CH-8400 Winterthur info@fanzan.ch
Heizungs- und Klimaanlageningenieur	GRT Ingenieure GmbH Tel. 041 52 26 18 18	Lagerstr. 10 CH-8400 Winterthur info@grt.ch
Elektroingenieur	Artho Elektro GmbH Tel. 041 48 80 46 27	Zugerstrasse 59 CH-8802 Wädenswil ZH info@artho.ch
Basistyp	Fanzan AG Tel. 041 3172 88 88	Sahlgauerstrasse 64 CH-7000 Chur info@fanzan.ch
Bauleitung	Fanzan AG Tel. 041 3172 88 88	Sahlgauerstrasse 64 CH-7000 Chur info@fanzan.ch

29.07.2025 rev. 09.09.2025 | gez. vim | gep. gua | Format: 189x60 | Mst. 1:50

Hirweise

festigem, höherem Boden oder DK-Schwelle bis UK-roher Sturz vermasselt.

[illegible][illegible][illegible]